A2 PROSOIL	BOREHOLE NO: BH-1	
	LOCATION : C.S. & S.A. DAG NO. 513, MOUZA BARA ASHULIA, ASHULIA BAZAR, DHAKA.	
PROJECT : Proposed Six Storied Building.	DEPTH OF BORING : 21.0m	R. L.: 6.70m below from Road Level.
CLIENT : S.M. Amimul Ehsan.	DATE OF BORING : 10-01-2009.	G. W. T : 3.81m below from E. G. L.

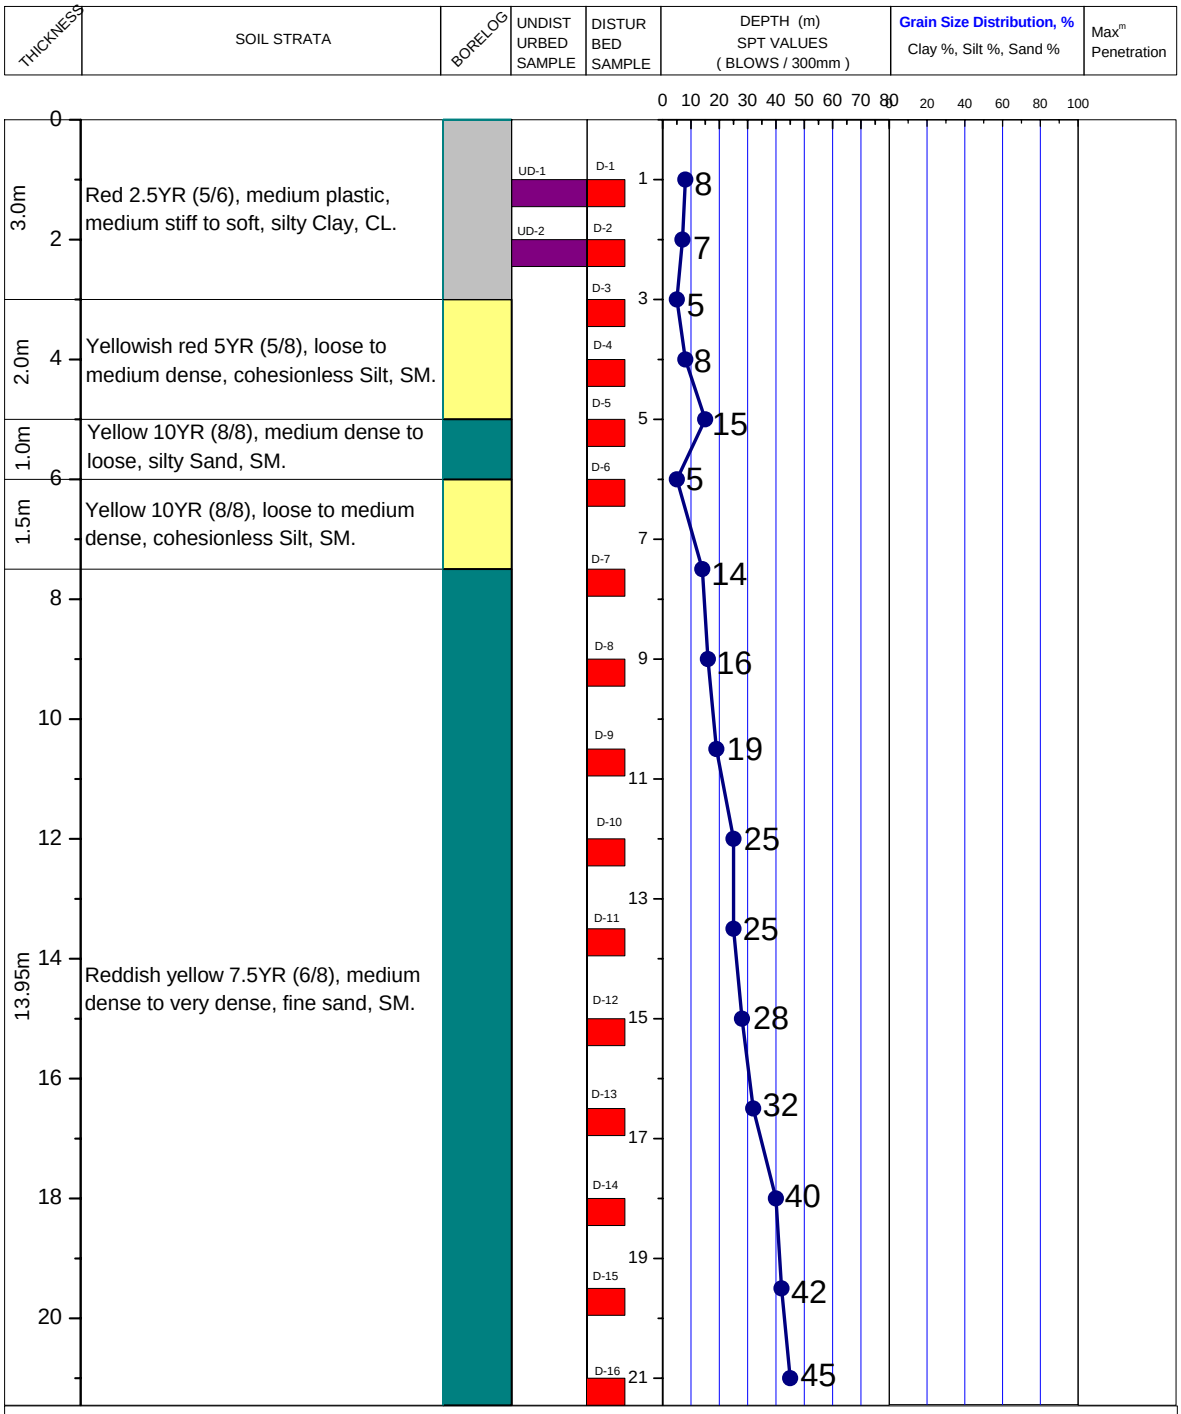

LEGEND FOR BORELOG AND GRAIN SIZE DISTRIBUTION

PLASTIC SILTY CLAY

LOW PLASTIC CLAYEY SILT

NON PLASTIC SILT

SAND

ORGANIC

UNDISTURBED SAMPLE

DISTURBED SAMPLE

SHALE

N- BLOWS DELIVERED PER FOOT BY A 140 LB HAMMER FALLING 30 INCHES

MAX^{m} PENETRATION= 50 BLOWS

AFTER 50 BLOWS PENETRATION DEPTH WERE MEASURED