A6	PROSOIL	BOREHOLE NO: BH-1 (SETTLEMENT CALCULATION)
		LOCATION : Meherpur, Golabganj, Sylhet. (24°43'19.8194"N, 92°02'08.9442"E).
PROJECT : Meherpur GPS, (Multi-purpose Cyclone Shelter/Govt. Primary School)		**SHALLOW FOOTING:** B: 0.6m, L=0.9m, P=100kpa
CLIENT : Us Army Corps Of Engr, Alaska District. THROUGH : AUSPICIOUS, QA Contractor.		**Shear failure Safety Factor=0.3**

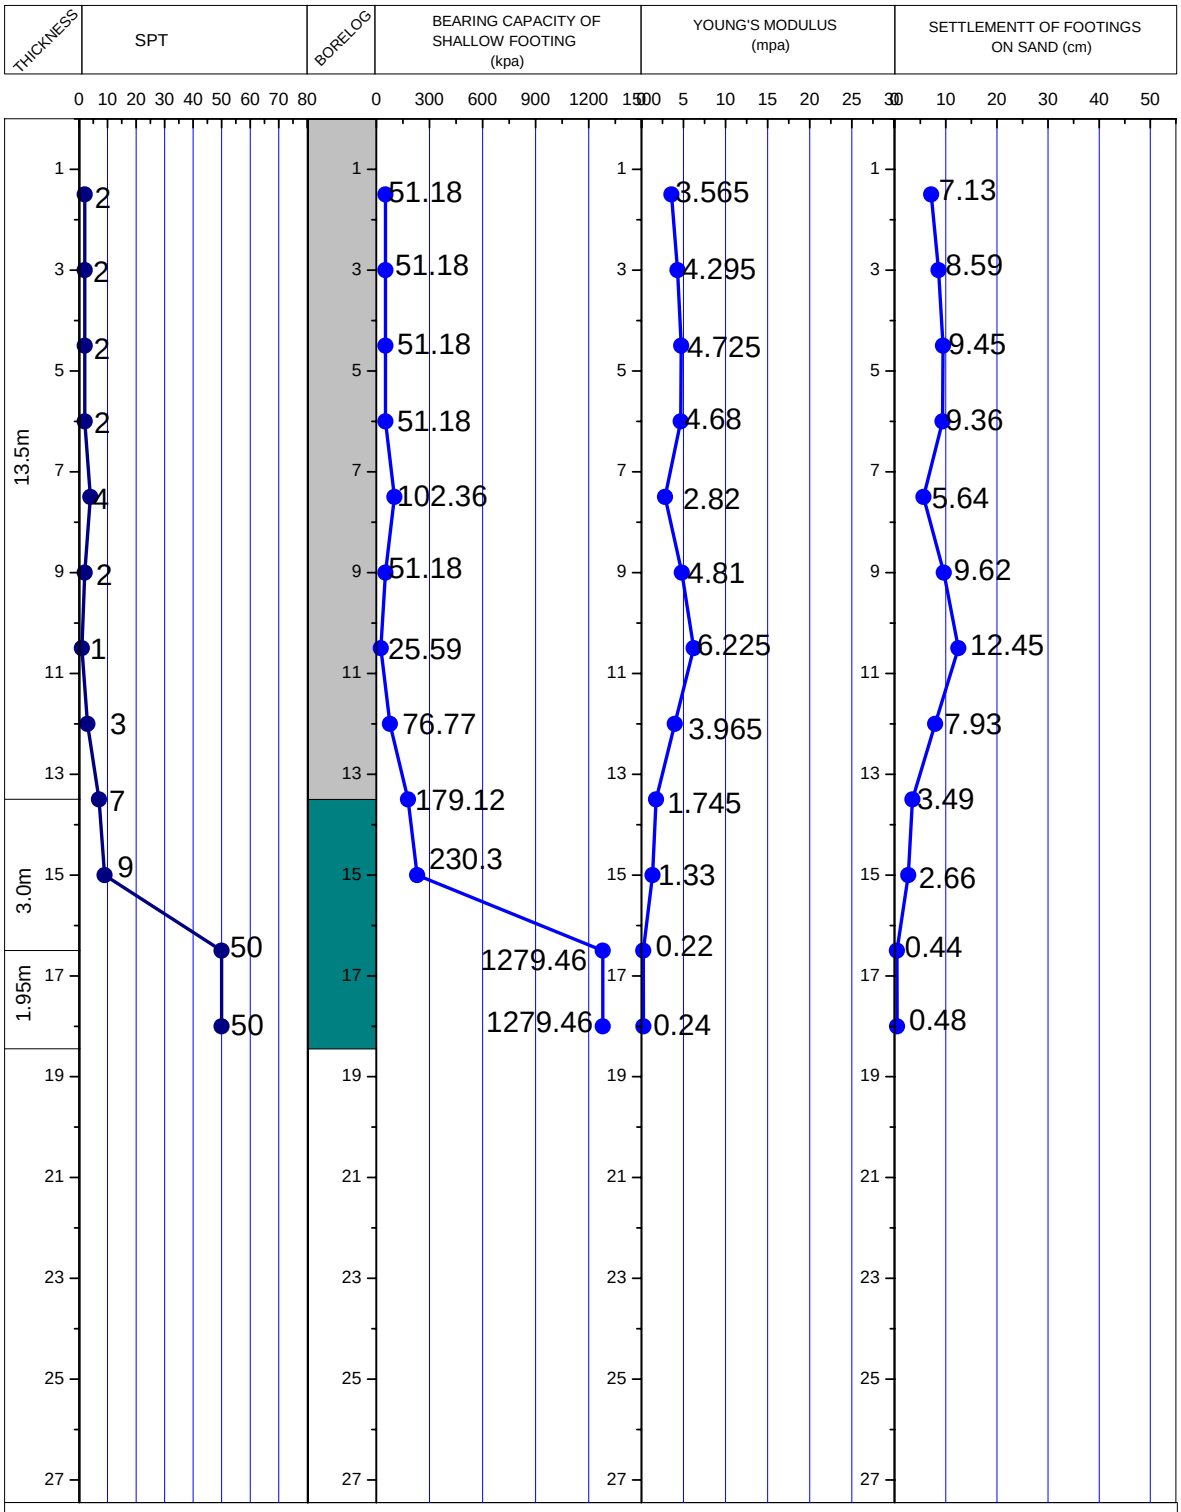

LEGEND FOR BOREHOLE AND GRAIN SIZE DISTRIBUTION (BASED ON 'ASTM CLASSIFICATION D-2487')

PLASTIC CLAY	SILT	SHALE	UNDISTURBED SAMPLE
MICACEOUS FINE SAND/SILT	SAND	PEAT/HIGHLY ORGANIC SOIL	

SETTLEMENT CALCULATION BY SOFTWARE: **NOVO SPT CORRELATION PROGRAM.**