
A2 PROSOIL	BOREHOLE NO: BH-1	
	LOCATION : Balabhadra Bridge at 25th km of Sarail-Nasirnagar-Lakhai Road, B.Baria.	
PROJECT : Proposed Balabhadra Bridge.	DEPTH OF BORING : 51.0m	Chainage: 25+540 R. L. : 7.20
CLIENT : Road Division, B.Baria.	DATE OF BORING : 05-10-2010.	G. W. T : 5.43m (RL).

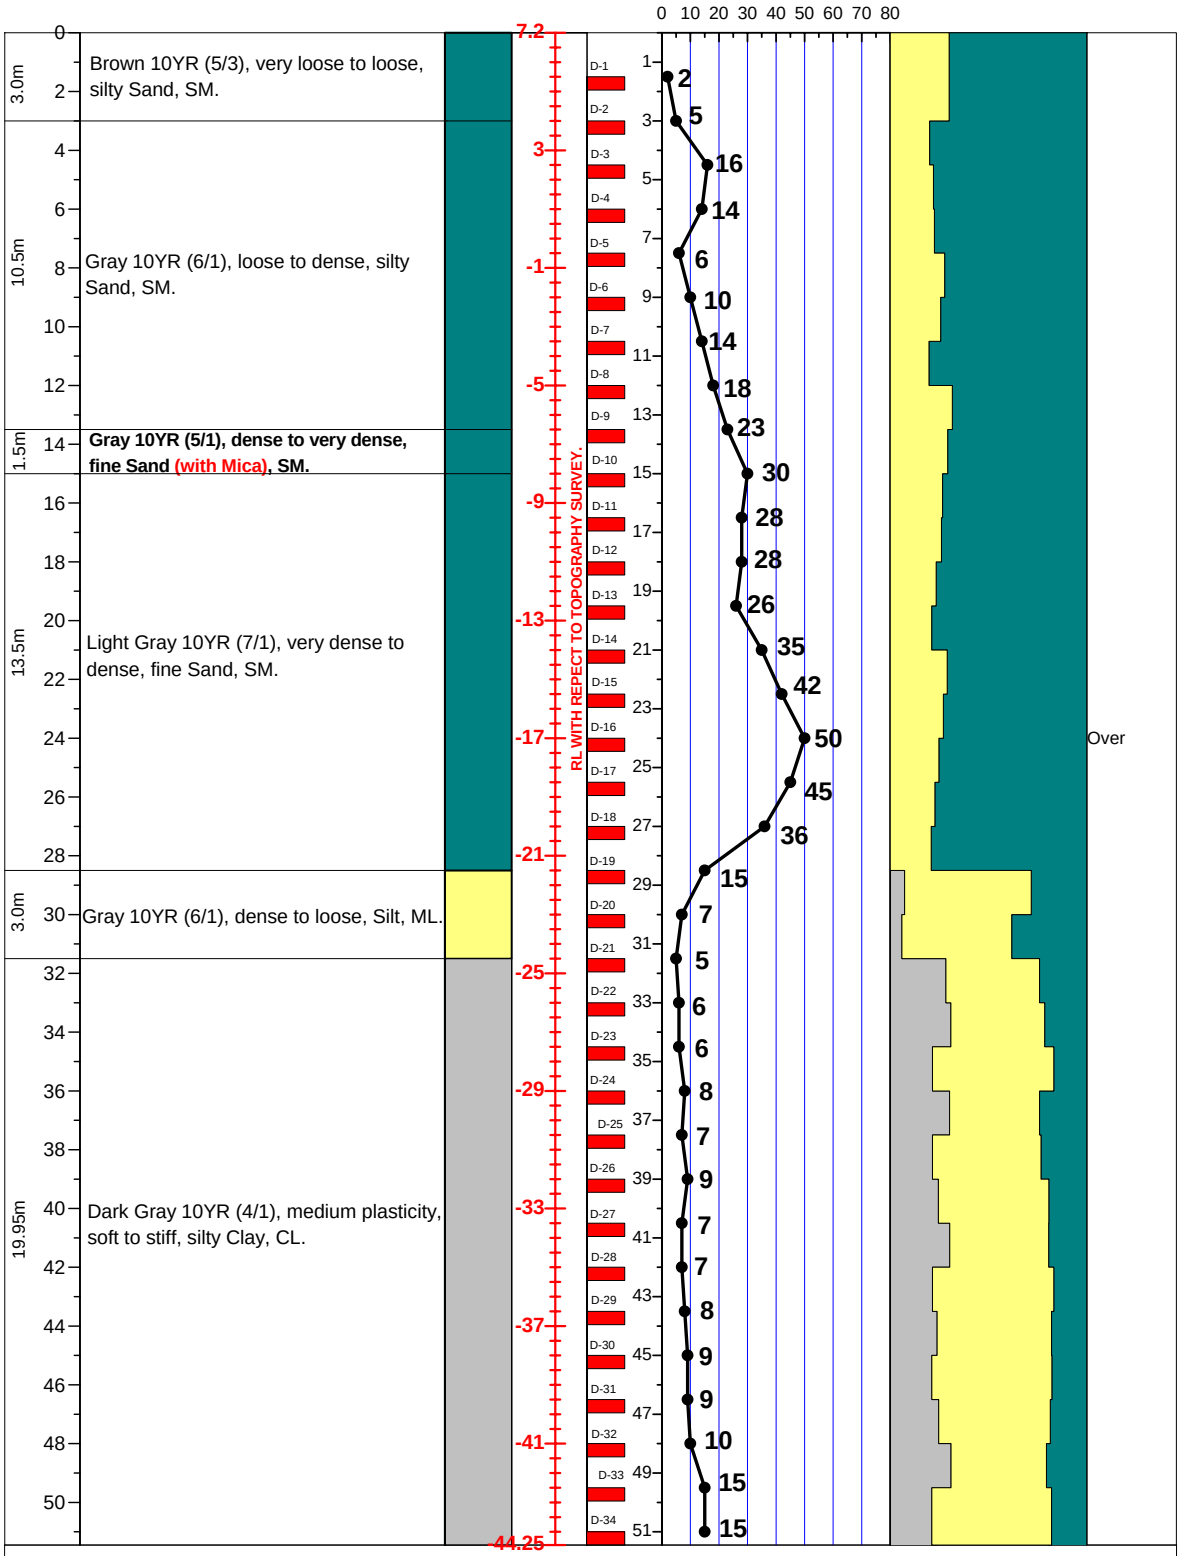

LEGEND FOR BOREHOLE AND GRAIN SIZE DISTRIBUTION (BASED ON 'ASTM CLASSIFICATION D-2487')

PLASTIC CLAY	SILT	PEAT/HIGHLY ORGANIC SOIL	UNDISTURBED SAMPLE
MICACEOUS FINE SAND/SILT	SAND	SHALE	DISTURBED SAMPLE

N- BLOWS DELIVERED PER FOOT BY A 140 LB HAMMER FALLING 30 INCHES

MAX^m PENETRATION= 50 BLOWS. AFTER 50 BLOWS PENETRATION DEPTH WERE MEASURED