A2	PROSOIL	BOREHOLE NO: BH-1	
		LOCATION : Nalka PGCL Complex, Sirajgonj.	
PROJECT : Proposed Head Office Building At Nalka PGCL Complex.		DEPTH OF BORING : 30.0m	R. L.: 1.06m below from Road Level.
CLIENT : PASHCHIMANCHAL GAS COMPANY LIMITED.		DATE OF BORING: 22-01-2013.	G. W. T : 6.40m below from E.G.L.

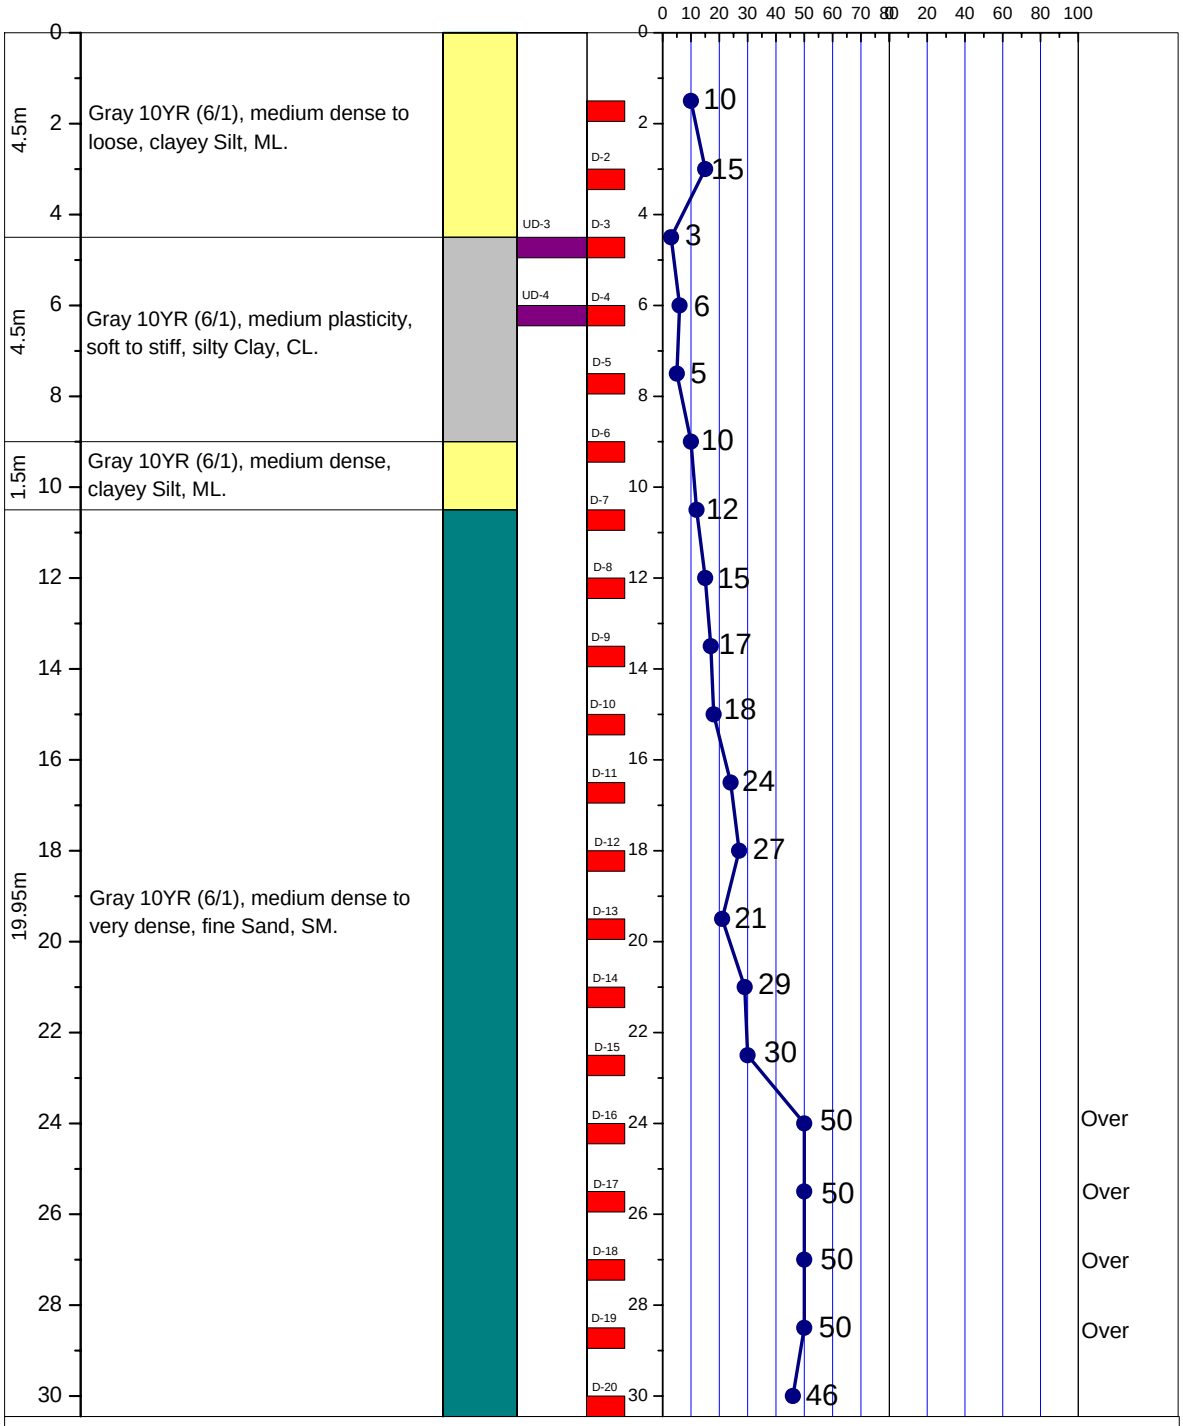

LEGEND FOR BORELOG AND GRAIN SIZE DISTRIBUTION (BASED ON 'ASTM CLASSIFICATION D-2487')

PLASTIC CLAY	SILT	SHALE	UNDISTURBED SAMPLE
MICACEOUS FINE SAND/SILT	SAND	PEAT/HIGHLY ORGANIC SOIL	DISTURBED SAMPLE

N- BLOWS DELIVERED PER FOOT BY A 140 LB HAMMER FALLING 30 INCHES

MAX^{m} PENETRATION= 50 BLOWS
AFTER 50 BLOWS PENETRATION DEPTH WERE MEASURED