
A2	PROSOIL	BOREHOLE NO: BH-1 (22°14'00.56" N, 90°49'26.92" E)	
		LOCATION: Chandpur Community, Lord Hardinj, Lalmohan, Bhola.	
PROJECT : Proposed 'Chandpur Community GPS', Multi-Purpose Cyclone Shelter/Govt. Primary School.		DEPTH OF BORING : 33.0m	R. L. : 1.0m below from Road Level.
CLIENT : US Army Corps Of Engineer, Alaska District. THROUGH : BFL-ACL-JV, DB CONTRACTOR.		DATE OF BORING: 15-03-2014 to 15-03-2014	B. W. T : 5.56m below from E.G.L.

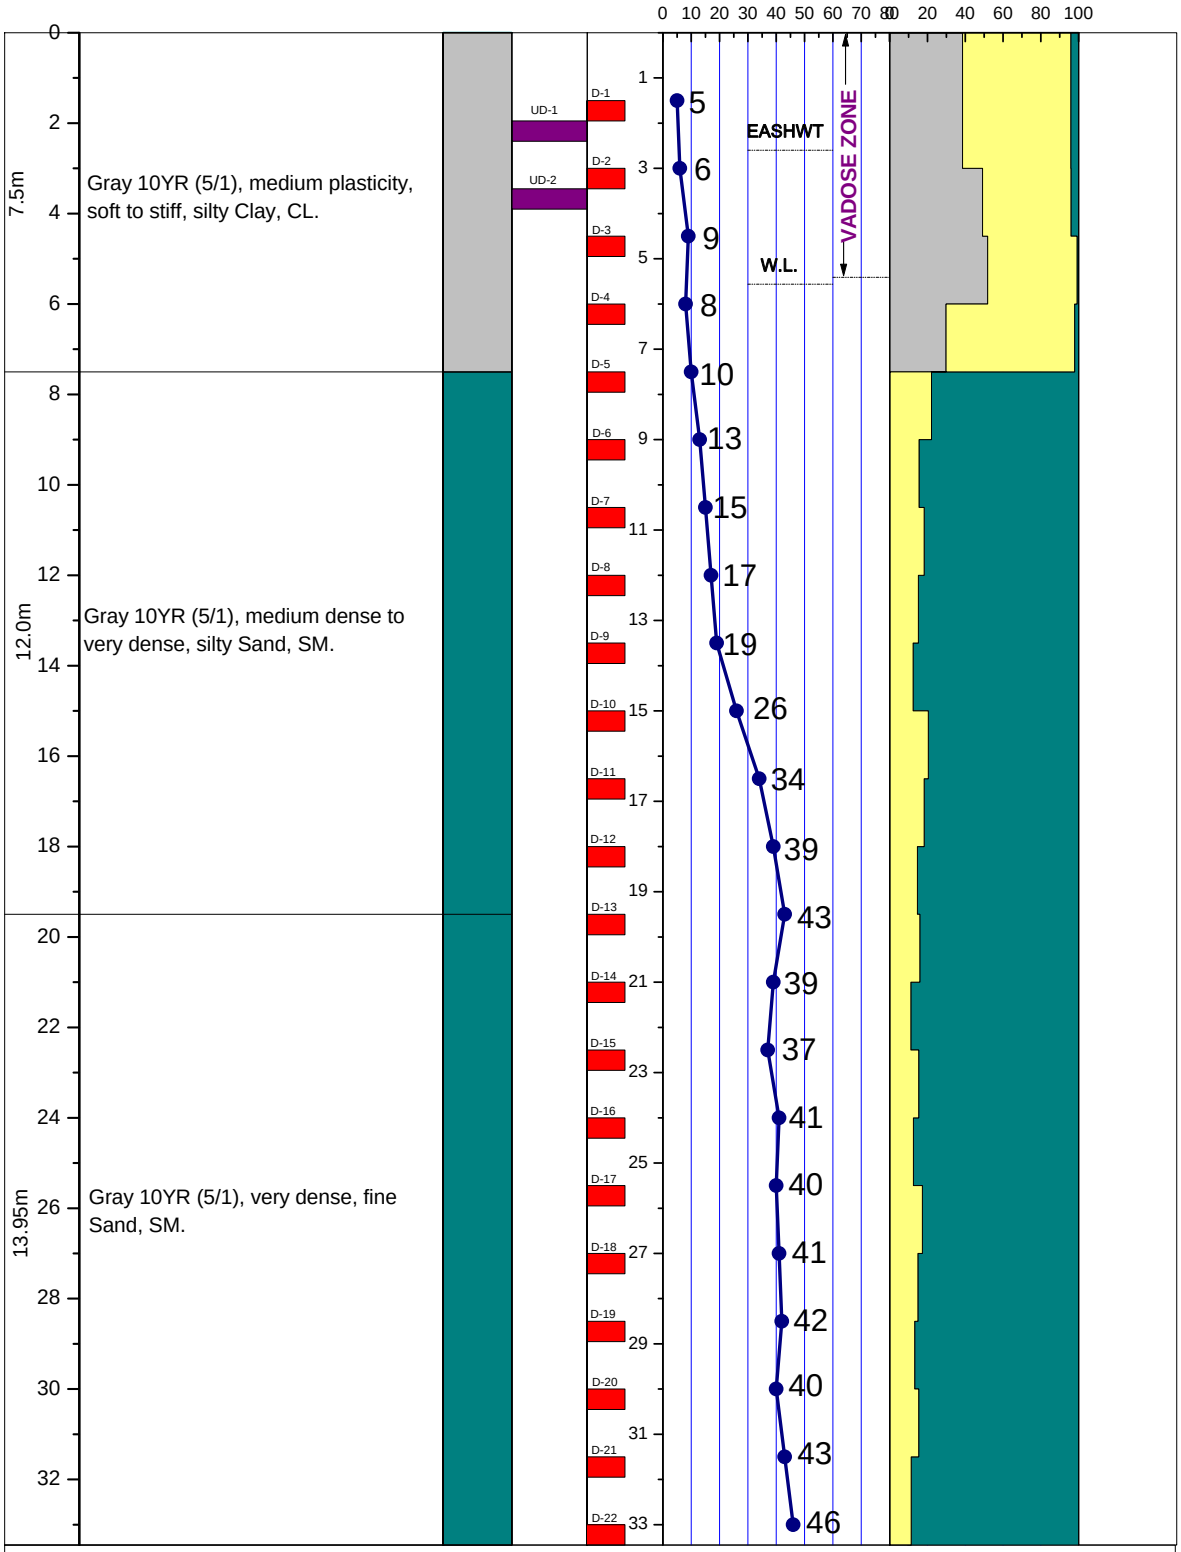

LEGEND FOR BORELOG AND GRAIN SIZE DISTRIBUTION (BASED ON 'ASTM CLASSIFICATION D-2487')

PLASTIC CLAY	SILT	PEAT/HIGHLY ORGANIC SOIL	UNDISTURBED SAMPLE
MICACEOUS FINE SAND/SILT	SAND	SHALE	DISTURBED SAMPLE

N- BLOWS DELIVERED PER FOOT BY A 140 LB HAMMER FALLING 30 INCHES

MAX^{m} PENETRATION= 50 BLOWS. AFTER 50 BLOWS PENETRATION DEPTH WERE MEASURED