A2 PROSOIL	BOREHOLE NO: BH1	
	LOCATION : Mollahat, Bagerhat.	
PROJECT : Telecommunication Tower	DEPTH OF BORING : 30.0m	R. L.: -0.61m from Road Level
CLIENT : GrameenPhone Ltd.	DATE OF BORING : 03-07-2004	G. W. T : -1.83m

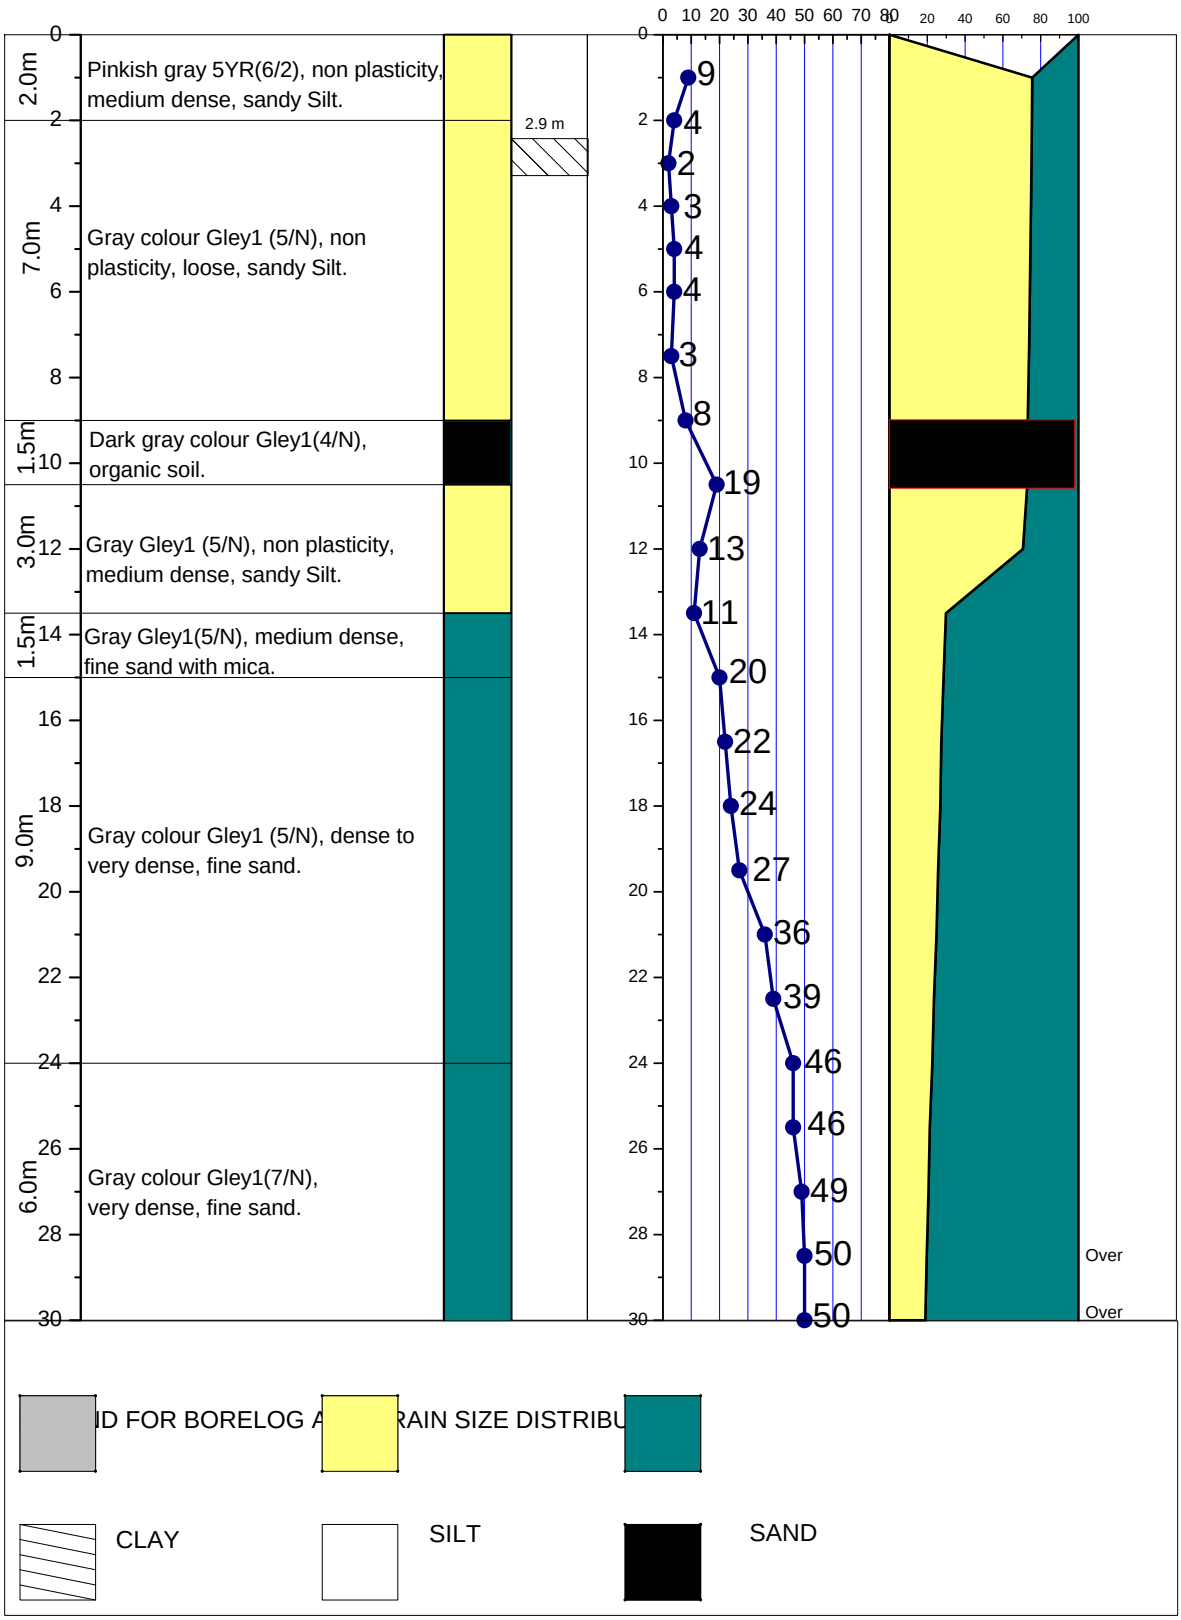

UNDISTURBED DISTURBED ORGANIC

N- BLOWS DELIVERED PER FOOT BY A 140 LB HAMMER FALLING 30 INCHES

MAX^{m} PENETRATION= 50 BLOWS

AFTER 50 BLOWS PENETRATION DEPTH WERE MEASURED