A2 PROSOIL	BOREHOLE NO: BH-1	
	LOCATION : Shantahar Rail Station, Bogra.	
PROJECT : Telecommunication Tower	DEPTH OF BORING : 20.0m	R. L.: -1.07m from Road Level.
CLIENT : GrameenPhone Ltd.	DATE OF BORING : 01-07-2004	G. W. T : -0.91m

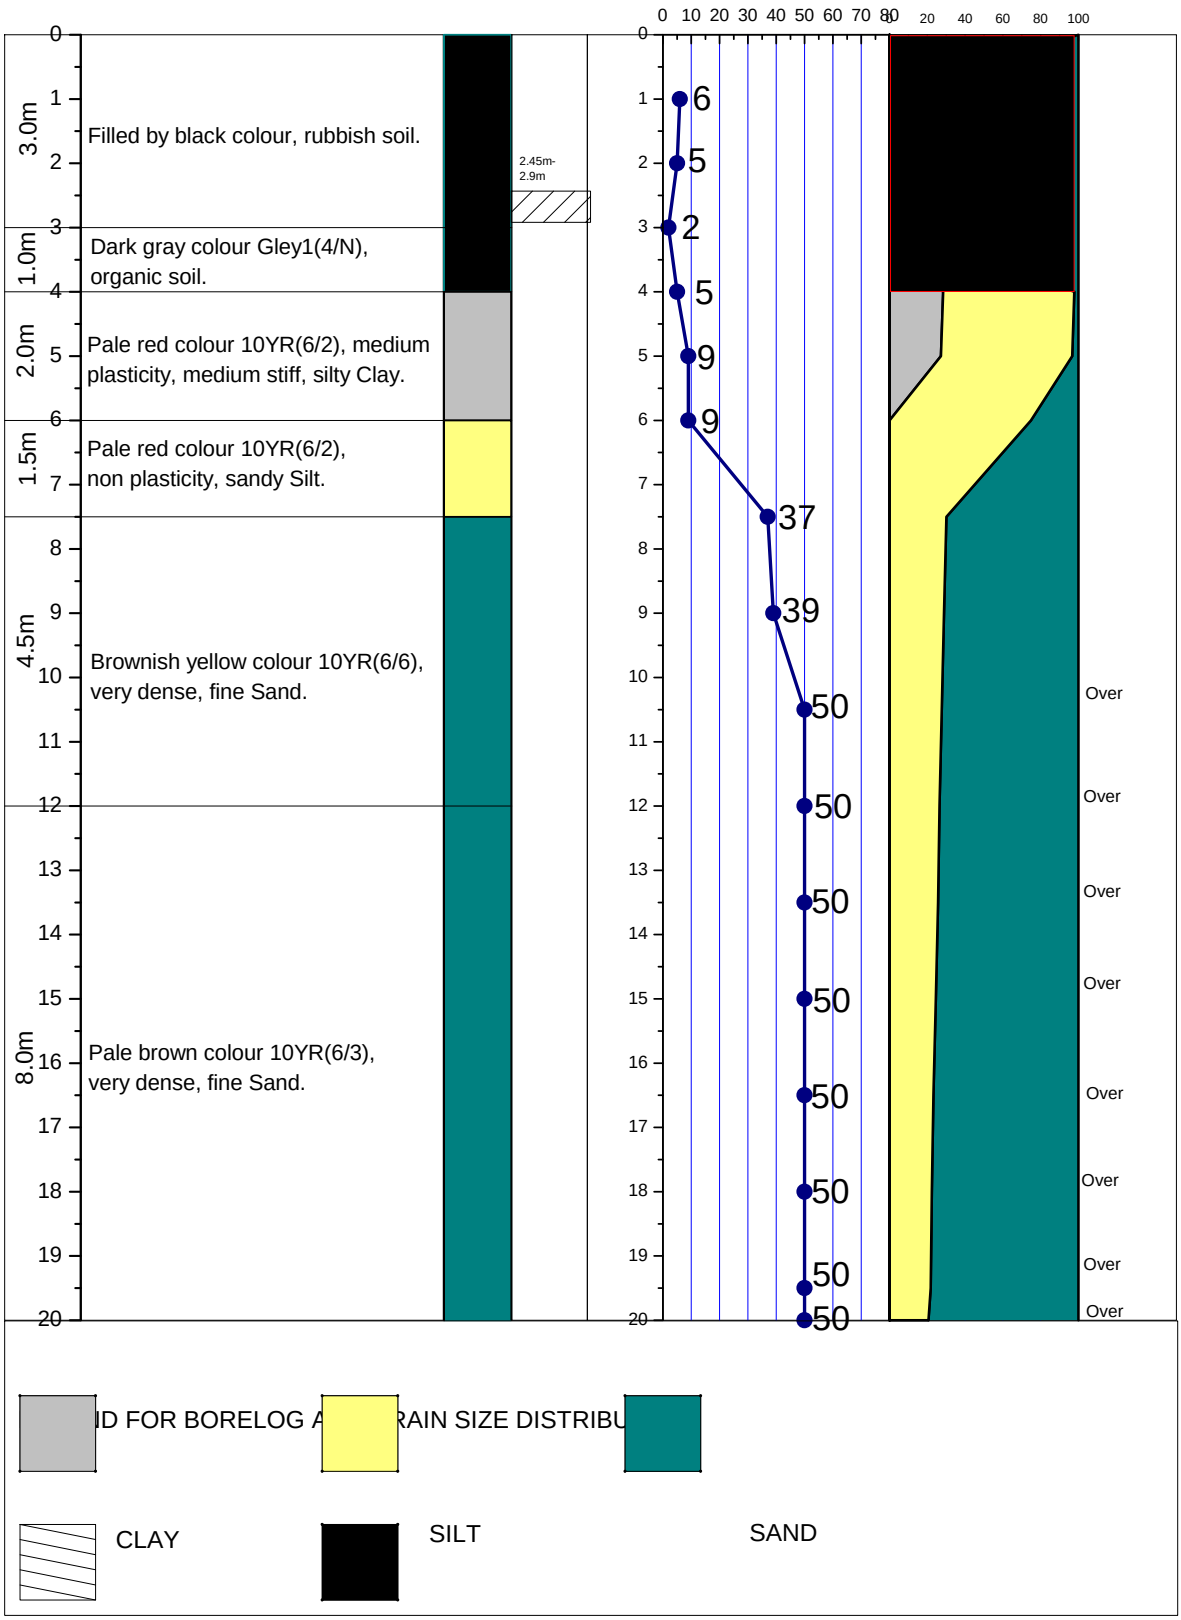

UNDISTURBED ORGANIC

N- BLOWS DELIVERED PER FOOT BY A 140 LB HAMMER FALLING 30 INCHES

MAX^{m} PENETRATION= 50 BLOWS

AFTER 50 BLOWS PENETRATION DEPTH WERE MEASURED