A2	Tarique Hasan & Associates Ltd.	BOREHOLE NO: 09	Easting: 223025.00	Northing: 2523284.00
		LOCATION : Barisal Airport, Barisal.		
PROJECT : Consultant Services for Development of Saidpur, Barisal and Osmani International Airport Projects (Design Phase)		DEPTH OF BORING : 15.0m		R. L. : 2.168m
CLIENT : Civil Aviation Authority of Bangladesh.		DATE OF BORING : 07-10-2018		B. W. T : 1.8 m below from E. G. L.

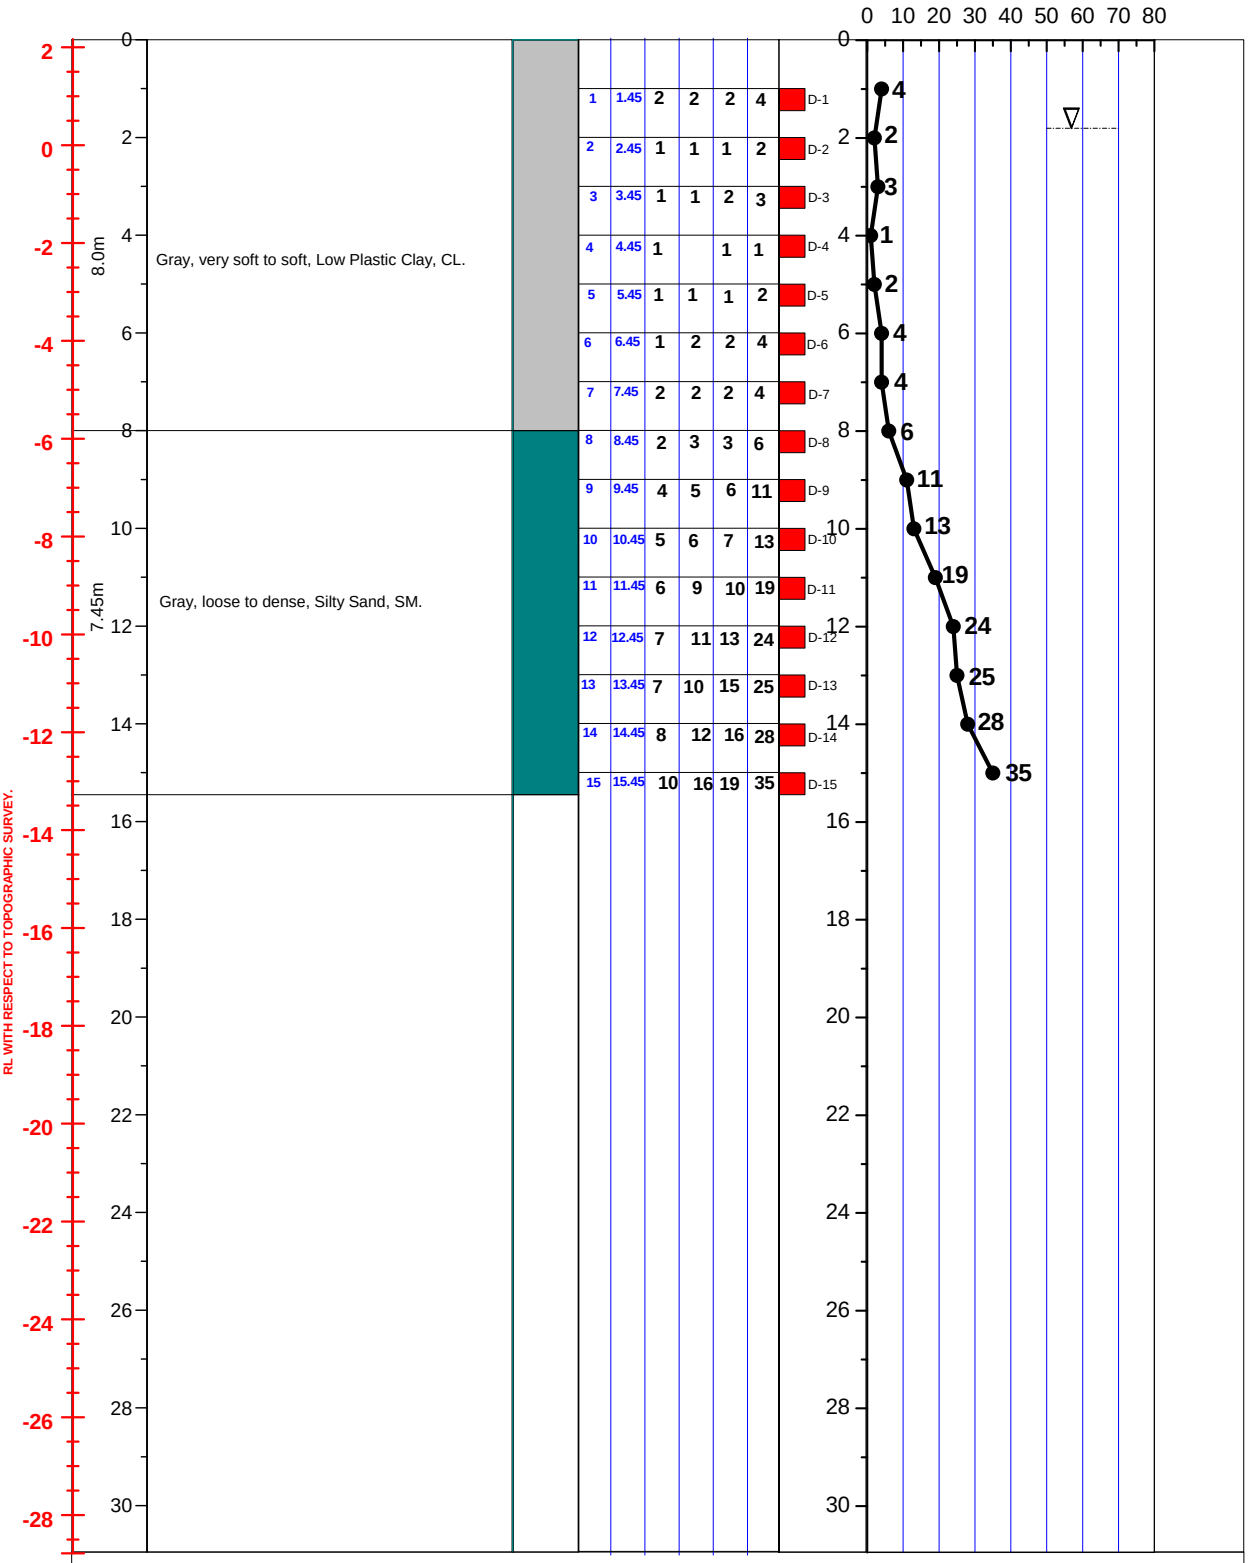

RL/ THICKNESS	SOIL STRATA	BORELOG	SAMPLING FROM (m)	SAMPLING TO (m)	SPT-N Value Blow/300mm N1=150 (mm)	N2=300 (mm)	N3=450 (mm)	N=N2 +N3	DISTURBED SAMPLE	DEPTH (m) SPT VALUES (BLOWS / 300mm)	Max^{m} Penetration
			1	1.45	2	2	2	4	D-1	4	
			2	2.45	1	1	1	2	D-2	2	
			3	3.45	1	1	2	3	D-3	3	
			4	4.45	1		1	1	D-4	1	
			5	5.45	1	1	1	2	D-5	2	
			6	6.45	1	2	2	4	D-6	4	
			7	7.45	2	2	2	4	D-7	4	
			8	8.45	2	3	3	6	D-8	6	
			9	9.45	4	5	6	11	D-9	11	
			10	10.45	5	6	7	13	D-10	13	
			11	11.45	6	9	10	19	D-11	19	
			12	12.45	7	11	13	24	D-12	24	
			13	13.45	7	10	15	25	D-13	25	
			14	14.45	8	12	16	28	D-14	28	
			15	15.45	10	16	19	35	D-15	35	

LEGEND FOR BOREHOLE AND GRAIN SIZE DISTRIBUTION (BASED ON 'ASTM CLASSIFICATION D-2487')

PLASTIC CLAY | SILT | PEAT/HIGHLY ORGANIC SOIL | UNDISTURBED SAMPLE

MICACEOUS FINE SAND/SILT | SAND | SHALE | DISTURBED SAMPLE

N- BLOWS DELIVERED PER FOOT BY A 140 LB HAMMER FALLING 30 INCHES

MAX^{m} PENETRATION= 50 BLOWS. AFTER 50 BLOWS PENETRATION DEPTH WERE MEASURED