A2 PROSOIL	BOREHOLE NO: BH-1	
	LOCATION : House #04, Road #8/A, Baridhara, Dhaka.	
PROJECT : Proposed Ten Storied Building.	DEPTH OF BORING : 30.0m	R. L.: On Road Level.
CLIENT : Building Technology & Ideas Ltd.	DATE OF BORING: 16-06-2010.	G. W. T : 0.31m below from E.G.L.

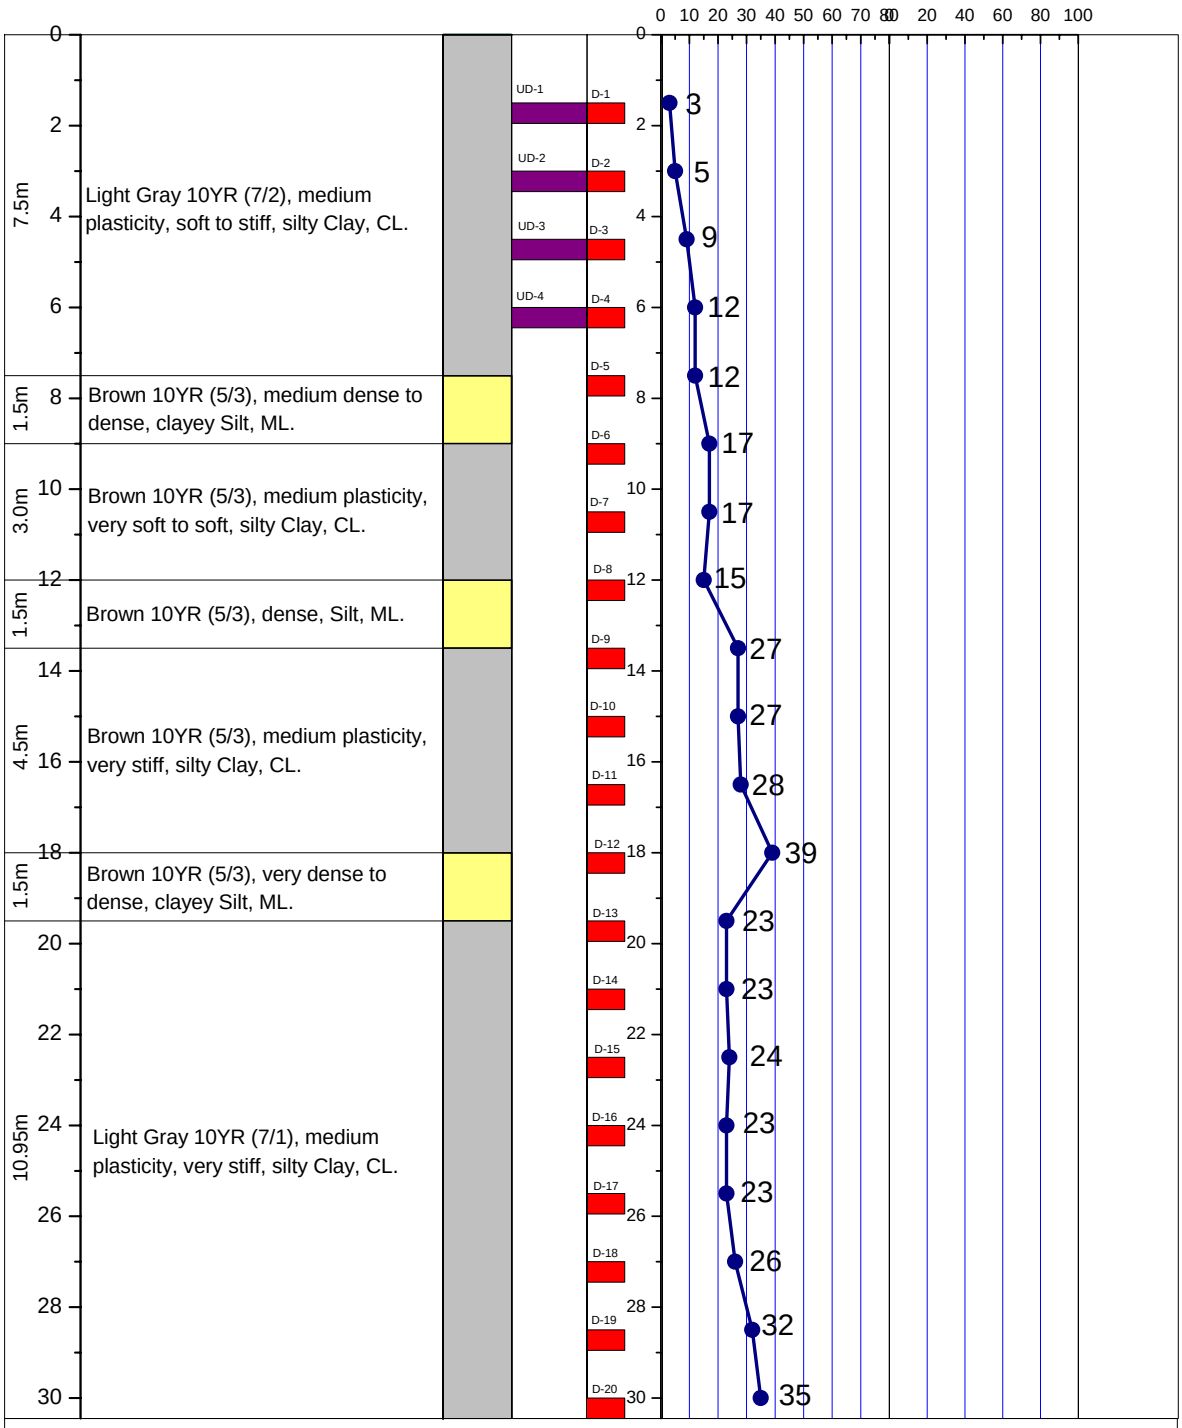

LEGEND FOR BORELOG AND GRAIN SIZE DISTRIBUTION (BASED ON 'ASTM CLASSIFICATION D-2487')

PLASTIC CLAY	SILT	SHALE	UNDISTURBED SAMPLE
MICACEOUS FINE SAND/SILT	SAND	PEAT/HIGHLY ORGANIC SOIL	DISTURBED SAMPLE

N- BLOWS DELIVERED PER FOOT BY A 140 LB HAMMER FALLING 30 INCHES

MAX^{m} PENETRATION= 50 BLOWS
AFTER 50 BLOWS PENETRATION DEPTH WERE MEASURED