A2	PROSOIL	BOREHOLE NO: BH-1	
		LOCATION : 2nd k.m. (Ch. 1+760 to 1+790) of Porshuram guthuma-(abdul aziz BA) Road.	
PROJECT : Proposed 35.0m Bridge.		DEPTH OF BORING : 42.0m	Chainage: 1+757 R. L. : 6.050
CLIENT : Road Division, Feni.		DATE OF BORING : 05-10-2013 to 06-10-2013.	G. W. T : 1.83m below from E.G.L.

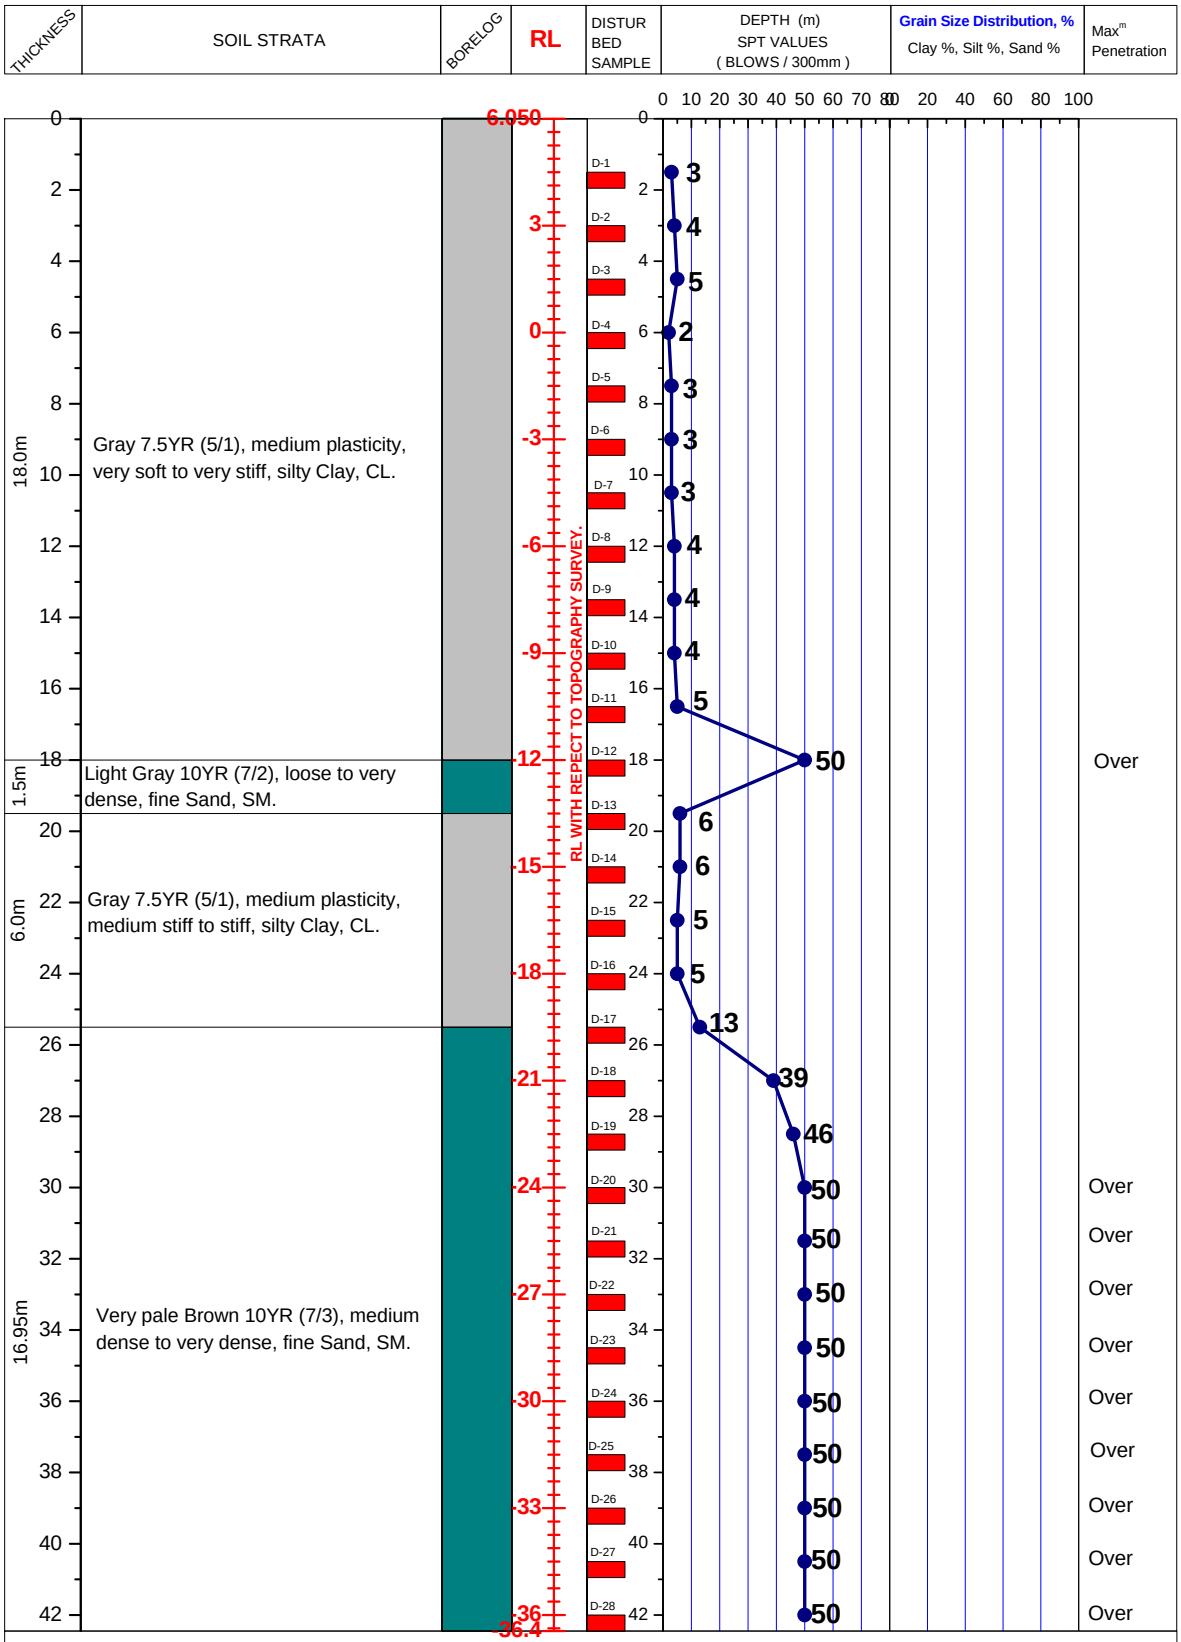

LEGEND FOR BOREHOLE AND GRAIN SIZE DISTRIBUTION (BASED ON 'ASTM CLASSIFICATION D-2487')

PLASTIC CLAY	SILT	PEAT/HIGHLY ORGANIC SOIL	UNDISTURBED SAMPLE
MICACEOUS FINE SAND/SILT	SAND	SHALE	DISTURBED SAMPLE

N- BLOWS DELIVERED PER FOOT BY A 140 LB HAMMER FALLING 30 INCHES

MAX^m PENETRATION= 50 BLOWS. AFTER 50 BLOWS PENETRATION DEPTH WERE MEASURED