
A2 PROSOIL	BOREHOLE NO: BH-1	
	LOCATION : Asad Bapari Road, Auch para, Tongi Pourosobha.	
PROJECT : Proposed Six Storied Building.	DEPTH OF BORING : 15.0m	R. L.: Road Level.
CLIENT : Syed Ahmed Khondoker and Hosnei Ara Begum.	DATE OF BORING : 19-09-2008.	G. W. T : 0.61m below from E. G. L.

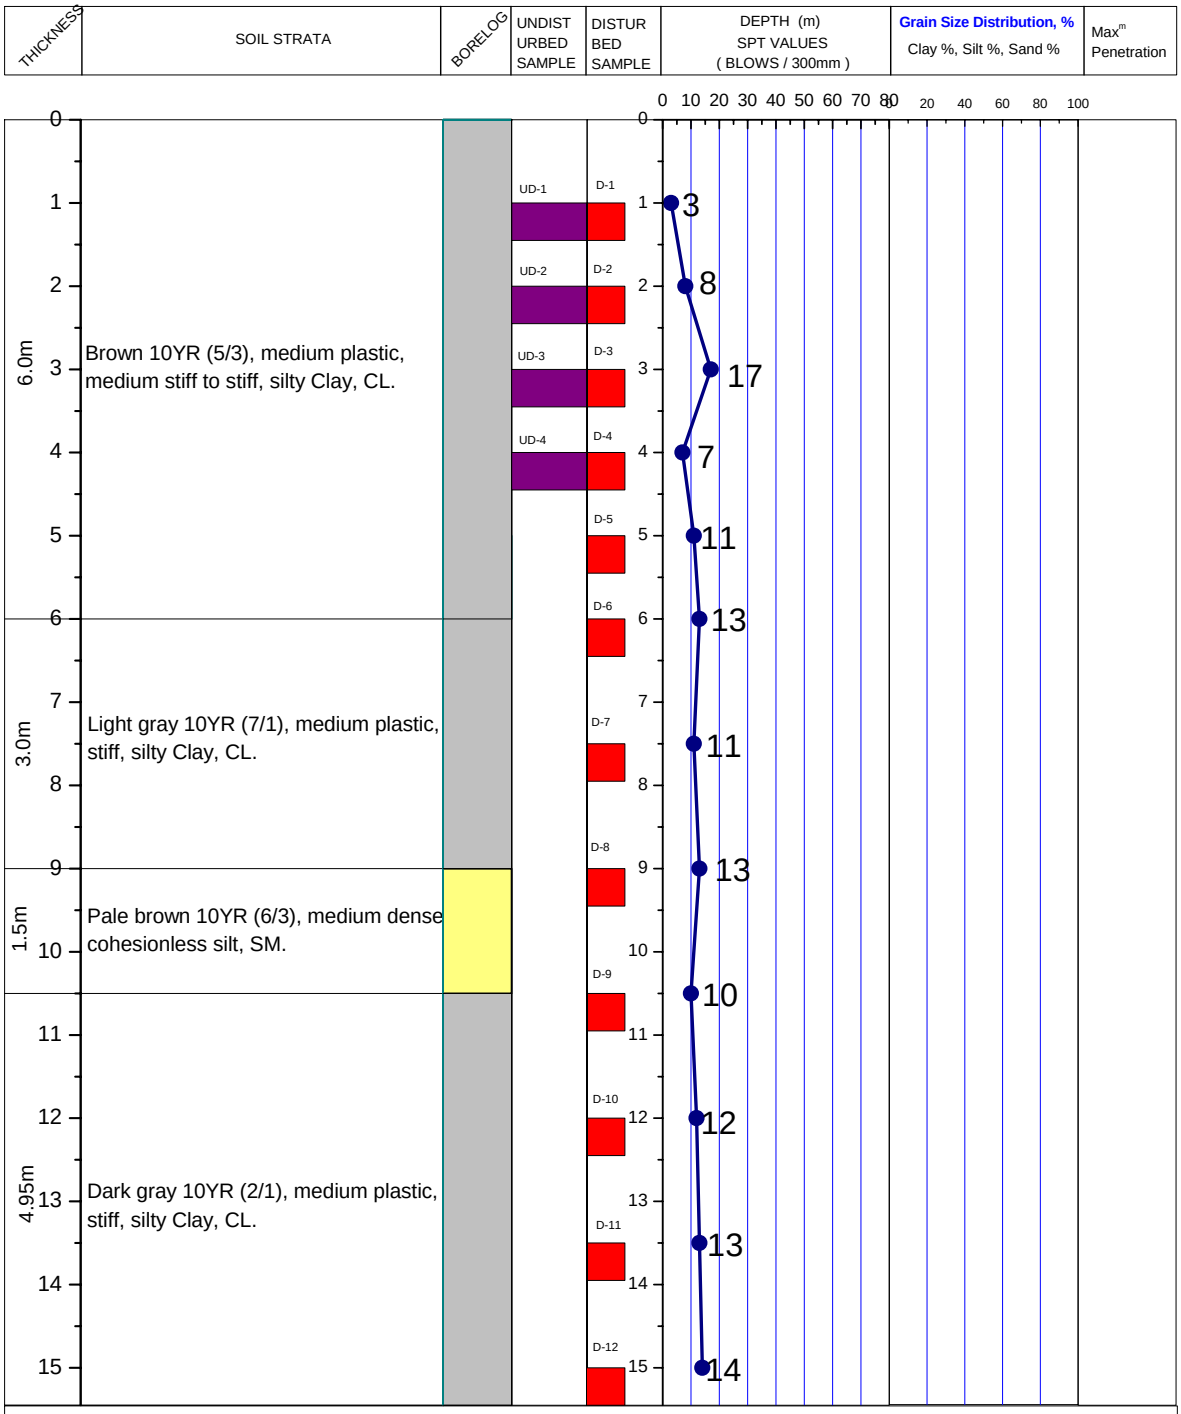

LEGEND FOR BORELOG AND GRAIN SIZE DISTRIBUTION

PLASTIC SILTY CLAY

LOW PLASTIC CLAYEY SILT

NON PLASTIC SILT

SAND

ORGANIC

UNDISTURBED SAMPLE

DISTURBED SAMPLE

SHALE

N- BLOWS DELIVERED PER FOOT BY A 140 LB HAMMER FALLING 30 INCHES

MAX^{m} PENETRATION= 50 BLOWS

AFTER 50 BLOWS PENETRATION DEPTH WERE MEASURED