A2 PROSOIL	BOREHOLE NO: BH-1	
	LOCATION : Bridge Over Dhanagoda River (Matlab Bridge) At Matlab, Chandpur.	
PROJECT : Proposed 305.25m Long P.C. Girder Bridge.	DEPTH OF BORING : 45.0m	GPS : 572719m Easting 582730m Northing R.L. : 2.34
CLIENT : Road Division, Chandpur.	DATE OF BORING : 24-12-2010.	G. W. T : On E.G.L.

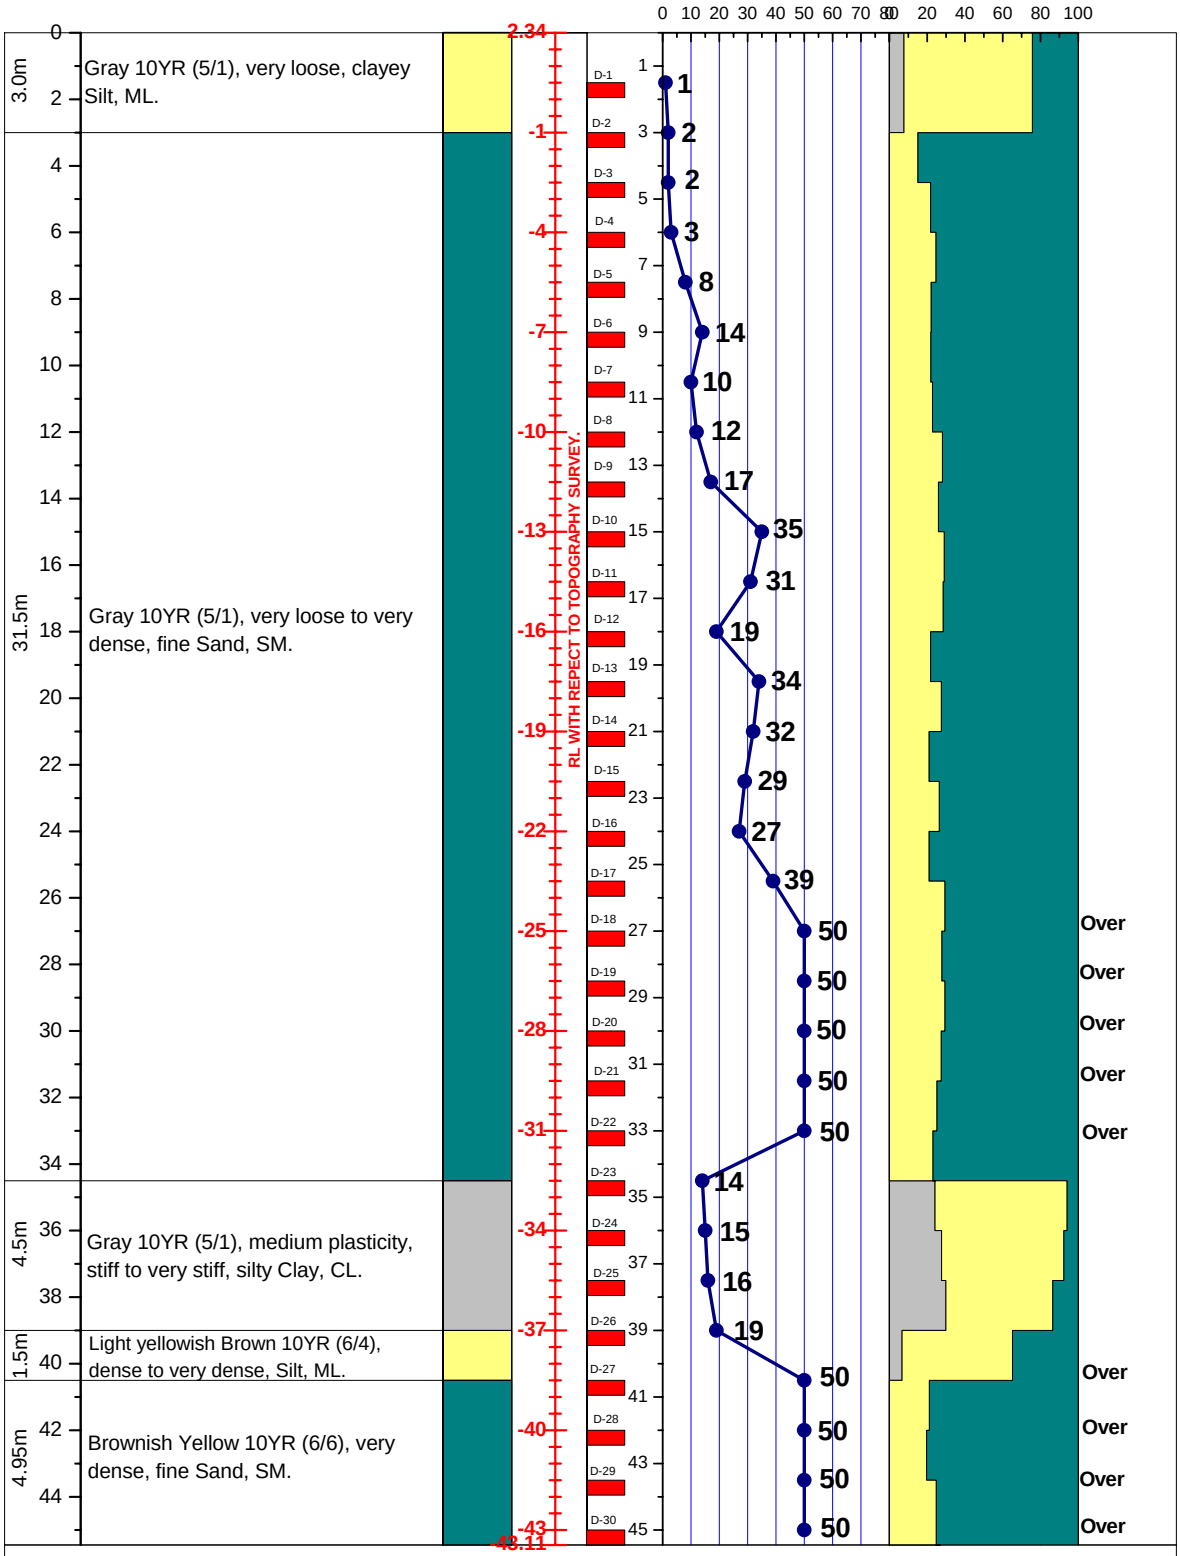

LEGEND FOR BORELOG AND GRAIN SIZE DISTRIBUTION (BASED ON 'ASTM CLASSIFICATION D-2487')

PLASTIC CLAY	SILT	PEAT/HIGHLY ORGANIC SOIL	UNDISTURBED SAMPLE
MICACEOUS FINE SAND/SILT	SAND	SHALE	DISTURBED SAMPLE

N- BLOWS DELIVERED PER FOOT BY A 140 LB HAMMER FALLING 30 INCHES

MAX^{m} PENETRATION= 50 BLOWS. AFTER 50 BLOWS PENETRATION DEPTH WERE MEASURED