A2	PROSOIL	BOREHOLE NO: BH-01 (ABUTMENT-01)	
		LOCATION : MAWNA, SREEPUR, GAZIPUR.	
PROJECT : JOYDEBPUR-MYMENSINGH ROAD IMPROVEMENT PROJECT (JMRIP), PACKAGE-4		DEPTH OF BORING : 15.0m	Chainage: 26+240 R. L. : 0.0
CLIENT : SPECIAL WORKS ORGANIZATION (SWO) CORPS OF ENGINEERS, BANGLADESH ARMY		DATE OF BORING : 11-04-2014.	B. W. T : 1.52m below from E.G.L.

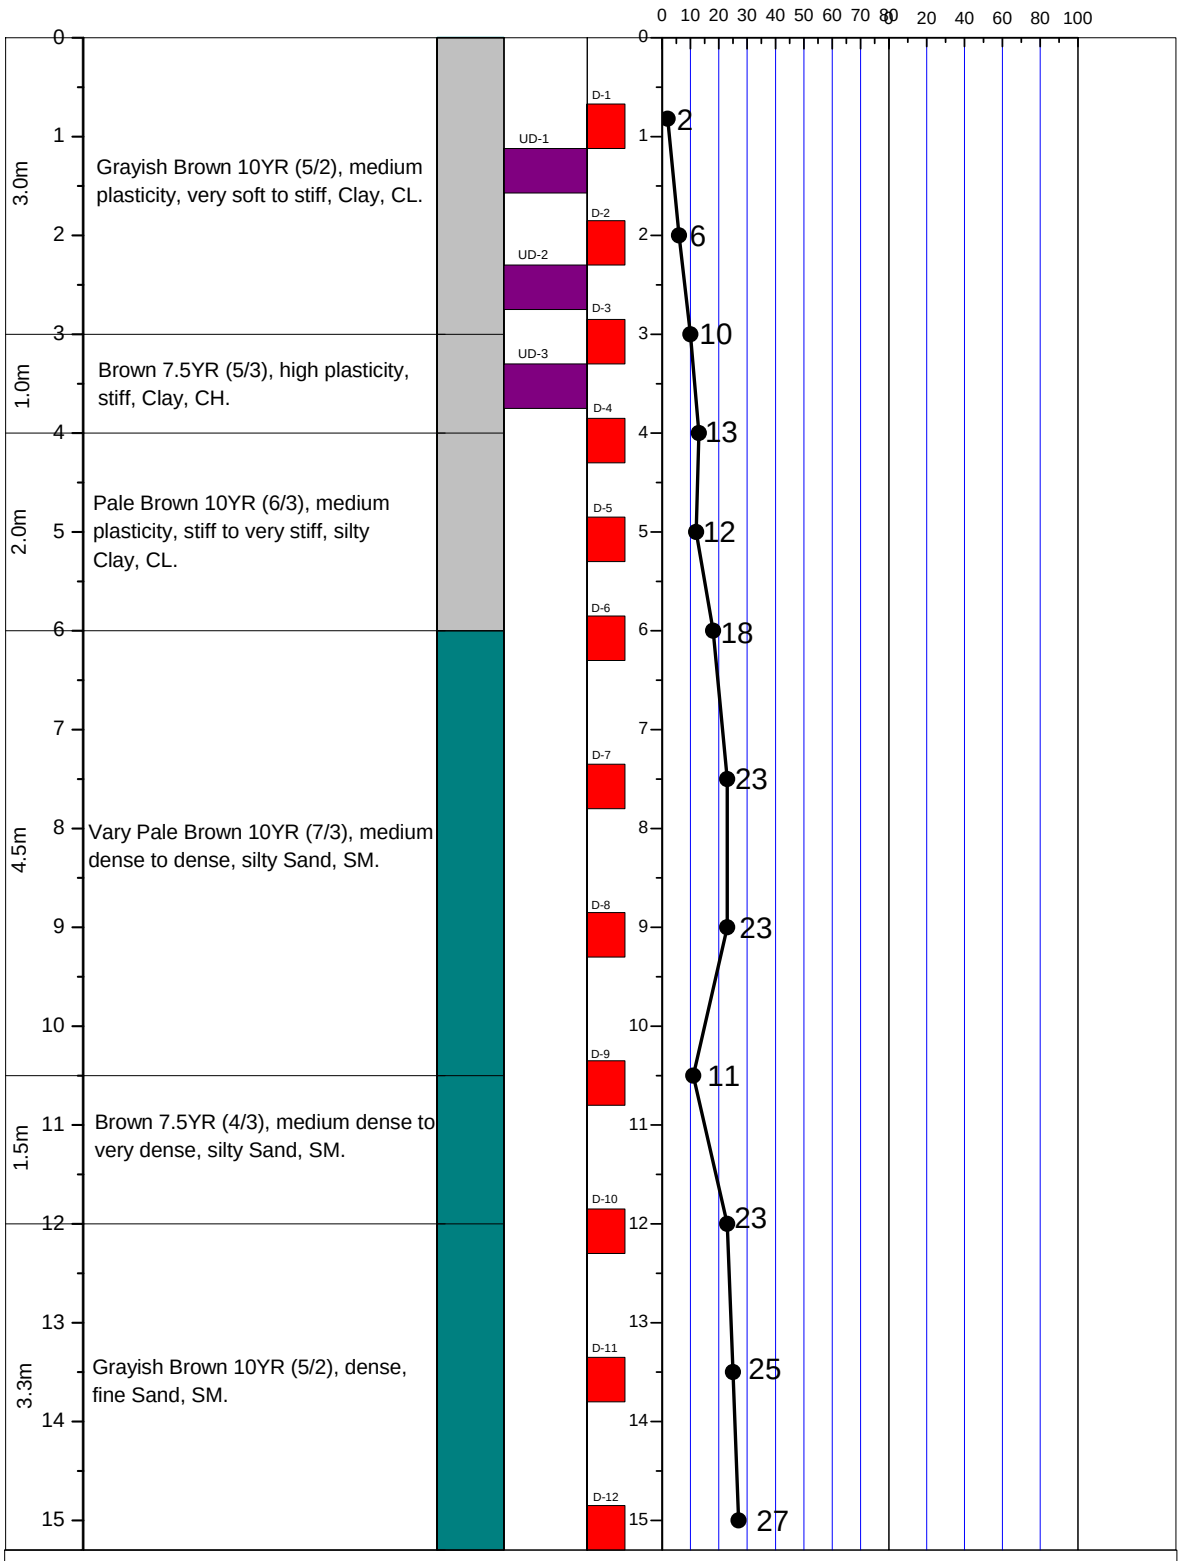

LEGEND FOR BORELOG AND GRAIN SIZE DISTRIBUTION (BASED ON 'ASTM CLASSIFICATION D-2487')

PLASTIC CLAY	SILT	PEAT/HIGHLY ORGANIC SOIL	UNDISTURBED SAMPLE
MICACEOUS FINE SAND/SILT	SAND	SHALE	DISTURBED SAMPLE

N- BLOWS DELIVERED PER FOOT BY A 140 LB HAMMER FALLING 30 INCHES

MAX^{m} PENETRATION= 50 BLOWS. AFTER 50 BLOWS PENETRATION DEPTH WERE MEASURED