A2	PROSOIL	BOREHOLE NO: BH-1	
		LOCATION: BAITUL AMAN BAZAR, FARIDPUR SADAR, FARIDPUR.	
PROJECT : Telecommunication Tower.		DEPTH OF BORING: 21.0m	R. L.: 2.5m below from Road Level.
CLIENT : Orascom Telecom Bangladesh Limited.		DATE OF BORING : 08-11-2015.	G. W. T : 0.30m below from E. G. L.

THICKNESS	SOIL STRATA	BORELOG	UNDISTURBED SAMPLE	DISTURBED SAMPLE	DEPTH (m) SPT VALUES (BLOWS / 300mm)	Grain Size Distribution, % Clay %, Silt %, Sand %	Max^{m} Penetration

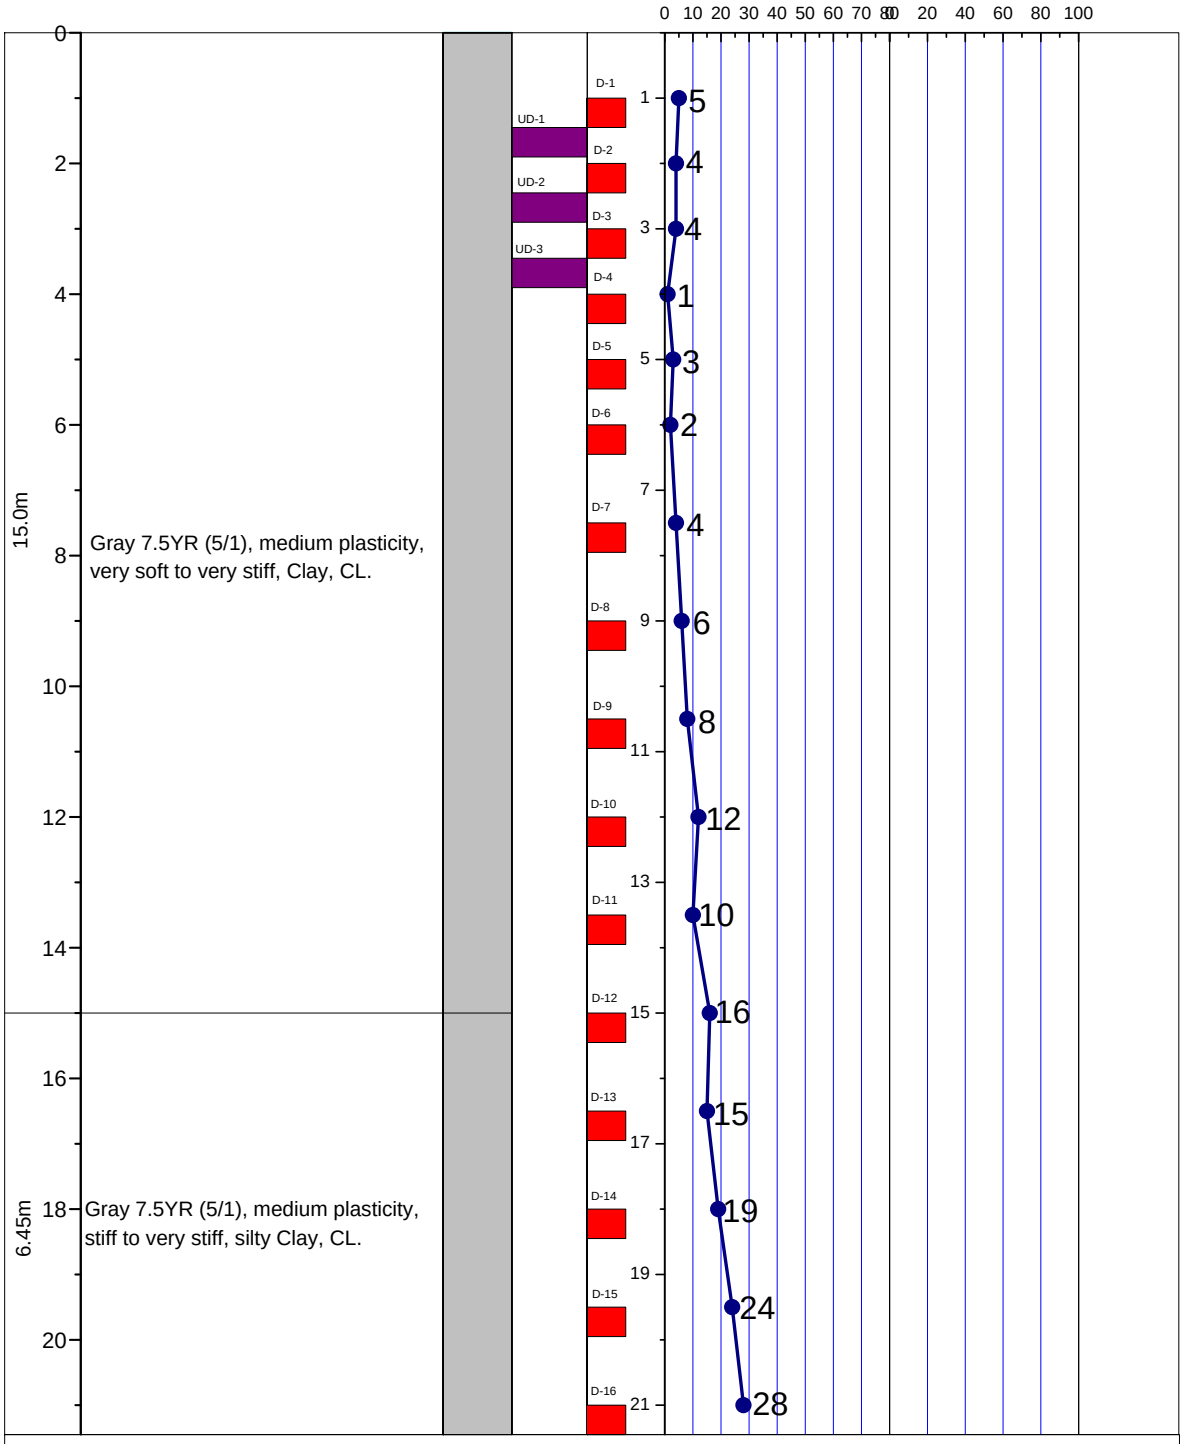

LEGEND FOR BORELOG AND GRAIN SIZE DISTRIBUTION (BASED ON 'ASTM CLASSIFICATION D-2487')

- PLASTIC CLAY
- SAND
- SILT
- SHALE
- PEAT/HIGHLY ORGANIC SOIL
- MICACEOUS FINE SAND/SILT
- UNDISTURBED SAMPLE
- DISTURBED SAMPLE

N- BLOWS DELIVERED PER FOOT BY A 140 LB HAMMER FALLING 30 INCHES

MAX^{m} PENETRATION= 50 BLOWS
AFTER 50 BLOWS PENETRATION DEPTH WERE MEASURED