A2 PROSOIL	BOREHOLE NO: BH-1	
	LOCATION : Mofoz Bagh Housing, Road No. 7, Plot 151/9/A, Sheikh er Tech.	
PROJECT : Proposed Six (6) Storied Building.	DEPTH OF BORING : 21.0m	R. L.: Road Level.
CLIENT : Mr. SM Younus.	DATE OF BORING : 26-08-2009	G. W. T : 1.52m below from E. G. L.

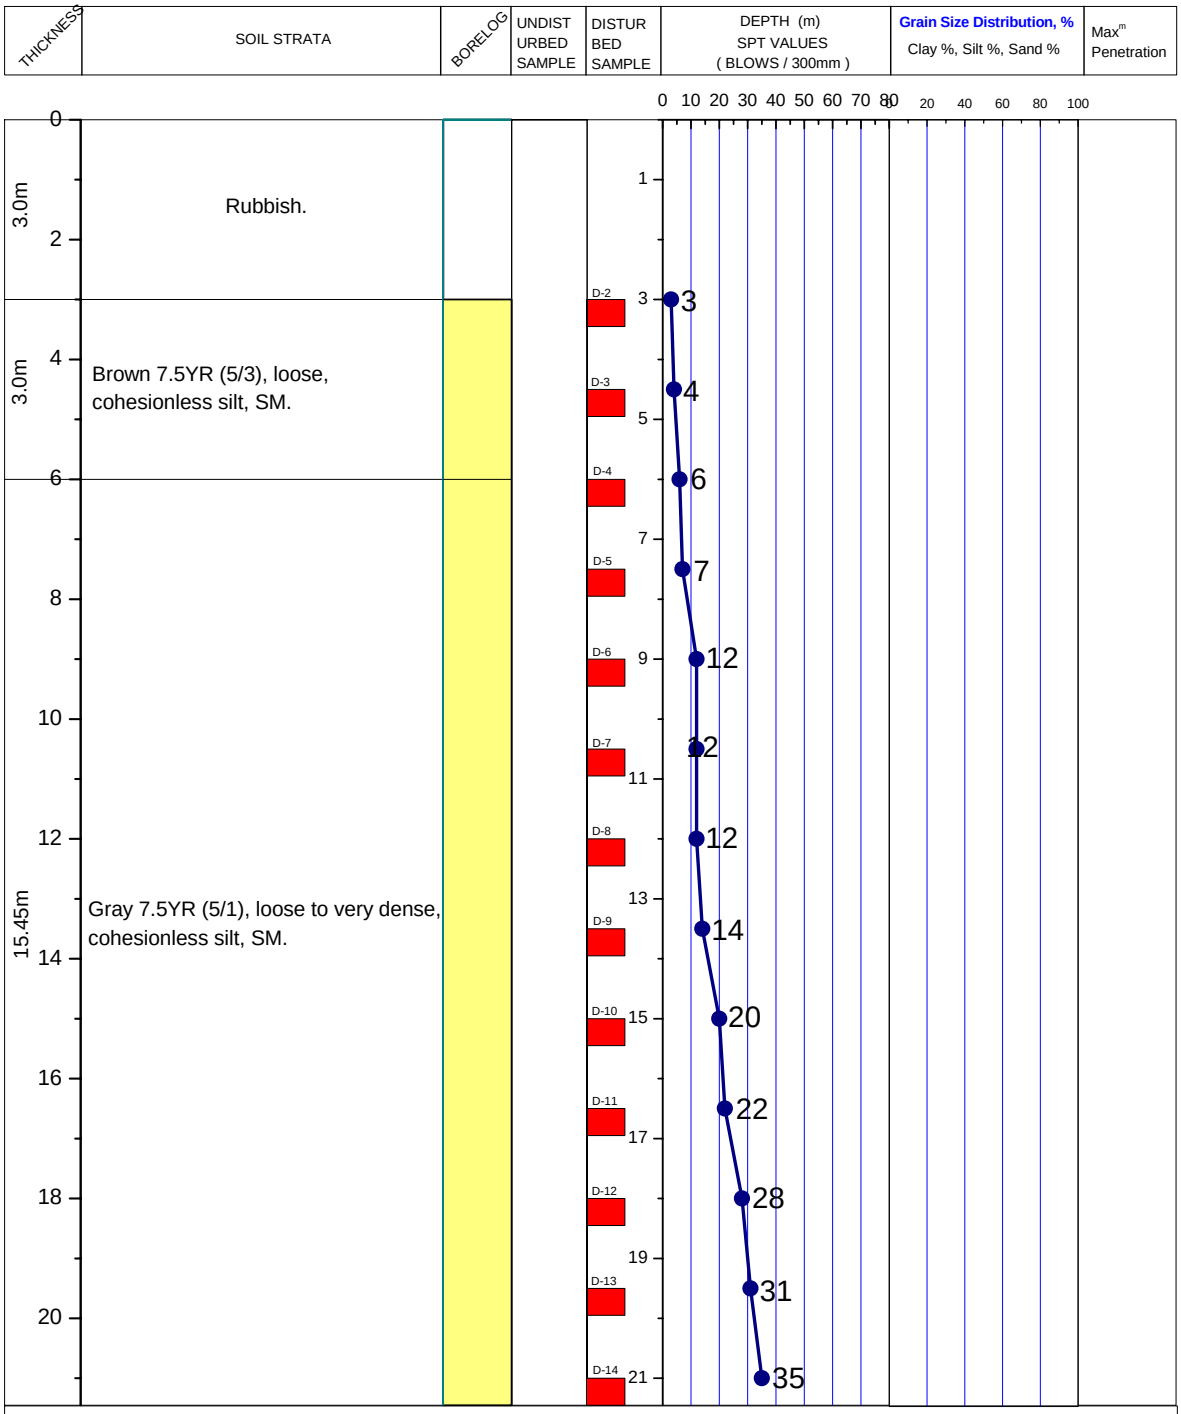

LEGEND FOR BORELOG AND GRAIN SIZE DISTRIBUTION

PLASTIC SILTY CLAY	NON PLASTIC SILT	ORGANIC	UNDISTURBED SAMPLE
LOW PLASTIC CLAYEY SILT	SAND	SHALE	DISTURBED SAMPLE

N- BLOWS DELIVERED PER FOOT BY A 140 LB HAMMER FALLING 30 INCHES

MAX^{m} PENETRATION= 50 BLOWS

AFTER 50 BLOWS PENETRATION DEPTH WERE MEASURED