A2	PROSOIL	BOREHOLE NO: BH-1	
		LOCATION : Charsindur Bridge Over Sitalakhya River Connecting Gazipur -Azmatpur -Etakhola Road, Narsingdi.	
PROJECT : Proposed Charsindur Bridge.		DEPTH OF BORING : 48.0m	Chainage: 0.00 R. L. : 7.89
CLIENT : Road Division, Narsingdi.		DATE OF BORING : 22-01-2013.	G. W. T : 2.74m below from E.G.L.

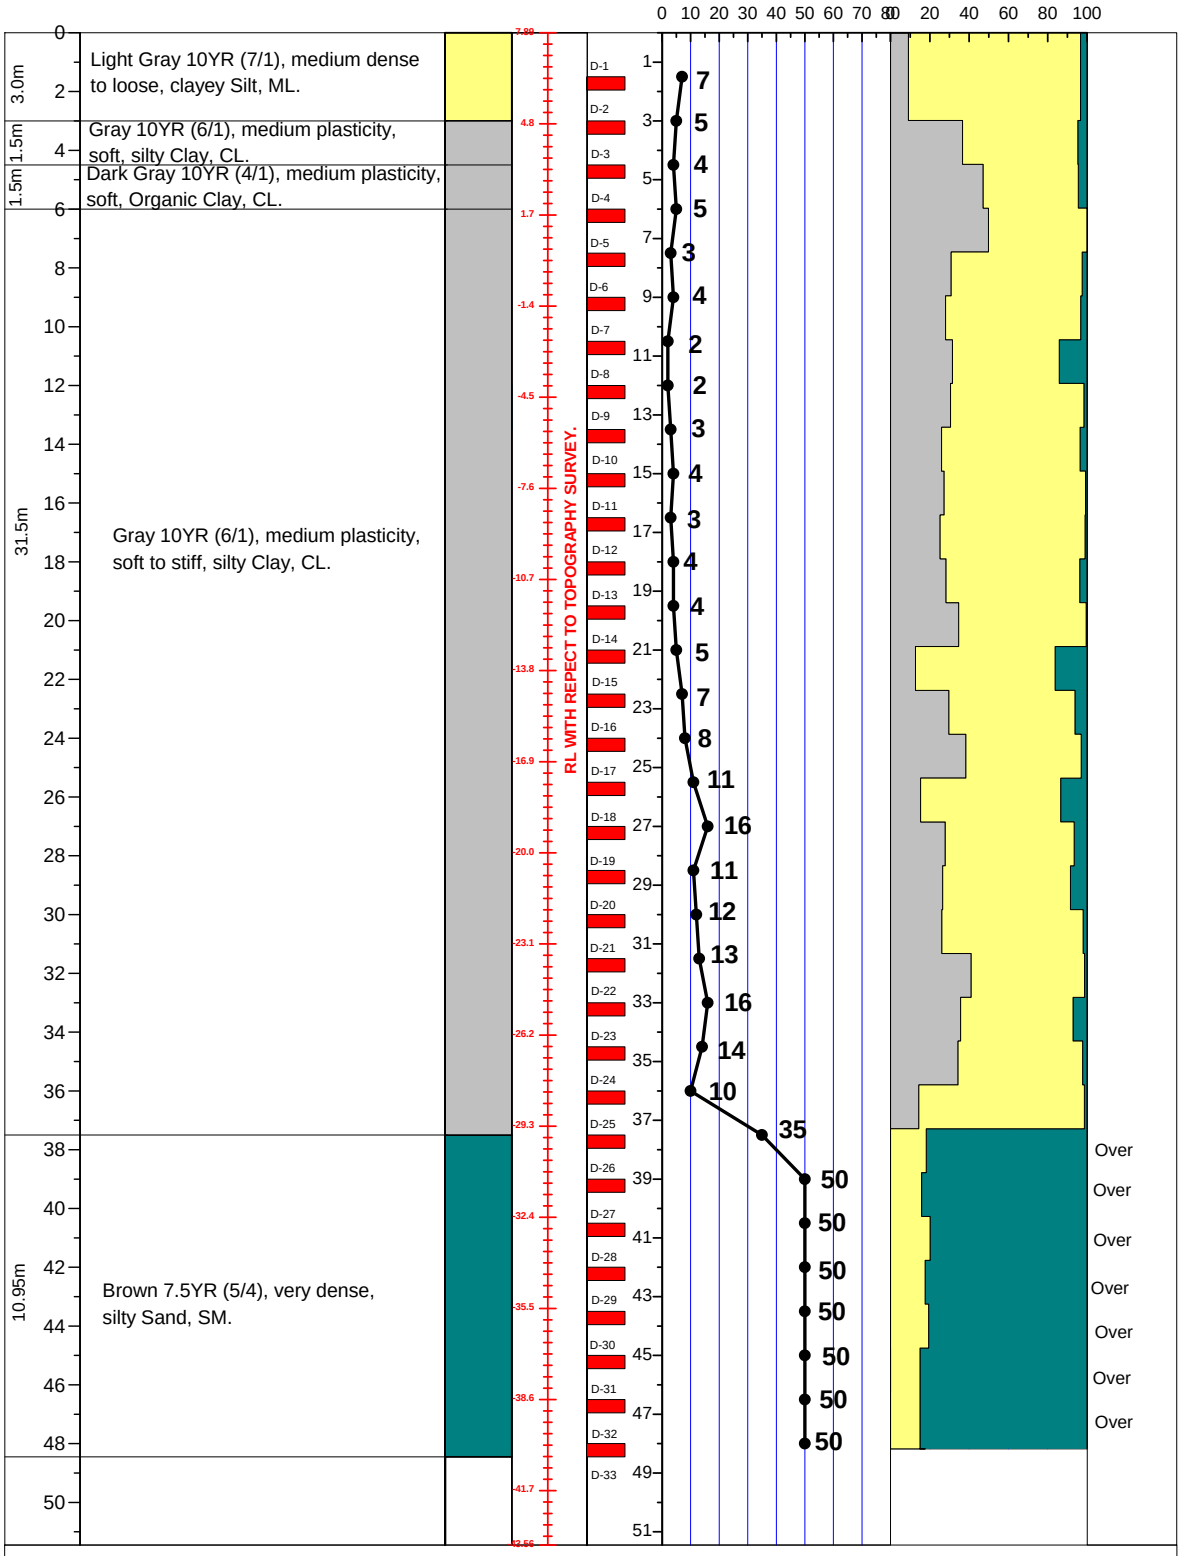

LEGEND FOR BORELOG AND GRAIN SIZE DISTRIBUTION (BASED ON 'ASTM CLASSIFICATION D-2487')

PLASTIC CLAY	SILT	PEAT/HIGHLY ORGANIC SOIL	UNDISTURBED SAMPLE
MICACEOUS FINE SAND/SILT	SAND	SHALE	DISTURBED SAMPLE

N- BLOWS DELIVERED PER FOOT BY A 140 LB HAMMER FALLING 30 INCHES

MAX^{m} PENETRATION= 50 BLOWS. AFTER 50 BLOWS PENETRATION DEPTH WERE MEASURED