A2 PROSOIL	BOREHOLE NO: BH-1	
	LOCATION : Plot# L34, Road# S-2, Thana: Pollobi, Mauza: Chatgoranbari, Pollobi-2, Mirpur, Dhaka.	
PROJECT : Proposed Six Storied Building.	DEPTH OF BORING : 21.0m	R. L.: 0.91m below from Road Level.
CLIENT : Md. Rafiqul Islam et al.	DATE OF BORING : 27-07-2008.	G. W. T : 3.04m below from E. G. L.

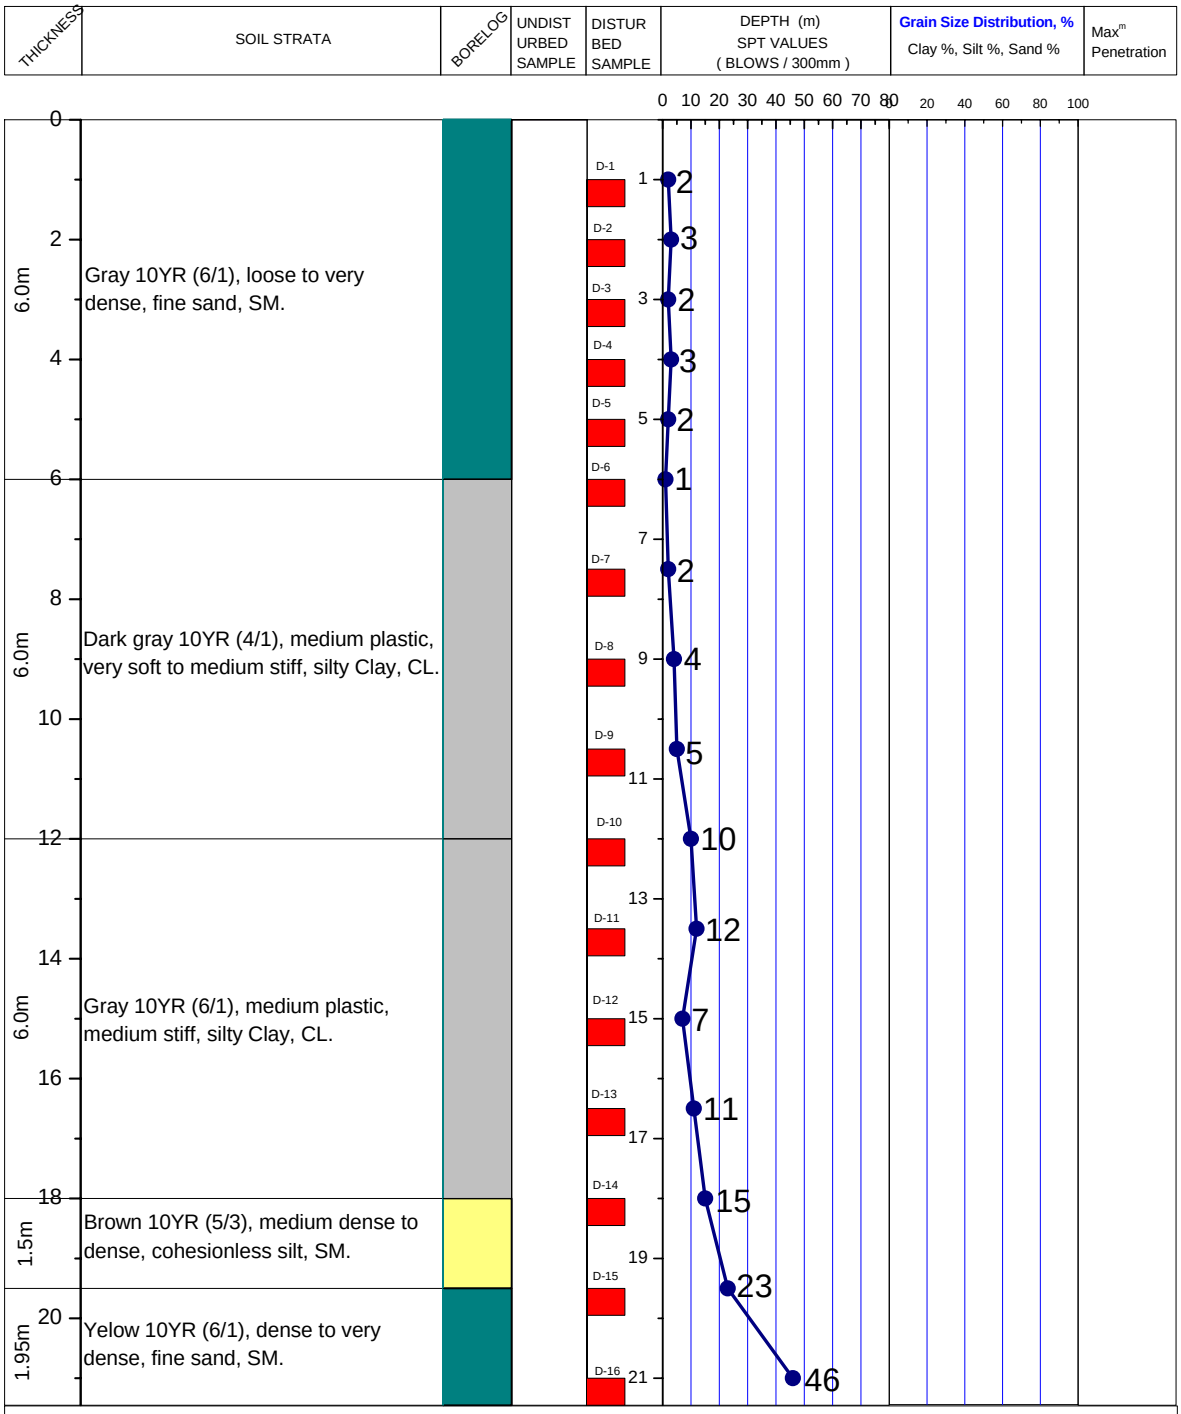

LEGEND FOR BORELOG AND GRAIN SIZE DISTRIBUTION

PLASTIC SILTY CLAY | LOW PLASTIC CLAYEY SILT | NON PLASTIC SILT | SAND

ORGANIC | UNDISTURBED SAMPLE | DISTURBED SAMPLE | SHALE

N- BLOWS DELIVERED PER FOOT BY A 140 LB HAMMER FALLING 30 INCHES

MAX^{m} PENETRATION= 50 BLOWS

AFTER 50 BLOWS PENETRATION DEPTH WERE MEASURED