A2 PROSOIL	BOREHOLE NO: BH-1	
	LOCATION : Kuruskul, Uttar Hindupara, Cox's Bazar.	
PROJECT : Telecommunication Tower.	DEPTH OF BORING : 9.0m	R. L.: 0.70m below from Road Level.
CLIENT : Warid Telecom International Ltd.	DATE OF BORING: 15-02-2011.	G. W. T : 2.95m below from E.G.L.

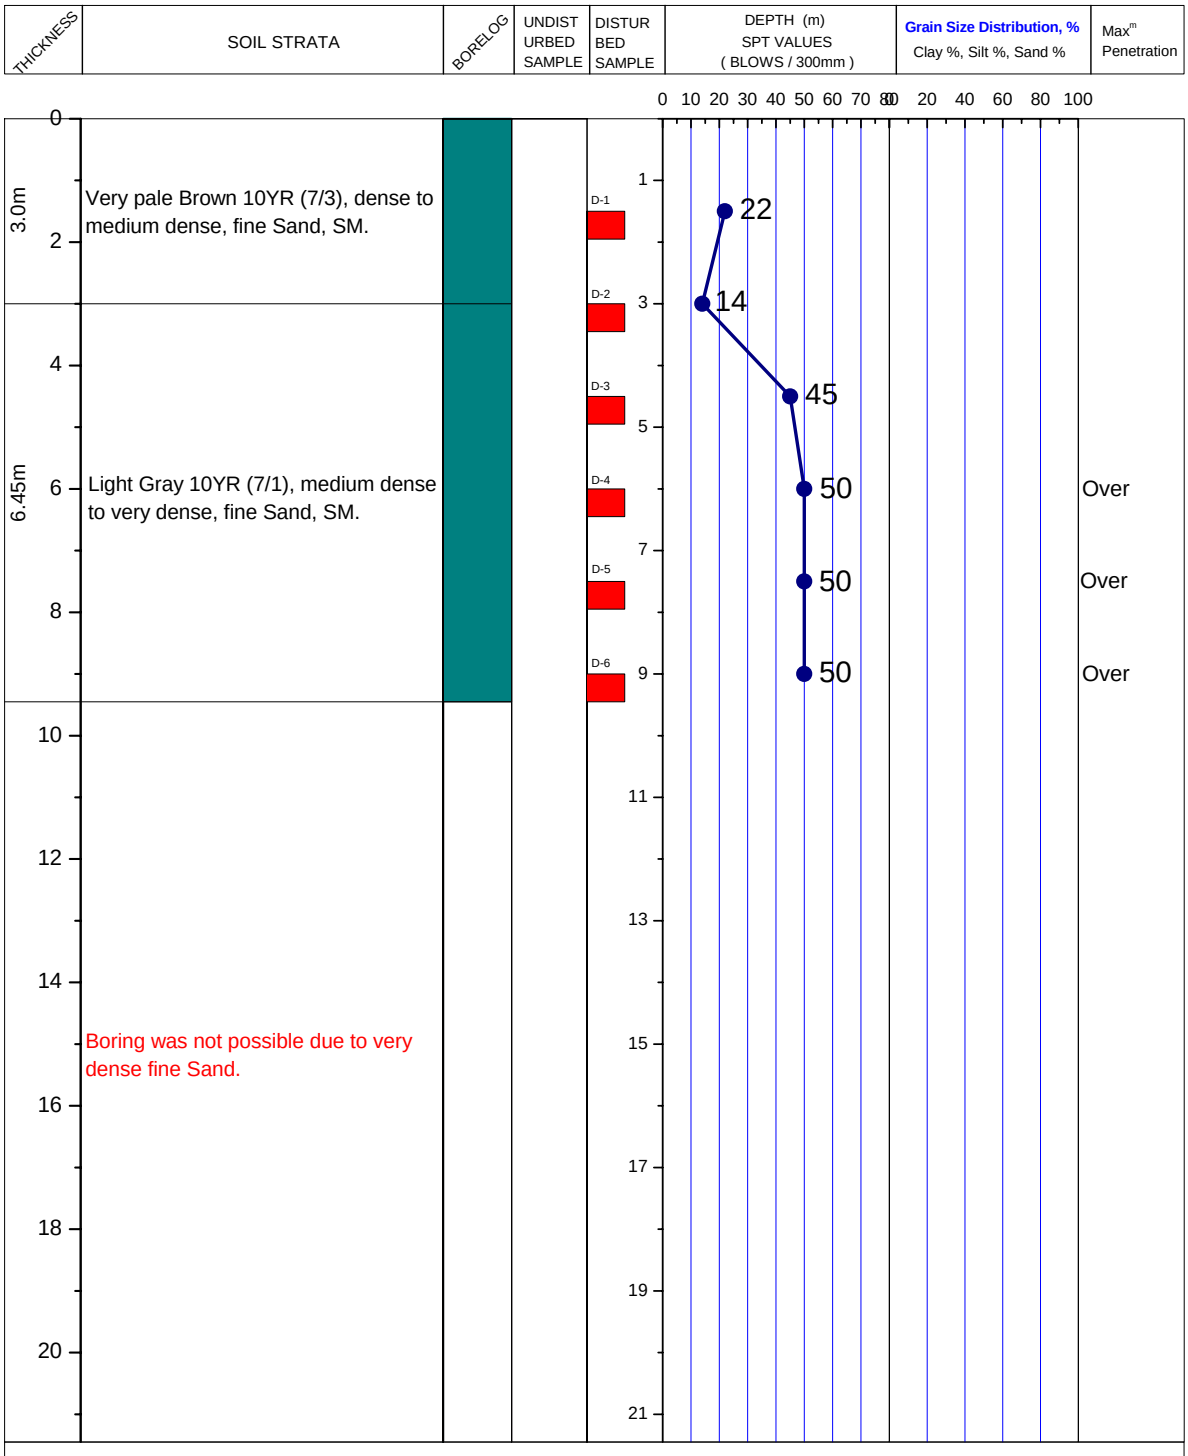

LEGEND FOR BORELOG AND GRAIN SIZE DISTRIBUTION (BASED ON 'ASTM CLASSIFICATION D-2487')

PLASTIC CLAY	SAND	SHALE	UNDISTURBED SAMPLE
MICACEOUS FINE SAND/SILT	SILT	PEAT/HIGHLY ORGANIC SOIL	DISTURBED SAMPLE

N- BLOWS DELIVERED PER FOOT BY A 140 LB HAMMER FALLING 30 INCHES

MAX^{m} PENETRATION= 50 BLOWS

AFTER 50 BLOWS PENETRATION DEPTH WERE MEASURED