A2 PROSOIL	BOREHOLE NO: BH-1	
	LOCATION: Krittonkhola, Kochua, Shokhipur, Tangail.	
PROJECT : Telecommunication Tower.	DEPTH OF BORING: 18.0m	R. L.: 1.37m below from Road Level.
CLIENT : Grameenphone Ltd.	DATE OF BORING: 16-08-2011.	G. W. T : On E. G. L.

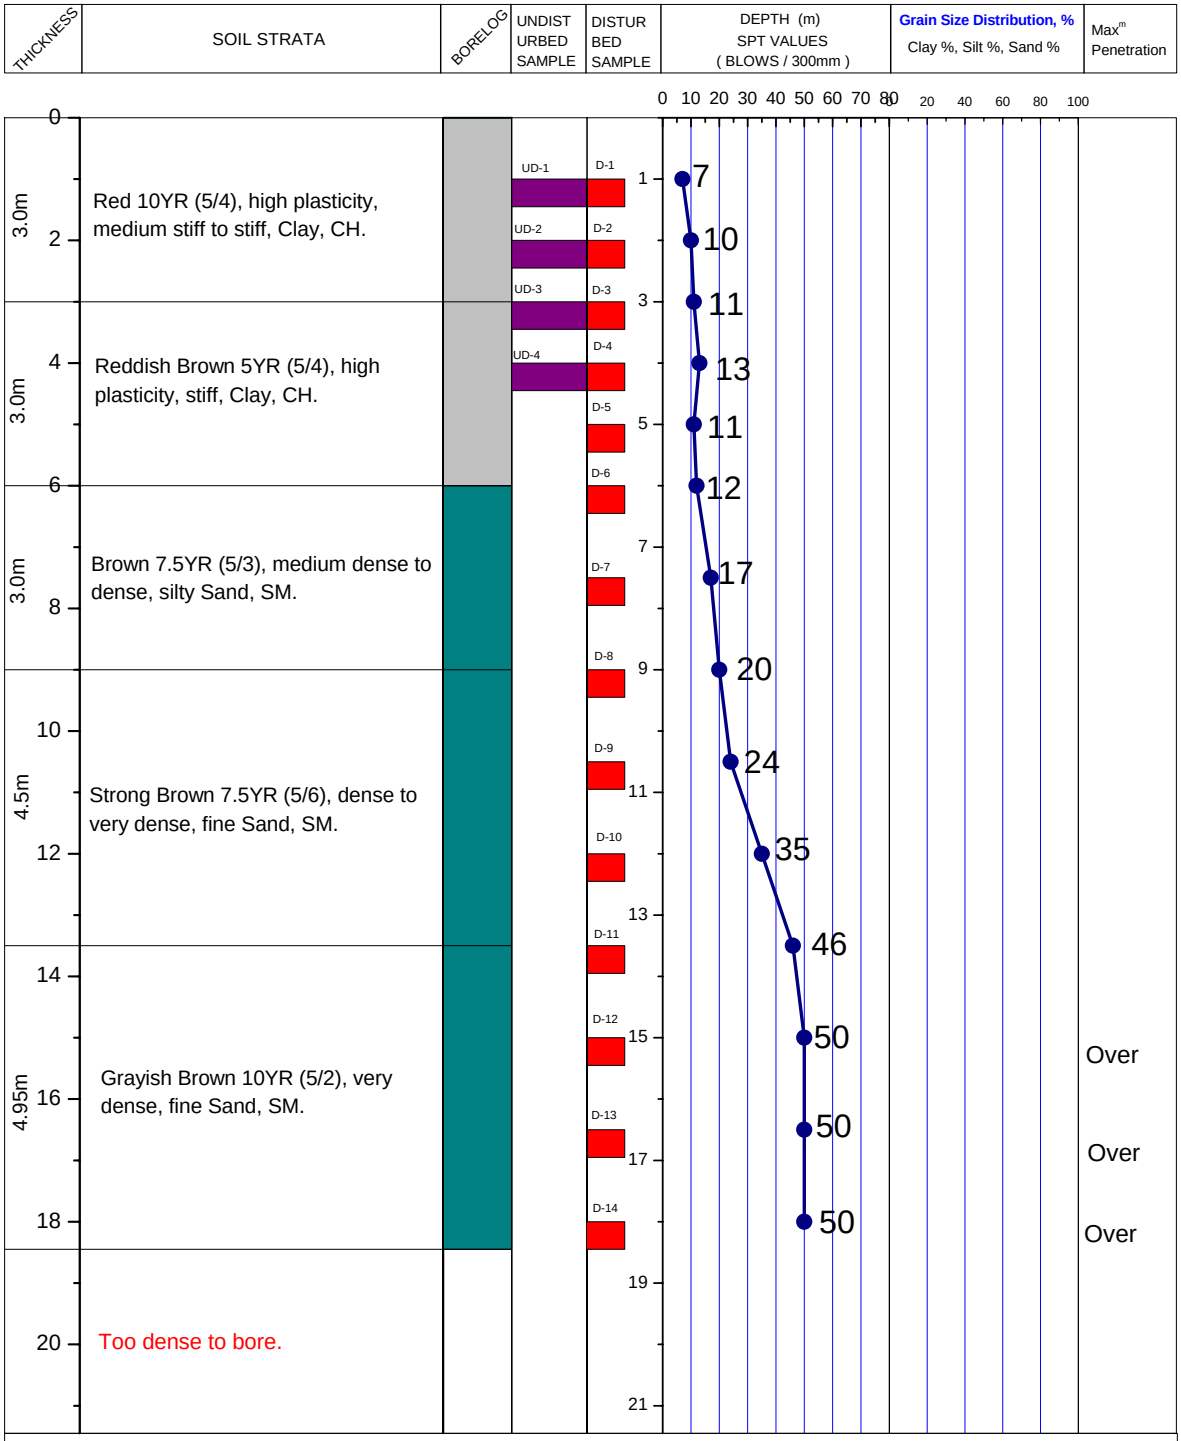

LEGEND FOR BORELOG AND GRAIN SIZE DISTRIBUTION (BASED ON 'ASTM CLASSIFICATION D-2487')

PLASTIC CLAY | SHALE | SILT | SAND

PEAT/HIGHLY ORGANIC SOIL | MICACEOUS FINE SAND/SILT | UNDISTURBED SAMPLE | DISTURBED SAMPLE

N- BLOWS DELIVERED PER FOOT BY A 140 LB HAMMER FALLING 30 INCHES

MAX^{m} PENETRATION= 50 BLOWS

AFTER 50 BLOWS PENETRATION DEPTH WERE MEASURED