A2	PROSOIL	BOREHOLE NO: BH-1	
		LOCATION : Chandi Pur, Dowarabazar, Sunamganj. (25°01'57.0244"N, 91°31'42.4964"E).	
PROJECT : Chandi Pur GPS, (Multi-purpose Cyclone Shelter/Govt. Primary School)		DEPTH OF BORING : 21.0m	R. L.: On Road Level.
CLIENT : US Army Corps of Engr, Alaska District. THROUGH : AUSPICIOUS, QA Contractor.		DATE OF BORING : 22-04-2013.	G. W. T : 4.27m below from E.G.L.

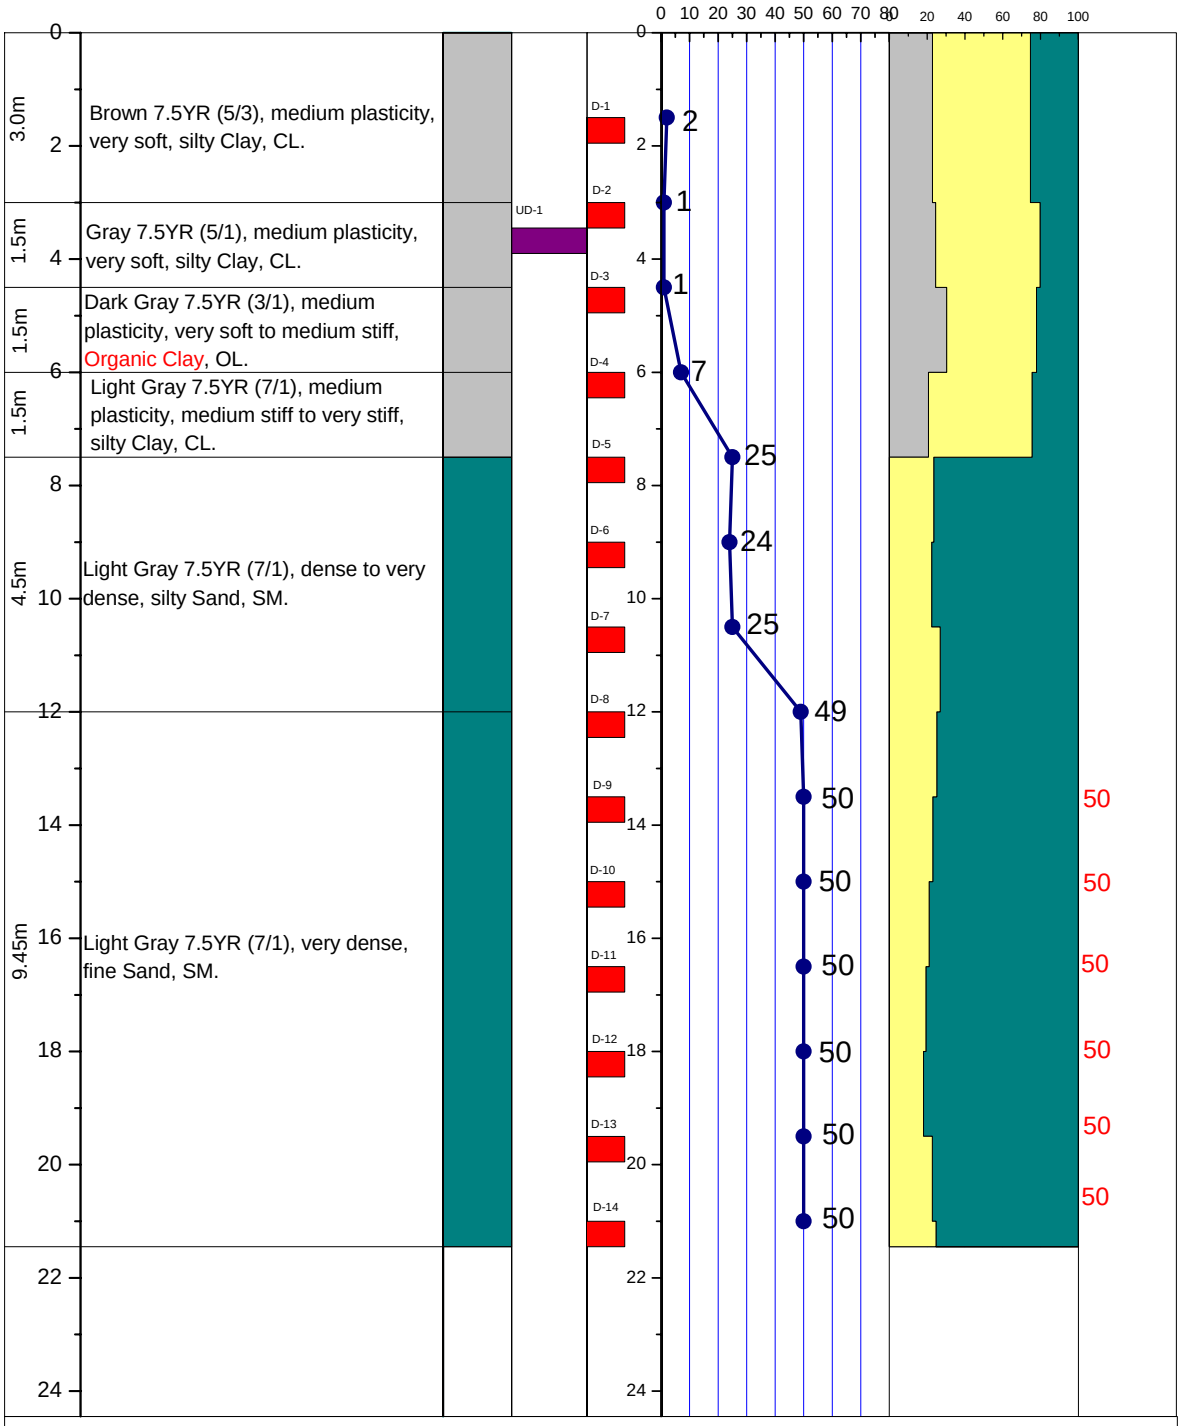

LEGEND FOR BORELOG AND GRAIN SIZE DISTRIBUTION (BASED ON 'ASTM CLASSIFICATION D-2487')

PLASTIC CLAY	SILT	SHALE	UNDISTURBED SAMPLE
MICACEOUS FINE SAND/SILT	SAND	PEAT/HIGHLY ORGANIC SOIL	DISTURBED SAMPLE

N- BLOWS DELIVERED PER FOOT BY A 140 LB HAMMER FALLING 30 INCHES

MAX^{m} PENETRATION= 50 BLOWS
AFTER 50 BLOWS PENETRATION DEPTH WERE MEASURED