| A2 PROSOIL | BOREHOLE NO: BH-2 | |
|---|---|---|
| | LOCATION : Shibrampur, Faridpur. | |
| PROJECT : Telecommunication Tower. | DEPTH OF BORING : 21.0m | R. L.: 0.30m below from Road Level. |
| CLIENT : Sheba Telecom (PVT.) Ltd. | DATE OF BORING : 03-11-2007. | G. W. T : 1.82m below from E. G. L. |

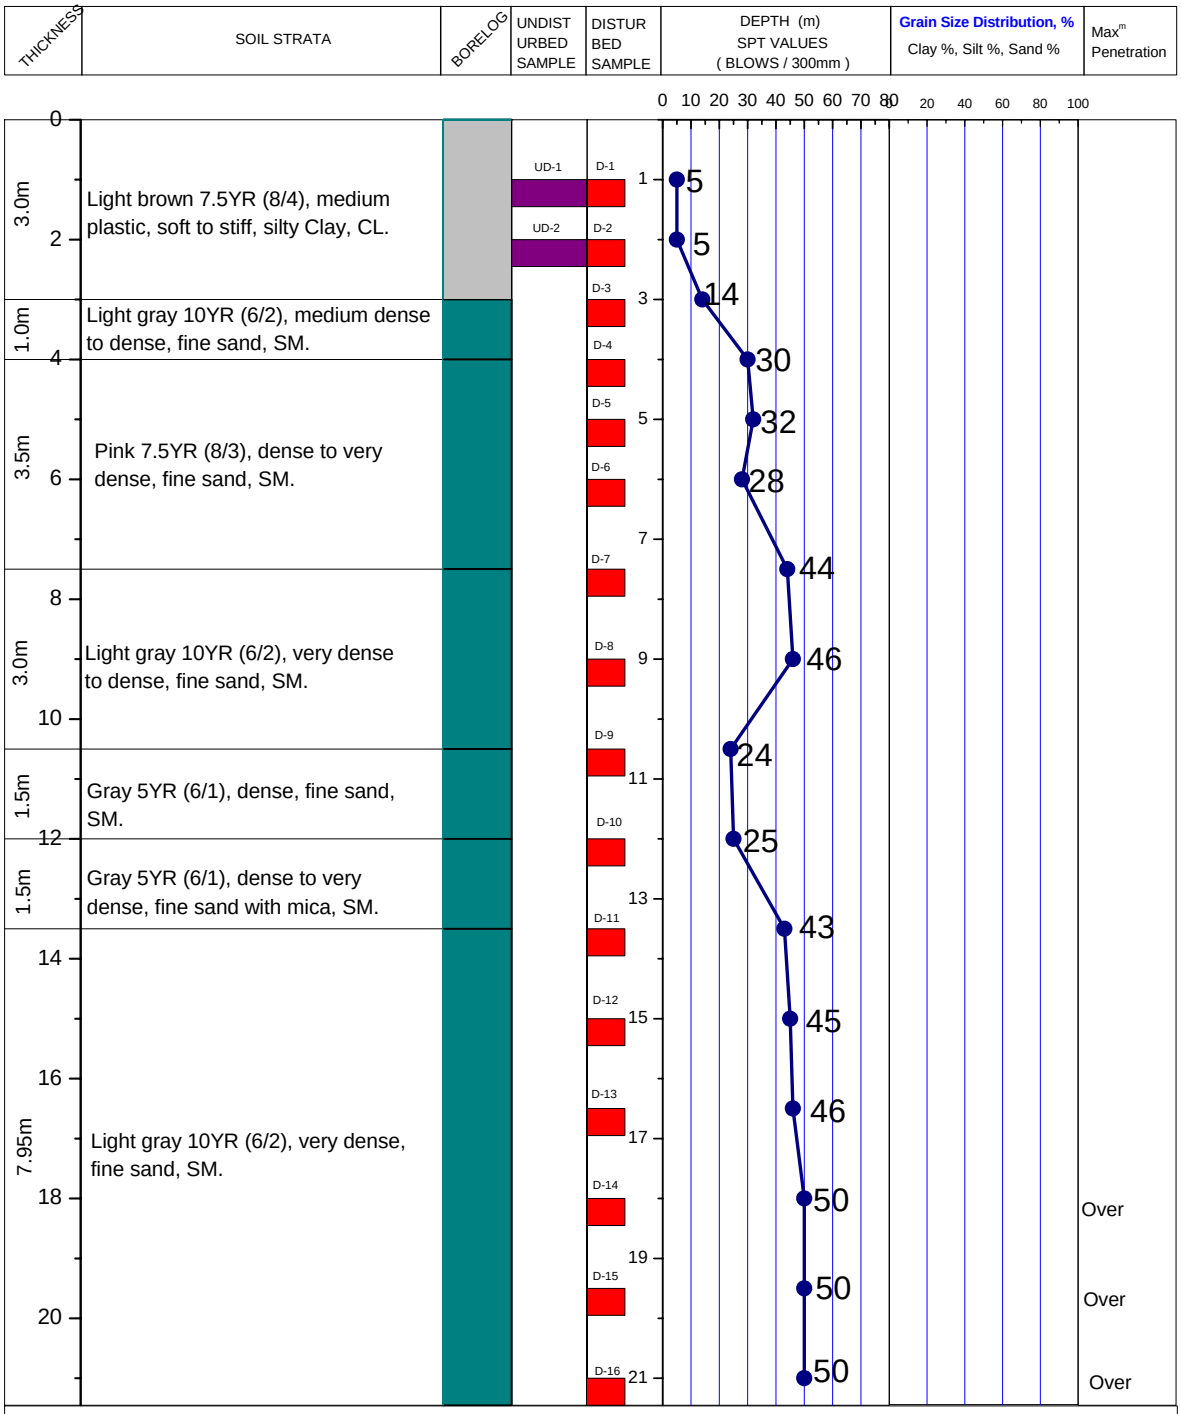


LEGEND FOR BORELOG AND GRAIN SIZE DISTRIBUTION

PLASTIC SILTY CLAY

LOW PLASTIC CLAYEY SILT

NON PLASTIC SILT

SAND

ORGANIC

UNDISTURBED SAMPLE

DISTURBED SAMPLE

SHALE

N- BLOWS DELIVERED PER FOOT BY A 140 LB HAMMER FALLING 30 INCHES

MAX$^{m}$ PENETRATION= 50 BLOWS

AFTER 50 BLOWS PENETRATION DEPTH WERE MEASURED