| A2 | PROSOIL | BOREHOLE NO: BH-1 | |
|---|---|---|---|
| | | LOCATION : Mohishcharoni, Morrlgonj, Bagerhat. | |
| PROJECT : MULTI PURPOSE CYCLONE SHELTER. | | DEPTH OF BORING : 21.0m | R. L.: 0.91m below from Road Level. |
| CLIENT : US Army Corps of Engineers, Pacific Ocean Division. | | DATE OF BORING : 06-01-2009. | G. W. T : 0.30m below from E. G. L. |

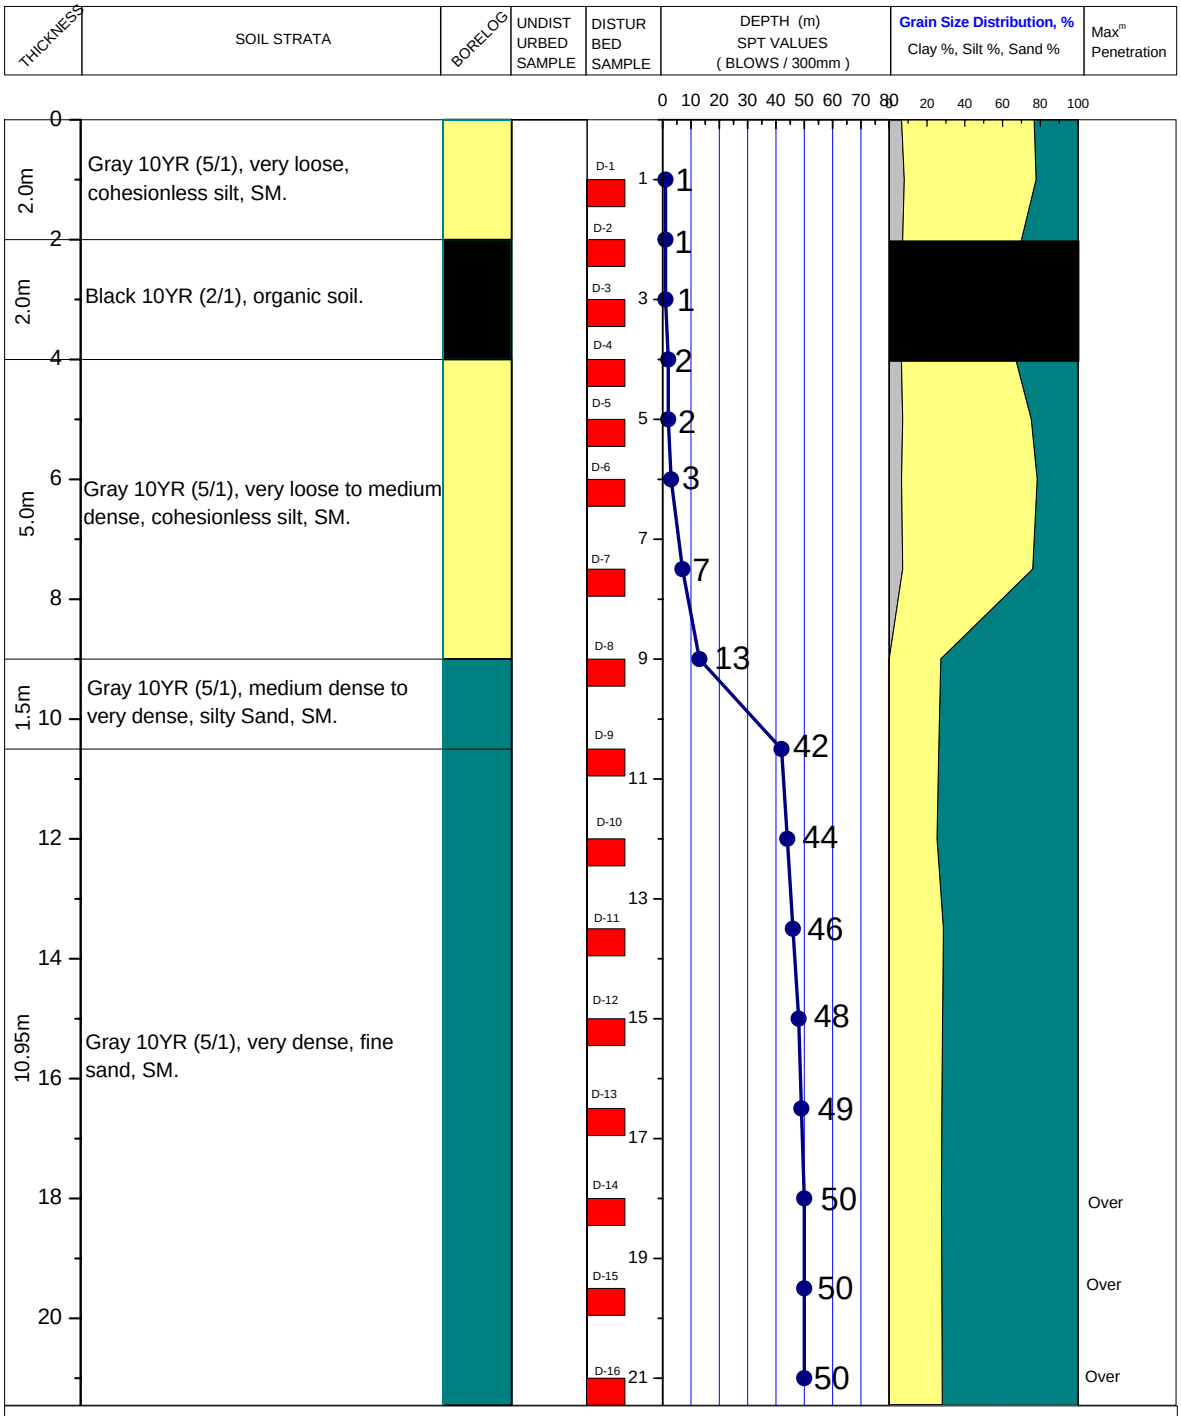


LEGEND FOR BORELOG AND GRAIN SIZE DISTRIBUTION

PLASTIC SILTY CLAY

LOW PLASTIC CLAYEY SILT

NON PLASTIC SILT

SAND

ORGANIC

UNDISTURBED SAMPLE

DISTURBED SAMPLE

SHALE

N- BLOWS DELIVERED PER FOOT BY A 140 LB HAMMER FALLING 30 INCHES

MAX$^{m}$ PENETRATION= 50 BLOWS

AFTER 50 BLOWS PENETRATION DEPTH WERE MEASURED