A2	PROSOIL	BOREHOLE NO: BH-1	
		LOCATION : Hartha 32m Land, Ujirpur, Barisal.	
PROJECT : Telecommunication Tower.		DEPTH OF BORING : 12.0m	R. L.: 2.40m below from Road Level.
CLIENT : AXIATA (Bangladesh) Ltd.		DATE OF BORING : 13-10-2009.	G. W. T : 0.60m below from E. G. L.

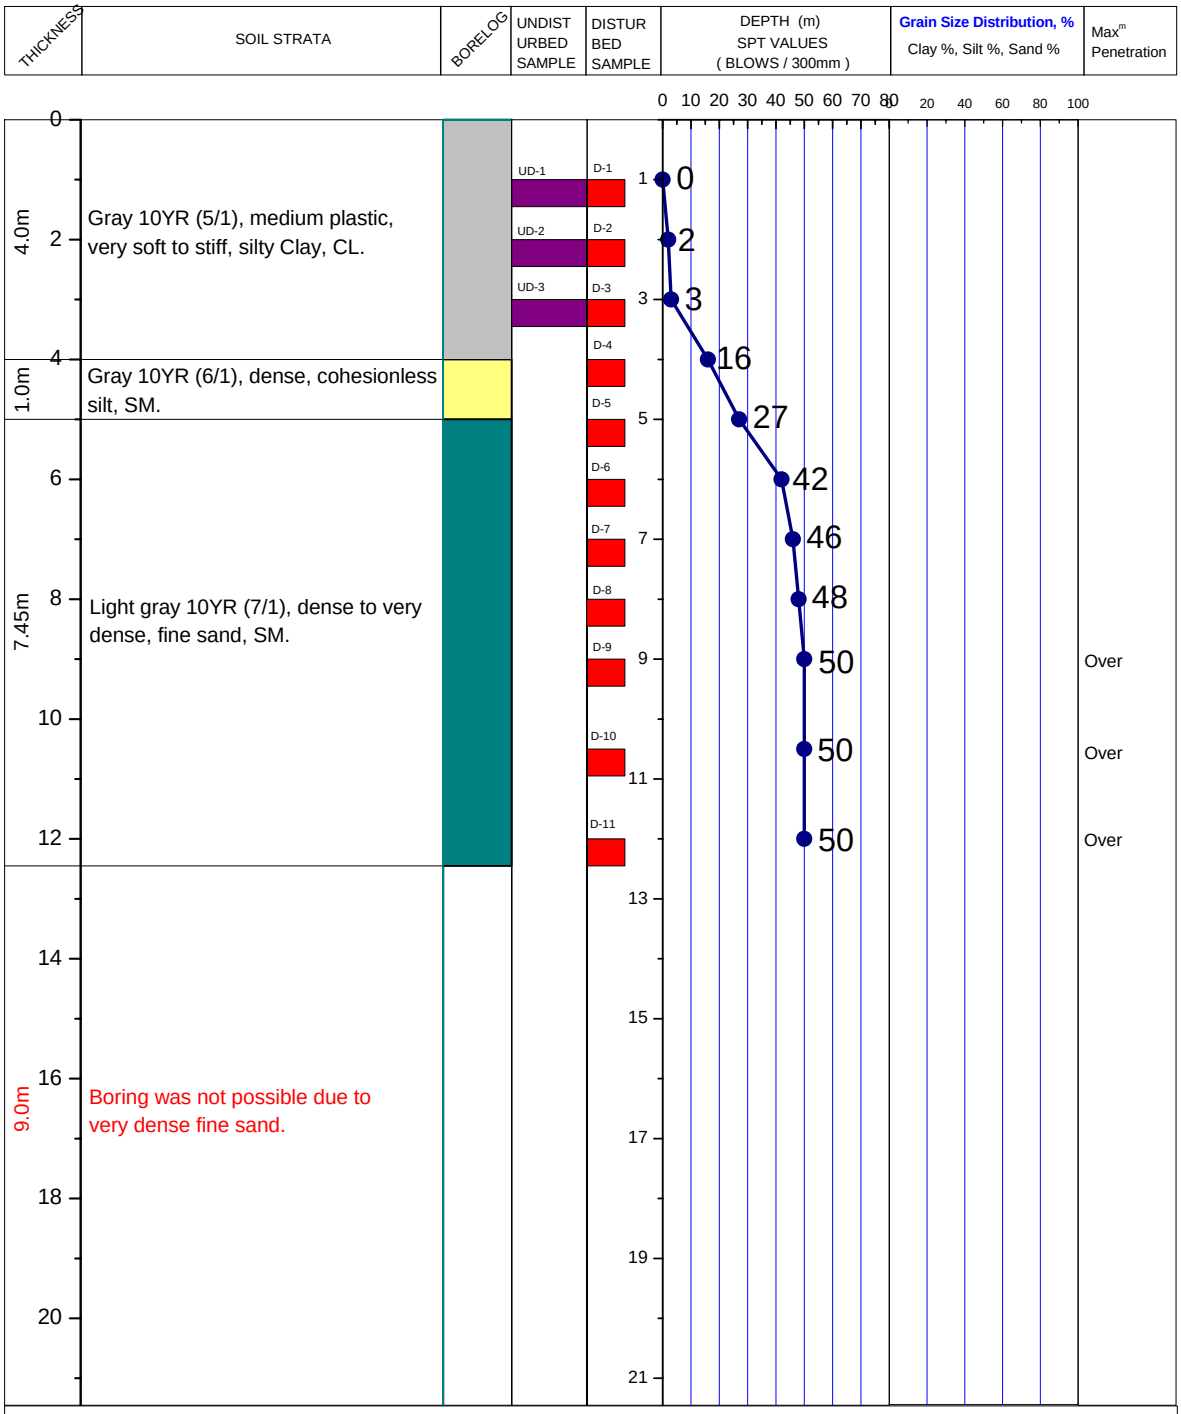

LEGEND FOR BORELOG AND GRAIN SIZE DISTRIBUTION

PLASTIC SILTY CLAY

LOW PLASTIC CLAYEY SILT

NON PLASTIC SILT

SAND

ORGANIC

UNDISTURBED SAMPLE

DISTURBED SAMPLE

SHALE

N- BLOWS DELIVERED PER FOOT BY A 140 LB HAMMER FALLING 30 INCHES

MAX^{m} PENETRATION= 50 BLOWS

AFTER 50 BLOWS PENETRATION DEPTH WERE MEASURED