A2	PROSOIL	BOREHOLE NO: BH-1	
		LOCATION: Begampur, Chuadanga Sador, Chuadanga.	
PROJECT : Telecommunication Tower.		DEPTH OF BORING: 16.5m	R. L.: 0.31m below from Road Level.
CLIENT : Grameenphone Ltd.		DATE OF BORING: 17-04-2014.	B. W. T : 2.44m below from E. G. L.

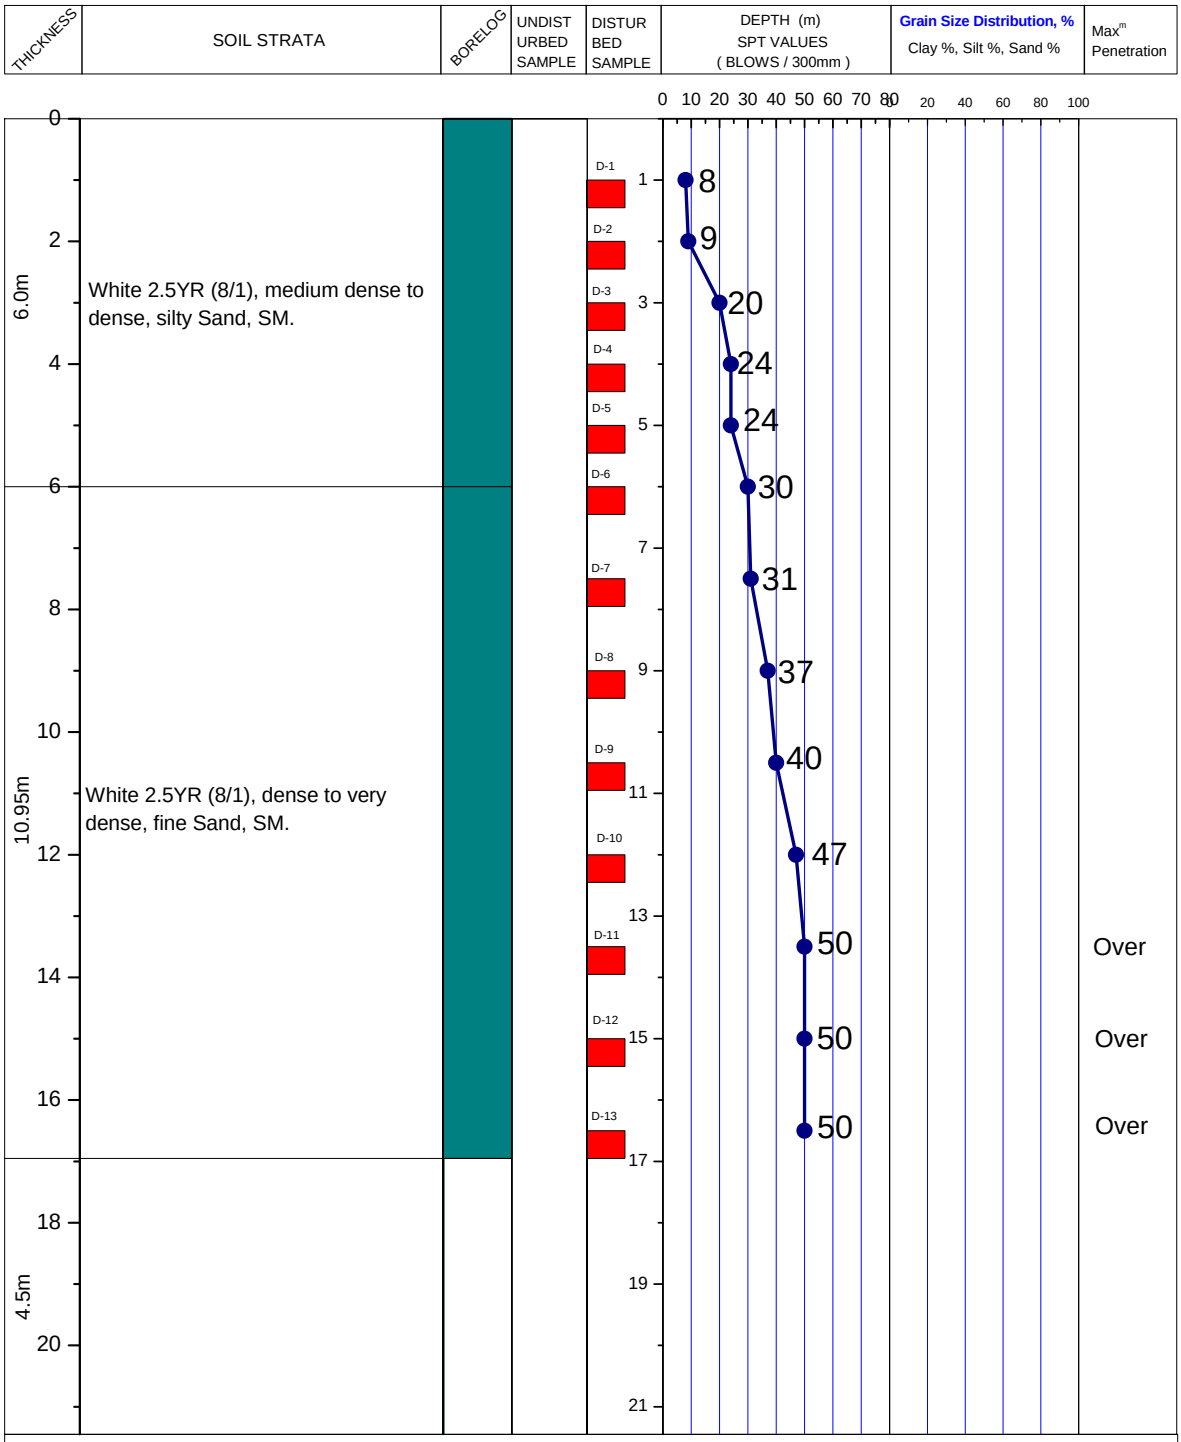

LEGEND FOR BORELOG AND GRAIN SIZE DISTRIBUTION (BASED ON 'ASTM CLASSIFICATION D-2487')

PLASTIC CLAY | SHALE | SILT | SAND

PEAT/HIGHLY ORGANIC SOIL | MICACEOUS FINE SAND/SILT | UNDISTURBED SAMPLE | DISTURBED SAMPLE

N- BLOWS DELIVERED PER FOOT BY A 140 LB HAMMER FALLING 30 INCHES

MAX^{m} PENETRATION= 50 BLOWS

AFTER 50 BLOWS PENETRATION DEPTH WERE MEASURED