A2	PROSOIL	BOREHOLE NO: BH-1	
		LOCATION: Cholitar Addar, Saker Mohammad, 5 No. Sankhola Union, **Chunarughat, Hobiganj.**	
PROJECT : Telecommunication Tower.		DEPTH OF BORING: 21.0m	R. L.: 1.22m below from Road Level.
CLIENT : Grameenphone Ltd.		DATE OF BORING: 08-05-2013.	G. W. T : 0.46m above from E. G. L.

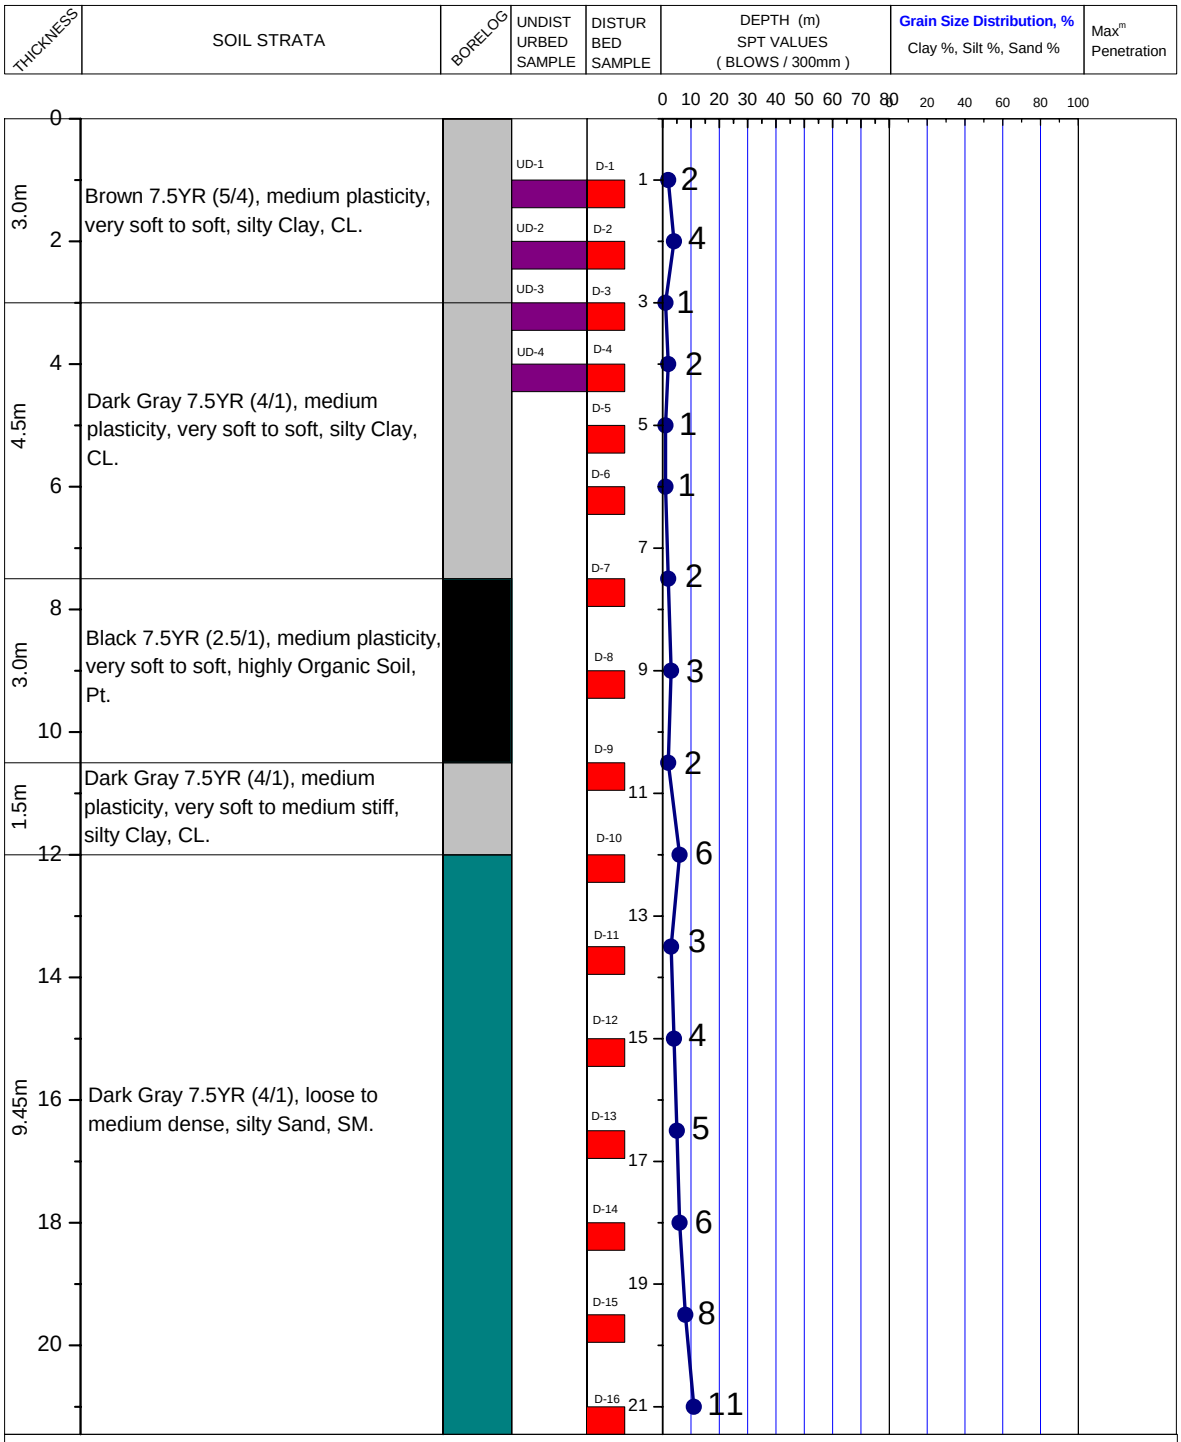

LEGEND FOR BORELOG AND GRAIN SIZE DISTRIBUTION (BASED ON 'ASTM CLASSIFICATION D-2487')

PLASTIC CLAY | SHALE | SILT | SAND

PEAT/HIGHLY ORGANIC SOIL | MICACEOUS FINE SAND/SILT | UNDISTURBED SAMPLE | DISTURBED SAMPLE

N- BLOWS DELIVERED PER FOOT BY A 140 LB HAMMER FALLING 30 INCHES

MAX^{m} PENETRATION= 50 BLOWS

AFTER 50 BLOWS PENETRATION DEPTH WERE MEASURED

A2	PROSOIL	BOREHOLE NO: BH-2	
		LOCATION: Cholitar Addar, Saker Mohammad, 5 No. Sankhola Union, **Chunarughat, Hobiganj.**	
PROJECT : Telecommunication Tower.		DEPTH OF BORING: 21.0m	R. L.: 1.22m below from Road Level.
CLIENT : Grameenphone Ltd.		DATE OF BORING: 09-05-2013.	G. W. T : 0.46m above from E. G. L.

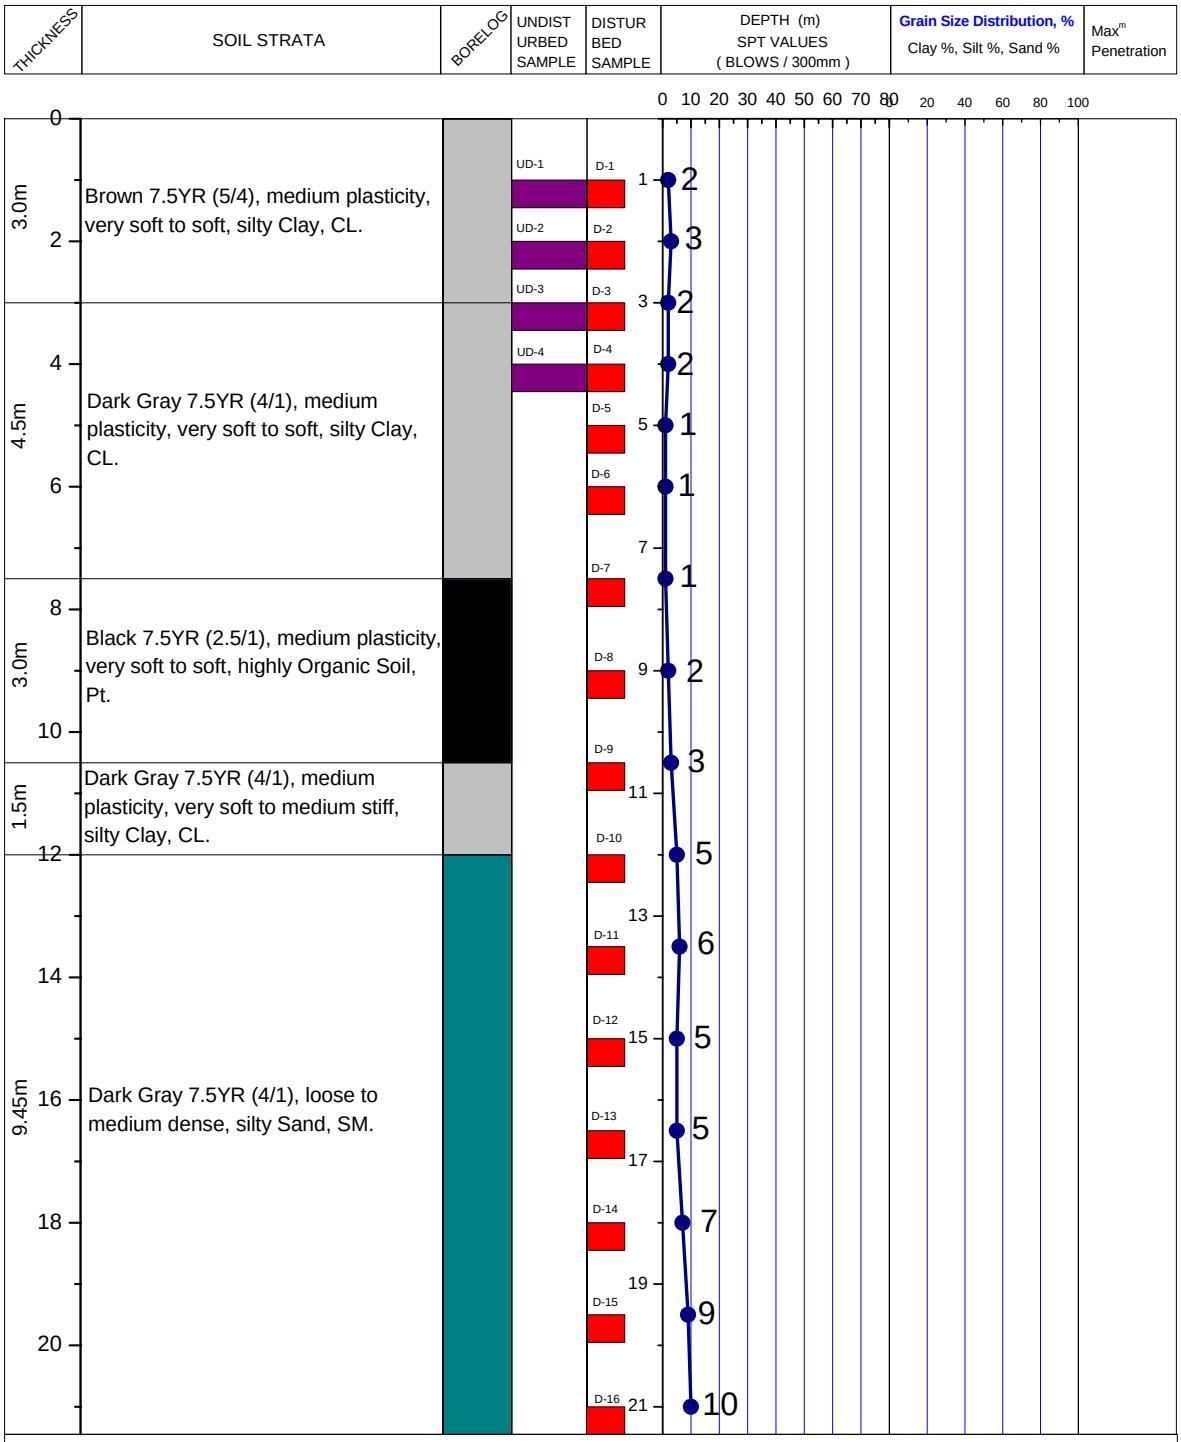

LEGEND FOR BORELOG AND GRAIN SIZE DISTRIBUTION (BASED ON 'ASTM CLASSIFICATION D-2487')

PLASTIC CLAY | SHALE | SILT | SAND

PEAT/HIGHLY ORGANIC SOIL | MICACEOUS FINE SAND/SILT | UNDISTURBED SAMPLE | DISTURBED SAMPLE

N- BLOWS DELIVERED PER FOOT BY A 140 LB HAMMER FALLING 30 INCHES

MAX^{m} PENETRATION= 50 BLOWS

AFTER 50 BLOWS PENETRATION DEPTH WERE MEASURED

A2	PROSOIL	BOREHOLE NO: BH-3	
		LOCATION: Cholitar Addar, Saker Mohammad, 5 No. Sankhola Union, **Chunarughat, Hobiganj.**	
PROJECT : Telecommunication Tower.		DEPTH OF BORING: 21.0m	R. L.: 1.22m below from Road Level.
CLIENT : Grameenphone Ltd.		DATE OF BORING: 09-05-2013.	G. W. T : 0.46m above from E. G. L.

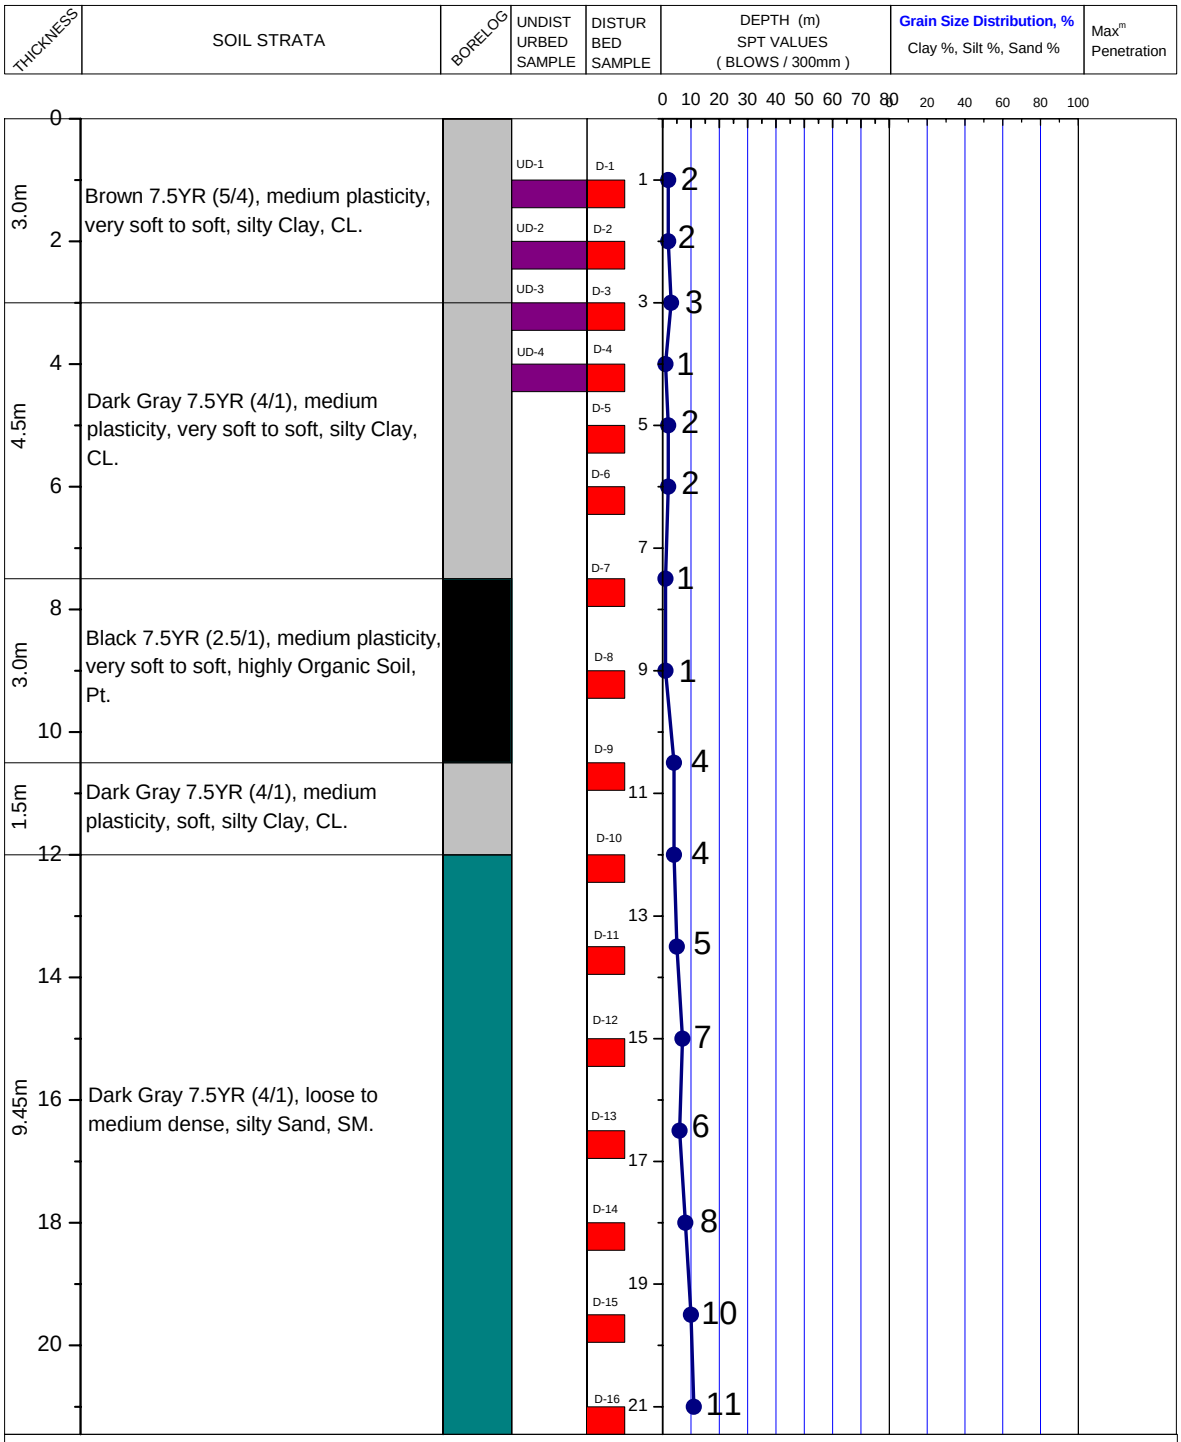

LEGEND FOR BORELOG AND GRAIN SIZE DISTRIBUTION (BASED ON 'ASTM CLASSIFICATION D-2487')

PLASTIC CLAY | SHALE | SILT | SAND

PEAT/HIGHLY ORGANIC SOIL | MICACEOUS FINE SAND/SILT | UNDISTURBED SAMPLE | DISTURBED SAMPLE

N- BLOWS DELIVERED PER FOOT BY A 140 LB HAMMER FALLING 30 INCHES

MAX^{m} PENETRATION= 50 BLOWS

AFTER 50 BLOWS PENETRATION DEPTH WERE MEASURED