A2	PROSOIL	BOREHOLE NO: BH-1	
		LOCATION : Kotalipara, Gopalganj.	
PROJECT : Kazi Akram Super Market.		DEPTH OF BORING : 51.0m	R. L. : 1.0m below from Road Level.
CLIENT : Kazi Akramuddin Ahmed.		DATE OF BORING : 31-08-2015 to 3-09-2015.	B. W. T : 1.40m below from E.G.L.

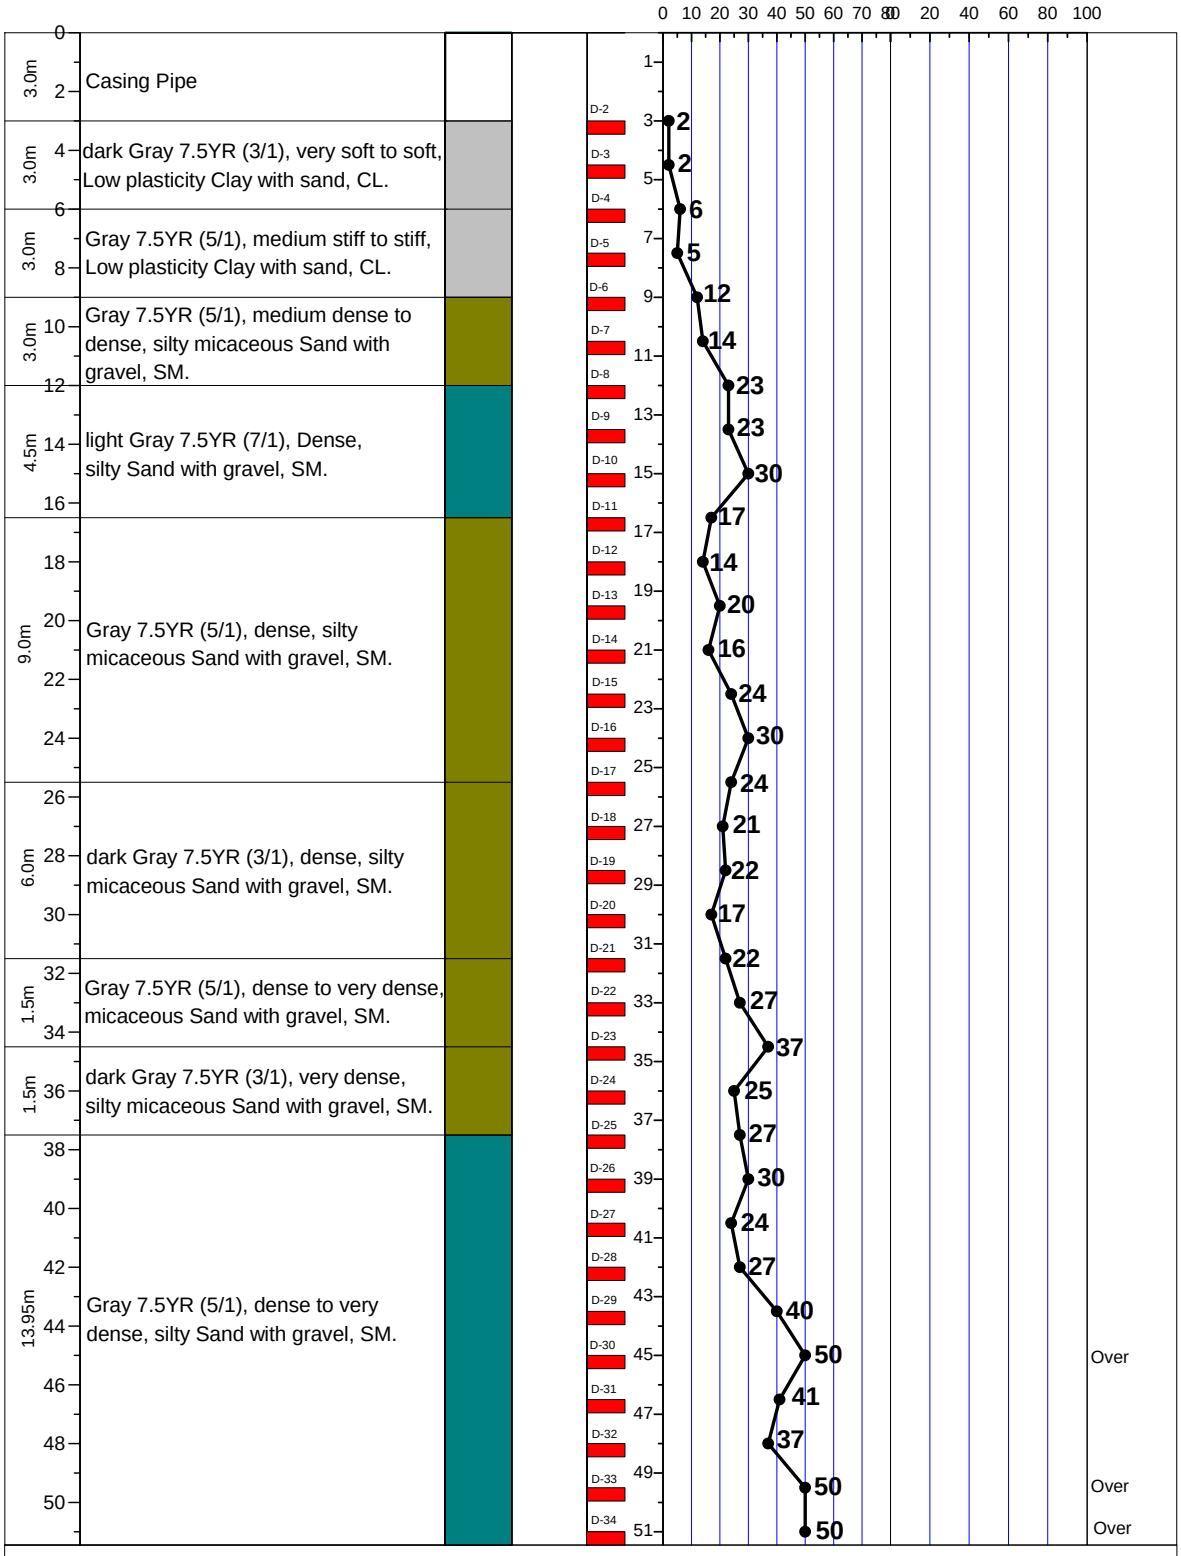

LEGEND FOR BOREHOLE AND GRAIN SIZE DISTRIBUTION (BASED ON 'ASTM CLASSIFICATION D-2487')

PLASTIC CLAY	SILT	PEAT/HIGHLY ORGANIC SOIL	UNDISTURBED SAMPLE
MICACEOUS FINE SAND/SILT	SAND	SHALE	DISTURBED SAMPLE

N- BLOWS DELIVERED PER FOOT BY A 140 LB HAMMER FALLING 30 INCHES

MAX^{m} PENETRATION= 50 BLOWS. AFTER 50 BLOWS PENETRATION DEPTH WERE MEASURED