A2 PROSOIL	BOREHOLE NO: BH-1	
	LOCATION : On Acquitted land (Dag No. 636, Mouza Bancharampur), of Bancharampur Road, B.Baria.	
PROJECT : Proposed Office Building.	DEPTH OF BORING : 33.0m	
CLIENT : Road Division, B.Baria.	DATE OF BORING: 07-02-2011.	G. W. T : 3.66m below from E.G.L.

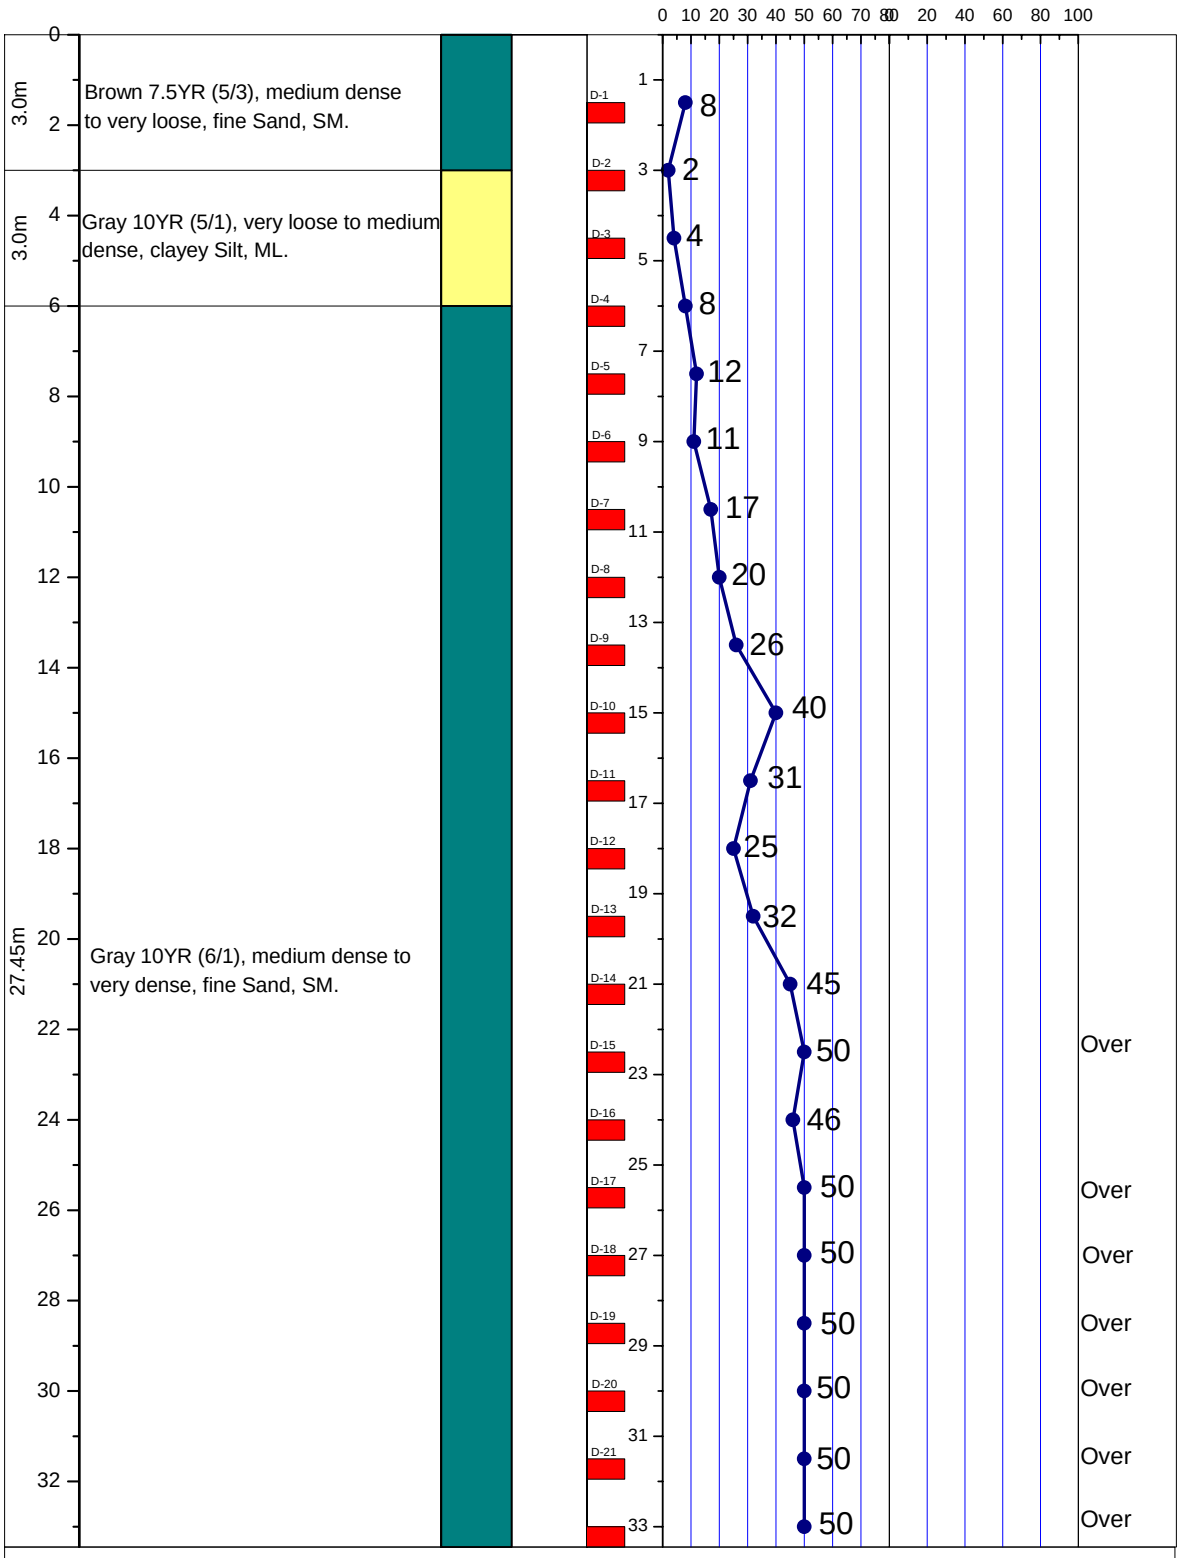

LEGEND FOR BORELOG AND GRAIN SIZE DISTRIBUTION (BASED ON 'ASTM CLASSIFICATION D-2487')

PLASTIC CLAY	SILT	PEAT/HIGHLY ORGANIC SOIL	UNDISTURBED SAMPLE
MICACEOUS FINE SAND/SILT	SAND	SHALE	DISTURBED SAMPLE

N- BLOWS DELIVERED PER FOOT BY A 140 LB HAMMER FALLING 30 INCHES

MAX^{m} PENETRATION= 50 BLOWS. AFTER 50 BLOWS PENETRATION DEPTH WERE MEASURED