A2	PROSOIL	BOREHOLE NO: BH-1	
		LOCATION : **Chainage 22+300 km on Sylhet-Salutikor-Companygonj -Bholagonj Road, Sylhet.**	
PROJECT: **Proposed Bridge from Chainage 22+309km to 22+338.5 km.**		DEPTH OF BORING : 51.0m	**Chainage: 22+331** **R. L. : 4.94**
CLIENT : Road Division, Sylhet.		DATE OF BORING: 15-02-2010.	G. W. T : 1.21m below from E.G.L.

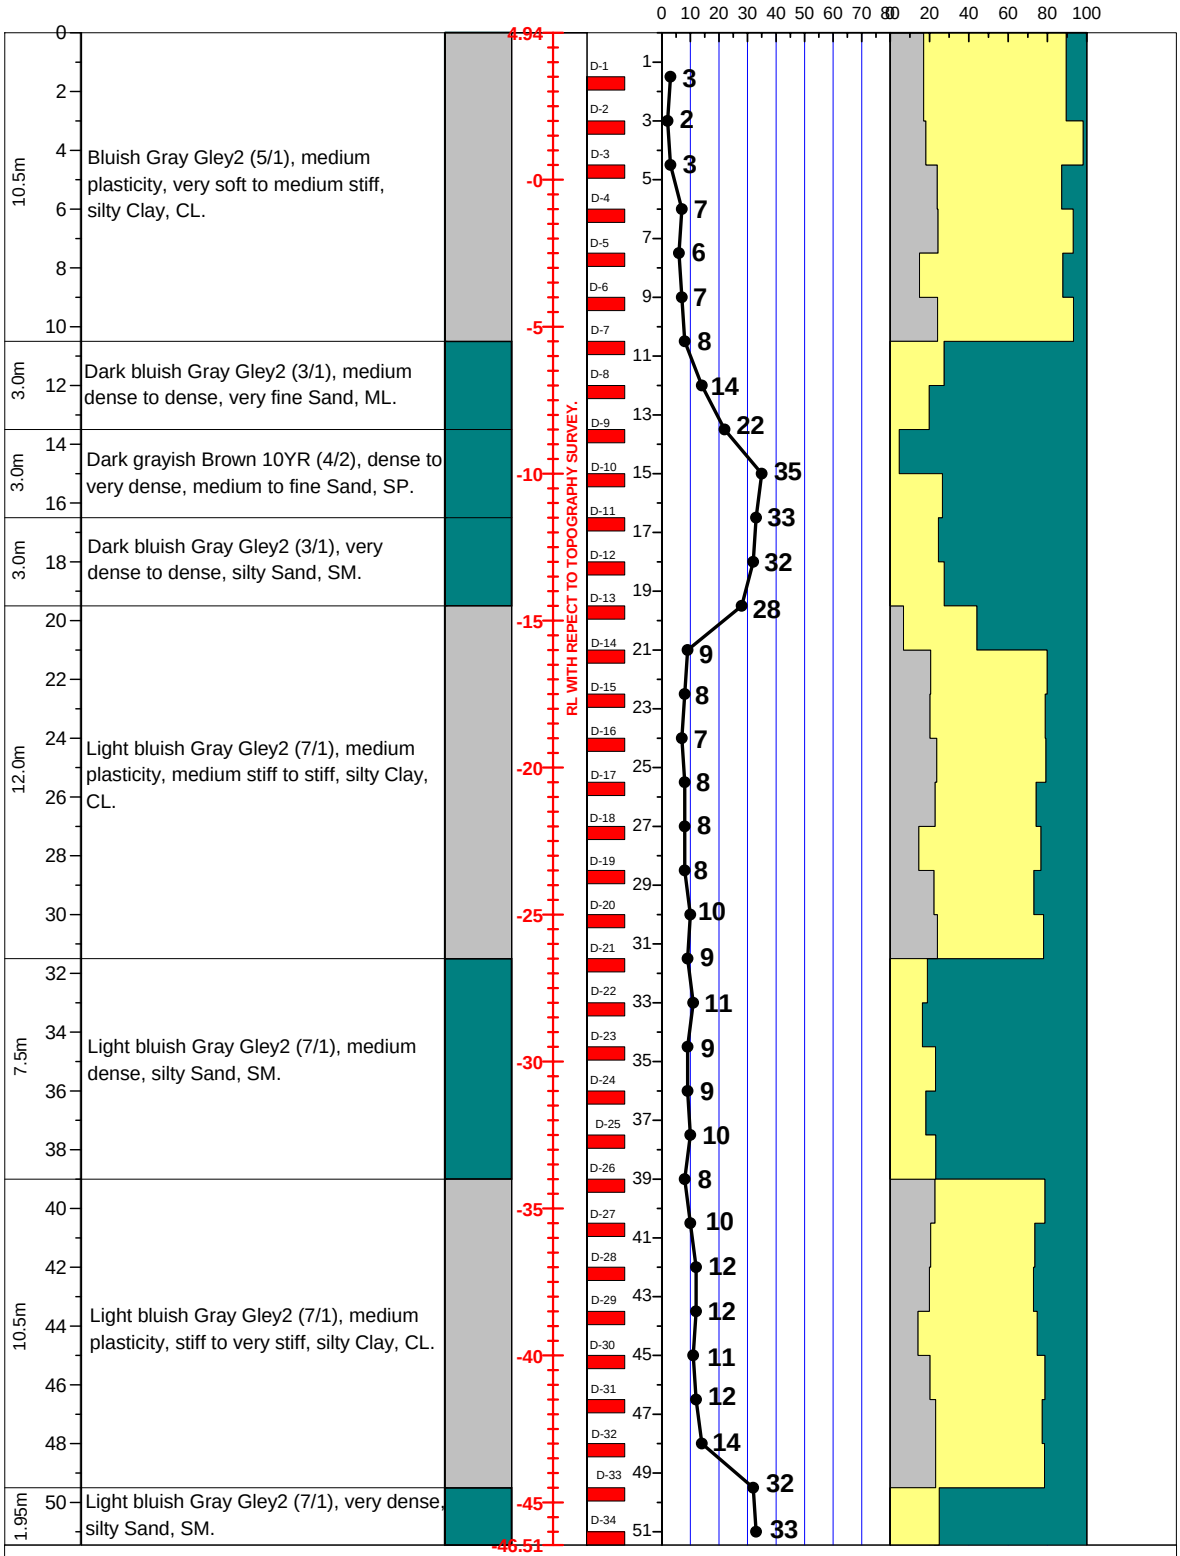

LEGEND FOR BOREHOLE AND GRAIN SIZE DISTRIBUTION (BASED ON 'ASTM CLASSIFICATION D-2487')

PLASTIC CLAY	SILT	PEAT/HIGHLY ORGANIC SOIL	UNDISTURBED SAMPLE
MICACEOUS FINE SAND/SILT	SAND	SHALE	DISTURBED SAMPLE

N- BLOWS DELIVERED PER FOOT BY A 140 LB HAMMER FALLING 30 INCHES

MAX^{m} PENETRATION= 50 BLOWS. AFTER 50 BLOWS PENETRATION DEPTH WERE MEASURED