| A2 | PROSOIL | BOREHOLE NO: BH-2 | |
|---|---|---|---|
| | | LOCATION: Vill: Bajnab, P.O: Purandia, P.S: Shibpur, District: Norshingdi. | |
| PROJECT : Telecommunication Tower. | | DEPTH OF BORING: 21.0m | R. L.: 0.76m below from Road Level. |
| CLIENT : AXIATA (Bangladesh) Ltd. | | DATE OF BORING: 23-09-2014. | B. W. T : 2.13m below from E. G. L. |

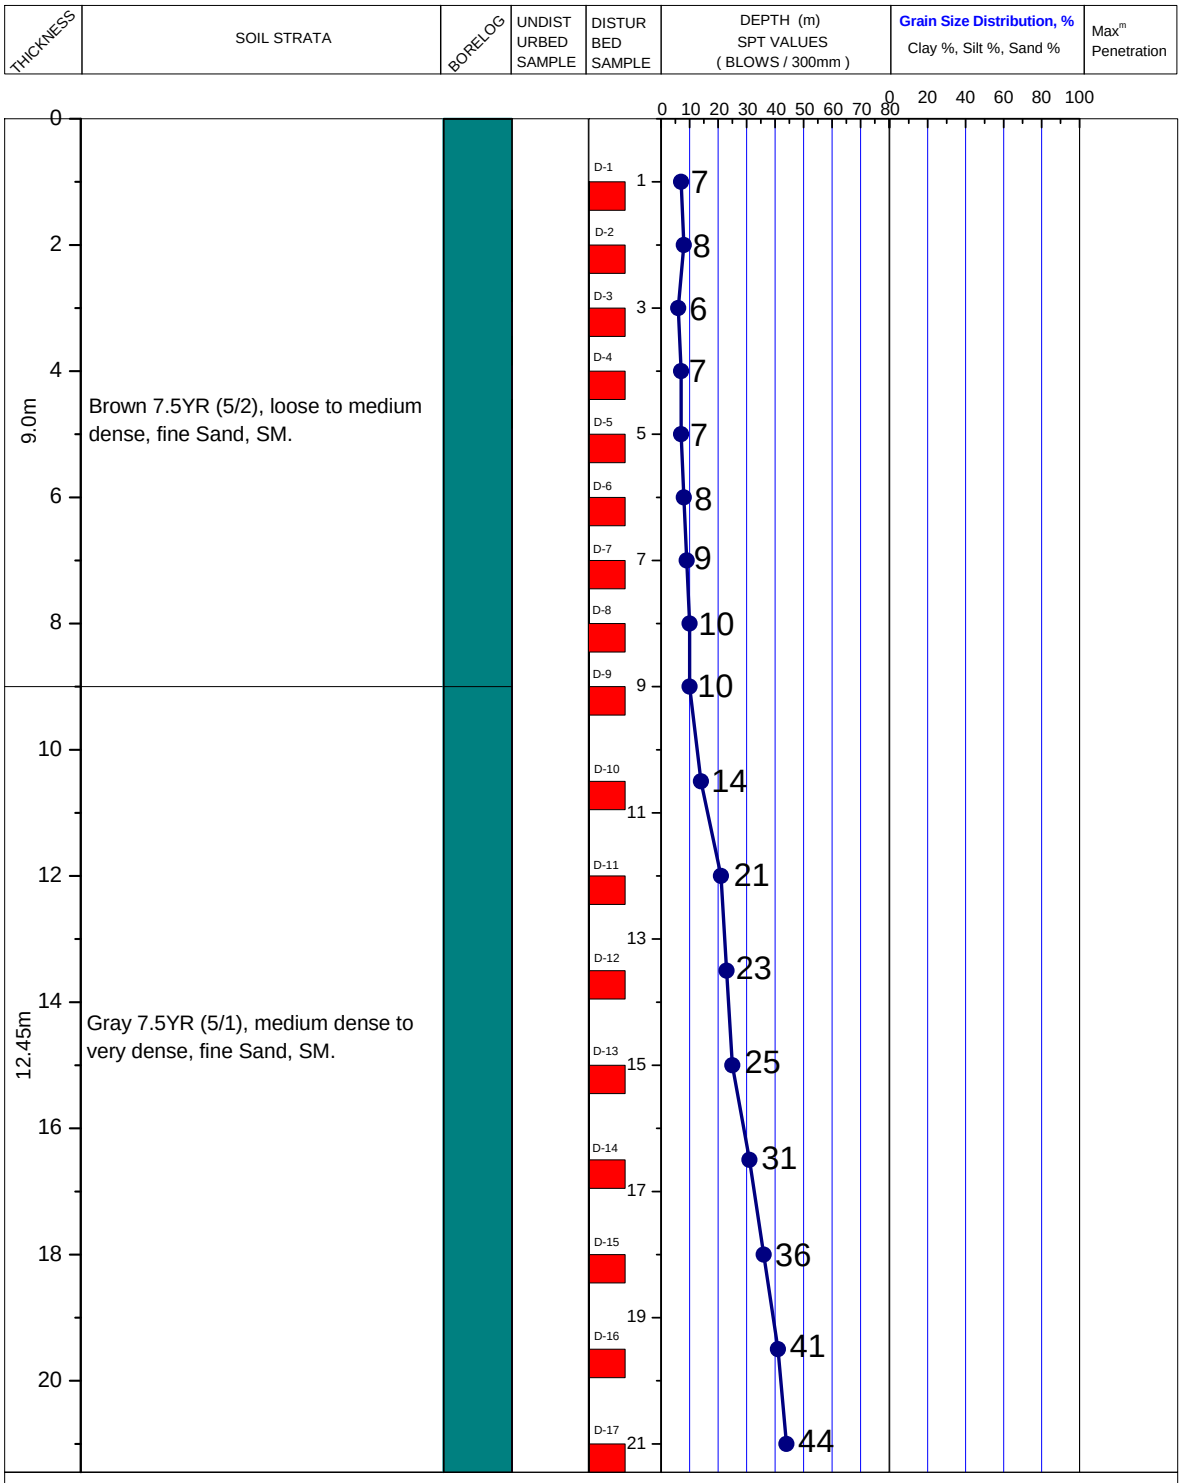


LEGEND FOR BORELOG AND GRAIN SIZE DISTRIBUTION (BASED ON 'ASTM CLASSIFICATION D-2487')

| | | | |
|---|---|---|---|
| PLASTIC CLAY | SAND | SILT | SHALE |
| PEAT/HIGHLY ORGANIC SOIL | MICACEOUS FINE SAND/SILT | UNDISTURBED SAMPLE | DISTURBED SAMPLE |

N- BLOWS DELIVERED PER FOOT BY A 140 LB HAMMER FALLING 30 INCHES

MAX^m PENETRATION= 50 BLOWS

AFTER 50 BLOWS PENETRATION DEPTH WERE MEASURED

PROSOIL FOUNDATION CONSULTANT DHAKA-1205 68/B, INDIRA ROAD

Md. Shamsul Islam

(Engr. Md. Shamsul Islam)
B. Sc. Engg. (Civil, BUET),
M. Engg. (Geotech), MCSD, FIEB, CCPE
Chief Executive
Prosoil Foundation Consultant