
A2	PROSOIL	Borehole No: 02	Easting: 239557	Northing: 2738585
		Location: Kewatkhali Rail Crossing Mymensingh		Borehole Depth: 130.5m
Name of Project: Kewatkhali Bridge Project.		Type of Drill Rig: Mechanical Rotary Drilling.		R. L. : 14.125m
CLIENT: Roads & Highways Department, Mymensingh.		Date of Boring: 29-03-2022 to 07-04-2022		B. W. T : 8.4m below from E. G. L.

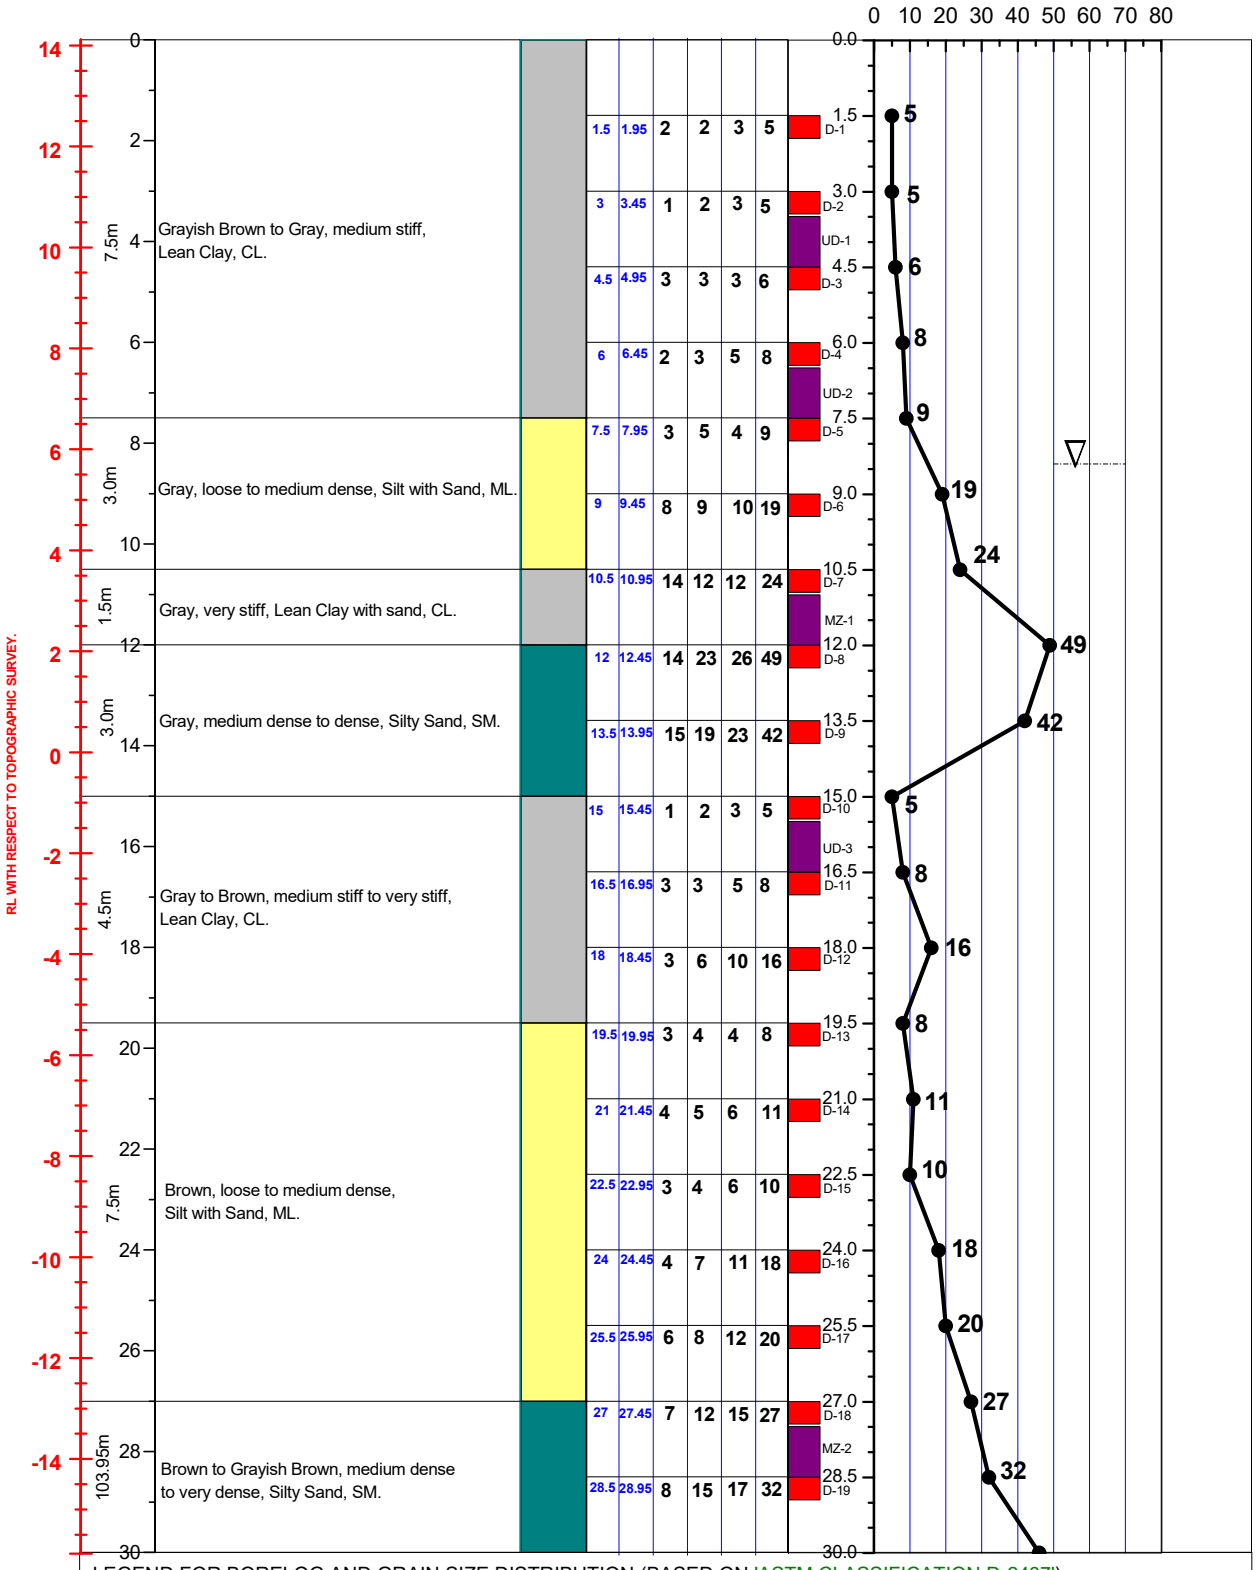

LEGEND FOR BORELOG AND GRAIN SIZE DISTRIBUTION (BASED ON 'ASTM CLASSIFICATION D-2487')

PLASTIC CLAY | SILT | PEAT/HIGHLY ORGANIC SOIL | UNDISTURBED SAMPLE

MICACEOUS FINE SAND/SILT | SAND | SHALE | DISTURBED SAMPLE

N- BLOWS DELIVERED PER FOOT BY A 140 LB HAMMER FALLING 30 INCHES

MAX^{m} PENETRATION= 50 BLOWS. AFTER 50 BLOWS PENETRATION DEPTH WERE MEASURED