
A2 PROSOIL	BOREHOLE NO: BH-01	
	LOCATION : Munshiganj	
PROJECT : Jinjira-Keraniganj-Nawabganj-Dohar-Srinagar Highway Development (with Kadamtoli to Johnny Tower Link) (R-820)	DEPTH OF BORING : 30.0m	R. L. : 9.91m
CLIENT : ROADS & HIGHWAYS DEPARTMENT.	DATE OF BORING : 11-02-2021	B. W. T : 2.5m below from E. G. L.

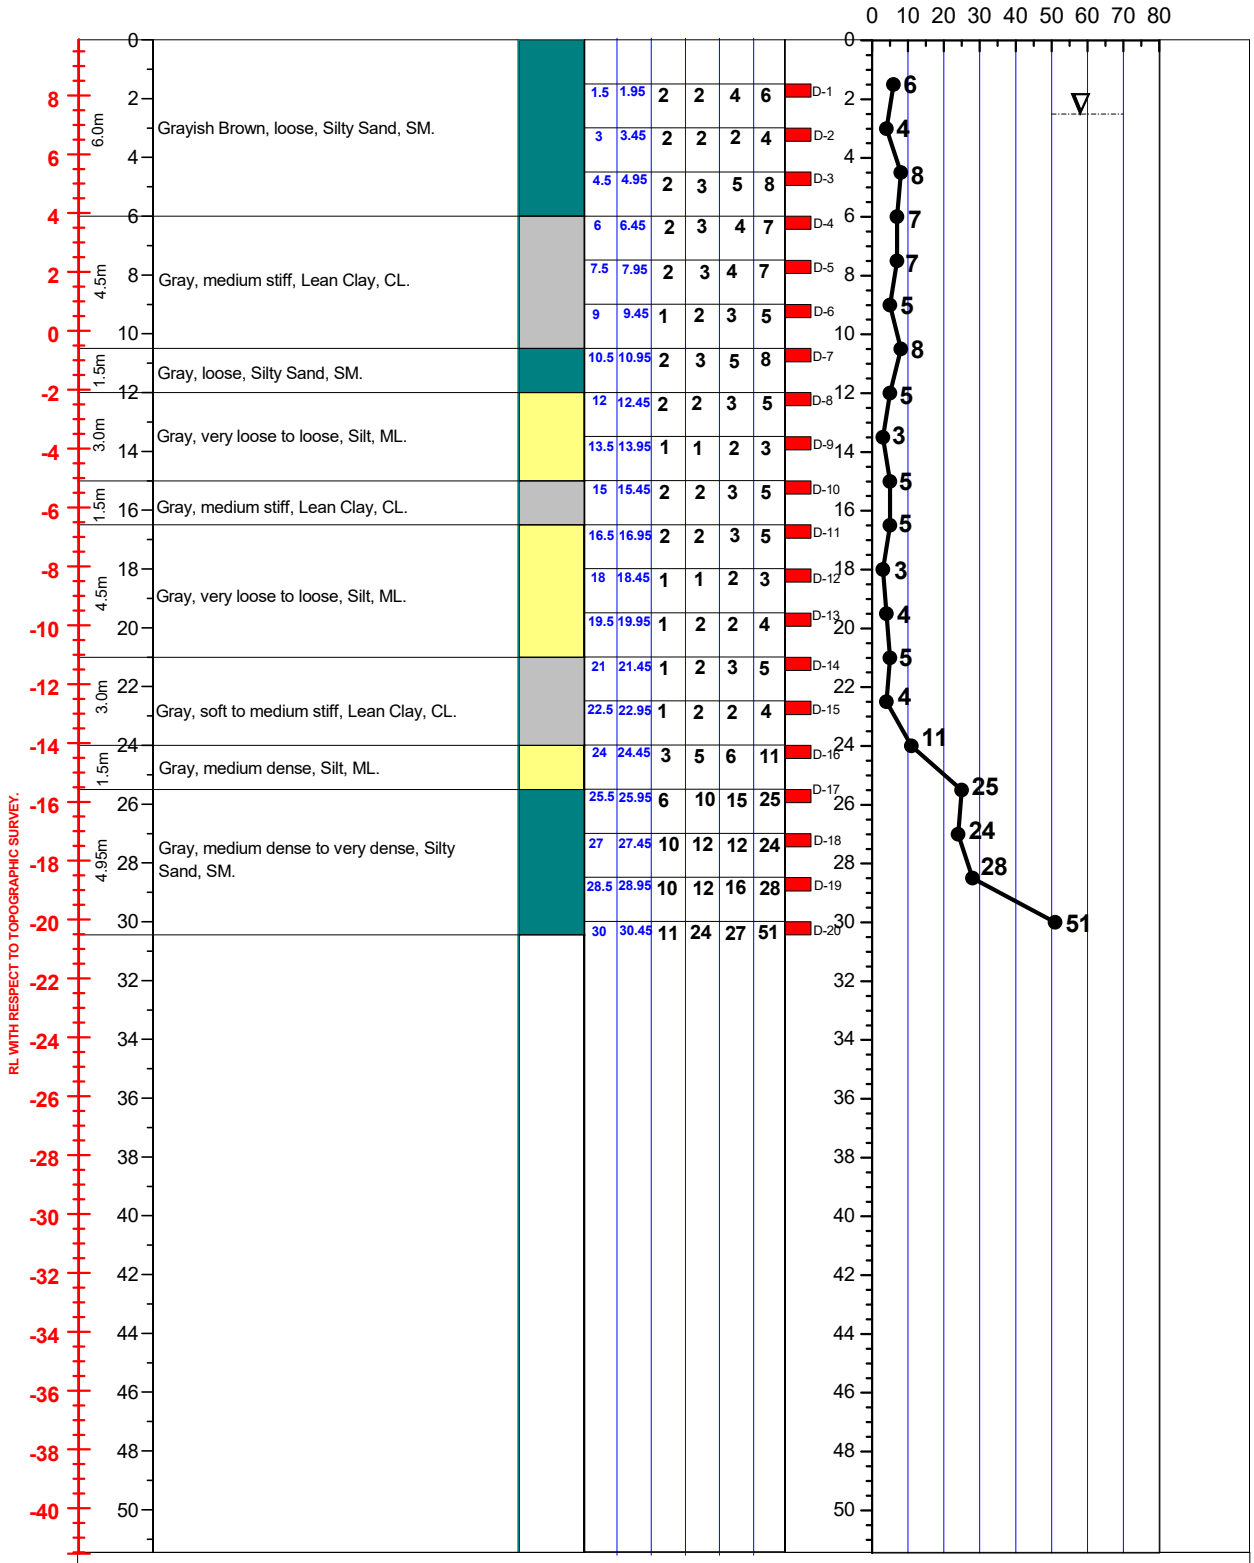

LEGEND FOR BOREHOLE AND GRAIN SIZE DISTRIBUTION (BASED ON 'ASTM CLASSIFICATION D-2487')

PLASTIC CLAY	SILT	PEAT/HIGHLY ORGANIC SOIL	UNDISTURBED SAMPLE
MICACEOUS FINE SAND/SILT	SAND	SHALE	DISTURBED SAMPLE

N- BLOWS DELIVERED PER FOOT BY A 140 LB HAMMER FALLING 30 INCHES

MAX^m PENETRATION= 50 BLOWS. AFTER 50 BLOWS PENETRATION DEPTH WERE MEASURED