A2	PROSOIL	BOREHOLE NO: BH-1	
		LOCATION : LRP Ch. 8.800 Km on Sylhet-Sunamgonj Road.	
PROJECT : Construction of Proposed Bridge.		DEPTH OF BORING : 33.0m	R. L.: Road Level.
CLIENT : Road Division, Sylhet.		DATE OF BORING : 20-10-2009.	G. W. T : 1.83m below from E.G.L.

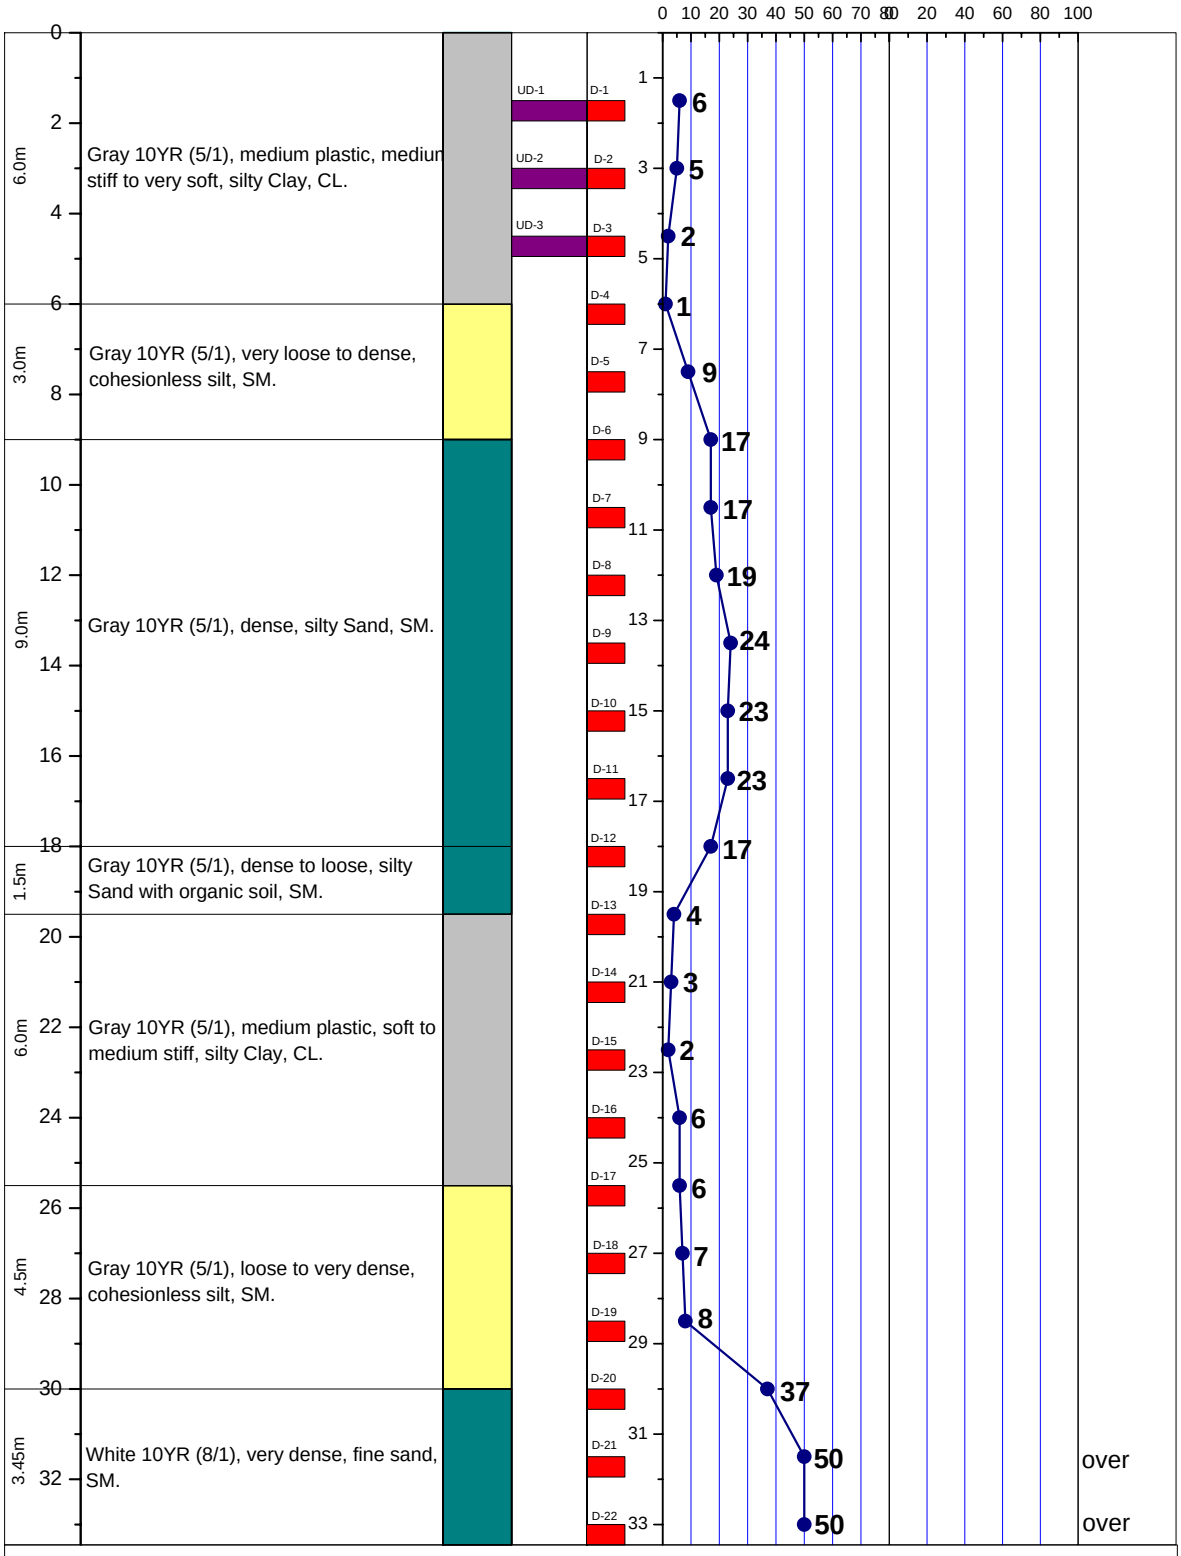

LEGEND FOR BORELOG AND GRAIN SIZE DISTRIBUTION

PLASTIC SILTY CLAY	NON PLASTIC SILT	ORGANIC	DISTURBED SAMPLE
LOW PLASTIC CLAYEY SILT	SAND	SHALE	UNDISTURBED SAMPLE

N- BLOWS DELIVERED PER FOOT BY A 140 LB HAMMER FALLING 30 INCHES

MAX^{m} PENETRATION= 50 BLOWS. AFTER 50 BLOWS PENETRATION DEPTH WERE MEASURED