A2 PROSOIL	BOREHOLE NO: BH-1	
	LOCATION : Chainage 12+305.5 km on Darbos (Sylhet-Jaflong High way) -Kanaighat Road, Sylhet.	
PROJECT : Proposed Darbos-Kanaighat Bridge from Chainage 12+305.5 to 12+330.62 km.)	DEPTH OF BORING : 33.0m	Chainage: 12+301.75 R. L. : 9.85
CLIENT : Road Division, Sylhet.	DATE OF BORING : 19-02-2010.	G. W. T : 0.30m below from E.G.L.

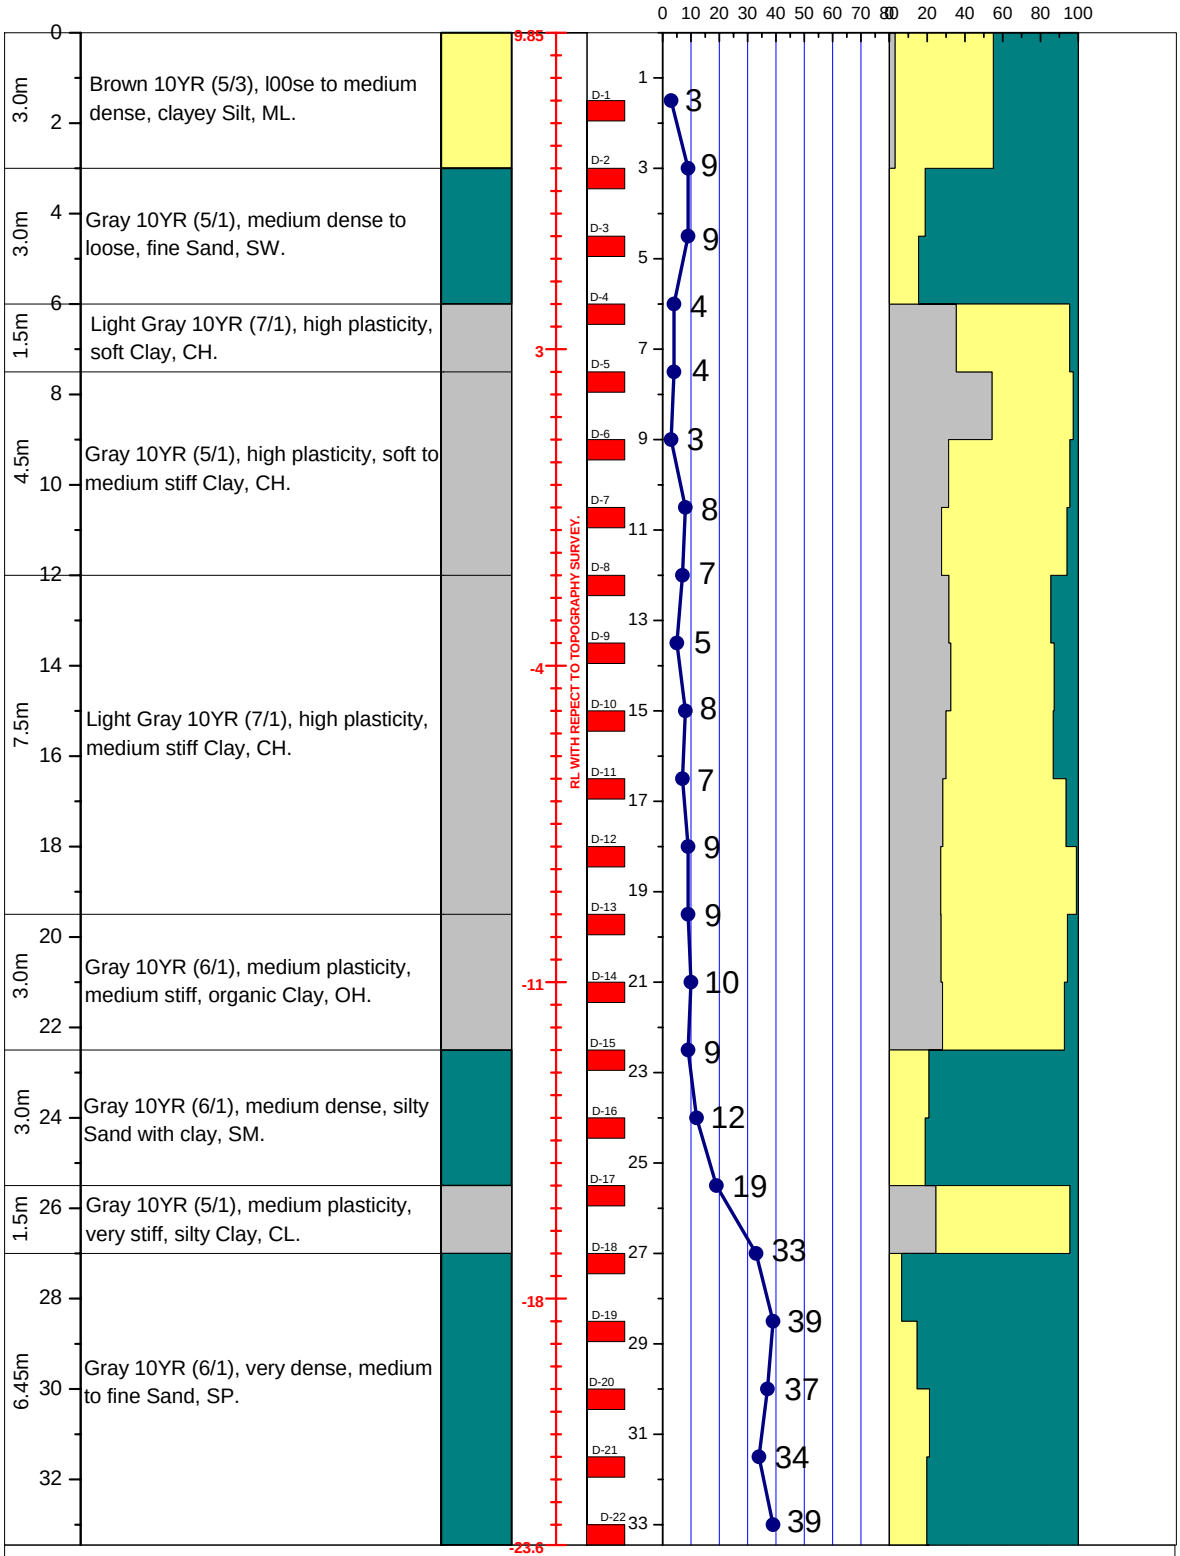

LEGEND FOR BORELOG AND GRAIN SIZE DISTRIBUTION (BASED ON 'ASTM CLASSIFICATION D-2487')

PLASTIC CLAY	SILT	PEAT/HIGHLY ORGANIC SOIL	UNDISTURBED SAMPLE
MICACEOUS FINE SAND/SILT	SAND	SHALE	DISTURBED SAMPLE

N- BLOWS DELIVERED PER FOOT BY A 140 LB HAMMER FALLING 30 INCHES

MAX^m PENETRATION= 50 BLOWS. AFTER 50 BLOWS PENETRATION DEPTH WERE MEASURED