| A2 | PROSOIL | BOREHOLE NO: BH-1 | |
|---|---|---|---|
| | | LOCATION : Majid jarina Foundation, Shariatpur Sadar. | |
| PROJECT : Construction of Auditorium Building. | | DEPTH OF BORING : 30.0m | R. L.: 1.5m below from Road Level. |
| CLIENT : Majid jarina Foundation. | | DATE OF BORING: 16-03-2015. | B. W. T : 0.60m below from E.G.L. |

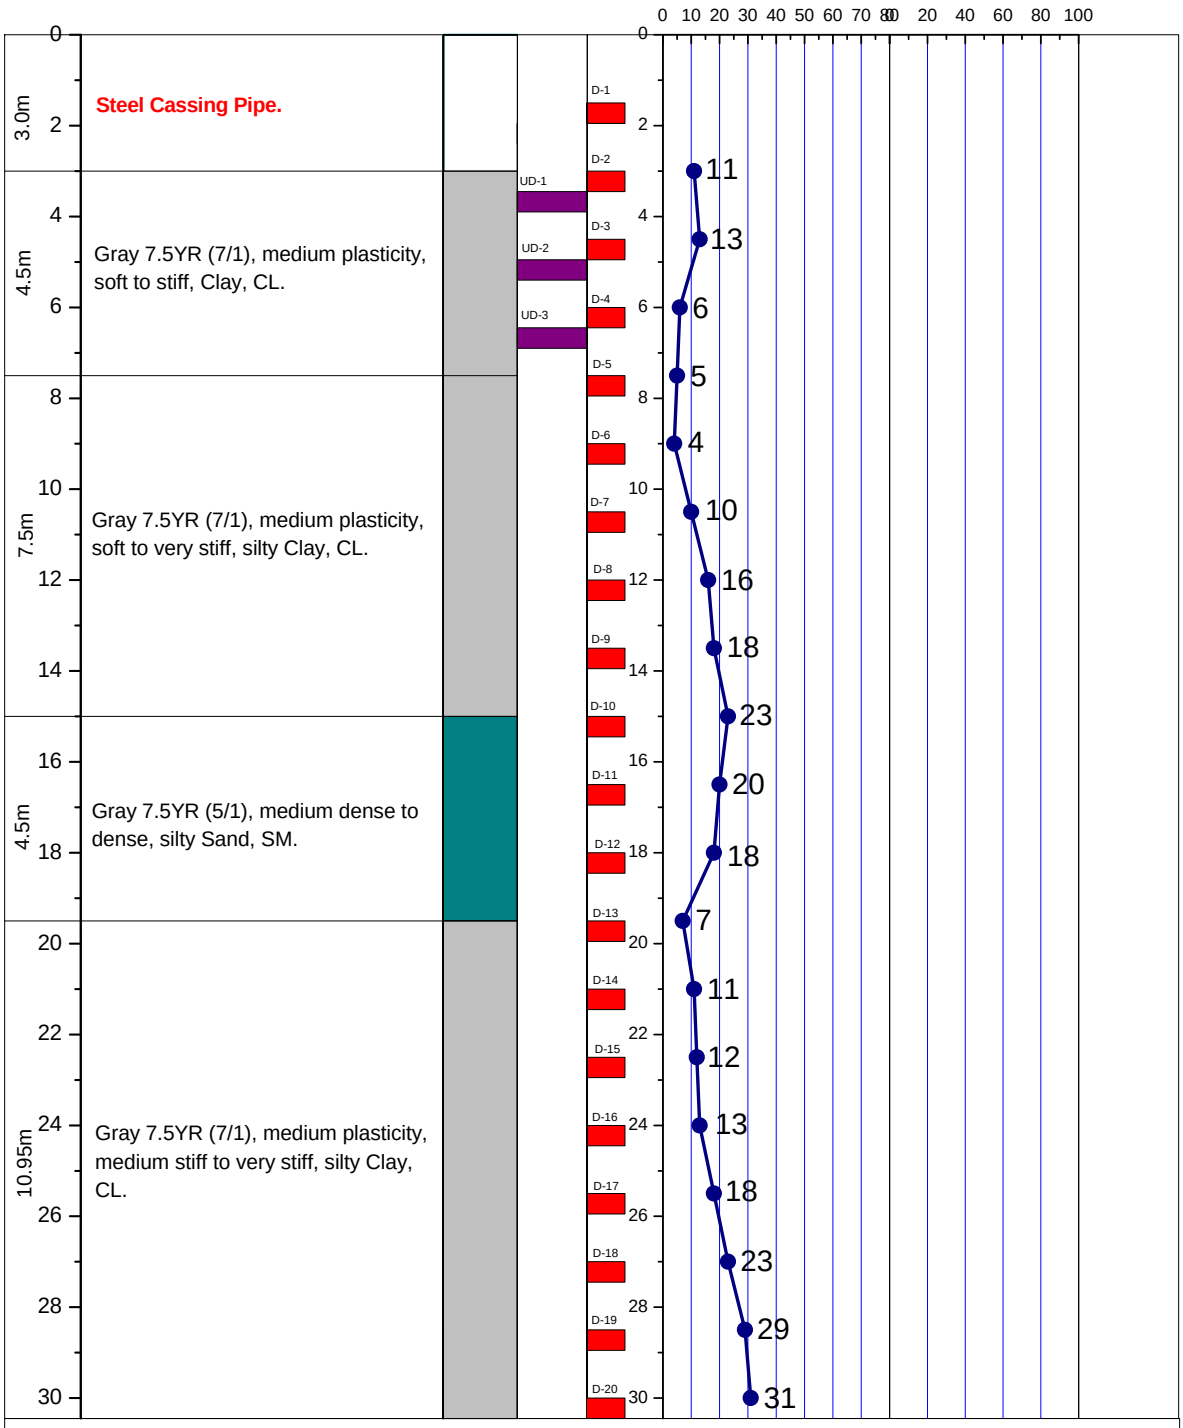


LEGEND FOR BORELOG AND GRAIN SIZE DISTRIBUTION (BASED ON 'ASTM CLASSIFICATION D-2487')

| | | | |
|---|---|---|---|
| PLASTIC CLAY | SILT | SHALE | UNDISTURBED SAMPLE |
| MICACEOUS FINE SAND/SILT | SAND | PEAT/HIGHLY ORGANIC SOIL | DISTURBED SAMPLE |

N- BLOWS DELIVERED PER FOOT BY A 140 LB HAMMER FALLING 30 INCHES

MAX$^{m}$ PENETRATION= 50 BLOWS
AFTER 50 BLOWS PENETRATION DEPTH WERE MEASURED