A2 PROSOIL	BOREHOLE NO: BH-1	
	LOCATION : 11th K.M. (Panchasar) of Fatullah-Munshigonj-Lauhagonj -Mawa Road, Munshigonj.	
PROJECT : Construction of 4 Storied R.C.C Framed Structure of Munshigonj Road Division office.	DEPTH OF BORING : 36.0m	Chainage: 11+000 R. L. : 5.15
CLIENT : Road Division, Munshigonj.	DATE OF BORING : 28-04-2010.	G. W. T : 1.22m below from E.G.L.

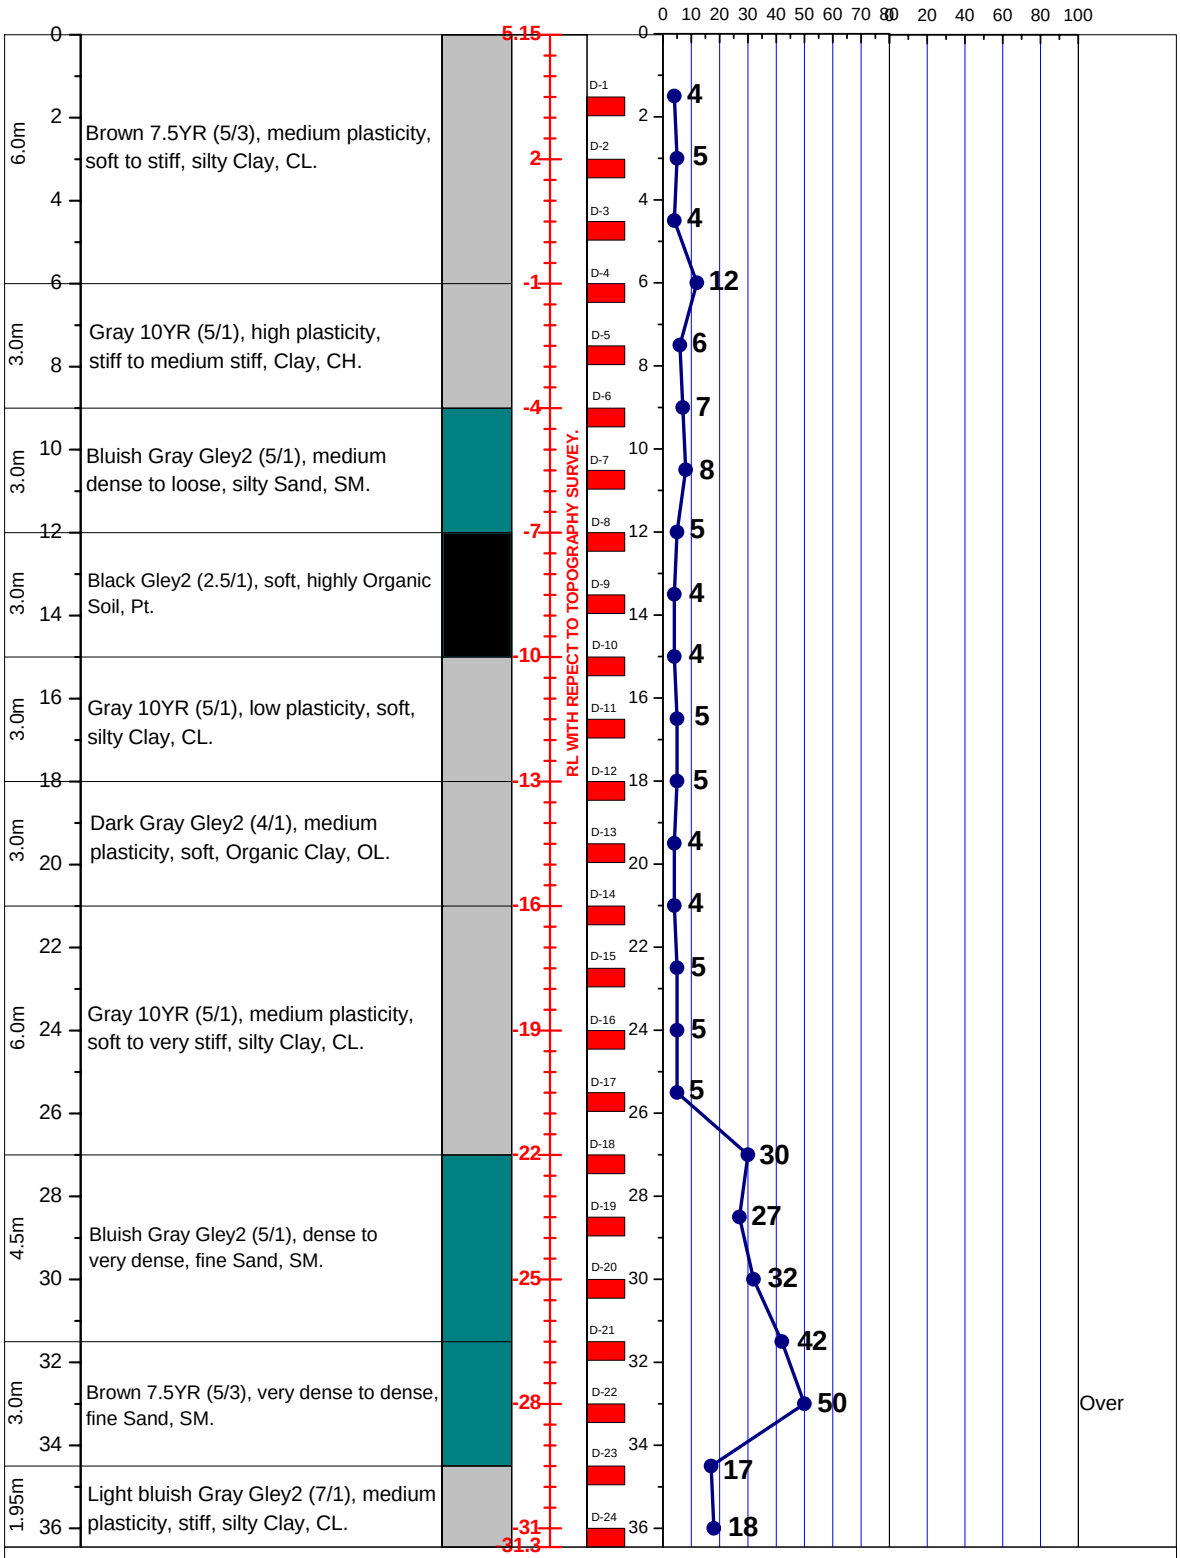

LEGEND FOR BORELOG AND GRAIN SIZE DISTRIBUTION (BASED ON 'ASTM CLASSIFICATION D-2487')

PLASTIC CLAY	SILT	PEAT/HIGHLY ORGANIC SOIL	UNDISTURBED SAMPLE
MICACEOUS FINE SAND/SILT	SAND	SHALE	DISTURBED SAMPLE

N- BLOWS DELIVERED PER FOOT BY A 140 LB HAMMER FALLING 30 INCHES

MAX^m PENETRATION= 50 BLOWS. AFTER 50 BLOWS PENETRATION DEPTH WERE MEASURED