A2	PROSOIL	BOREHOLE NO: BH-1	
		LOCATION : Chainage 9+954 to 10+064m at Feni-Chagalniya Road (Masterpara-Alakdia-Valukdia-Laskarhat-Santirhat) Road.	
PROJECT : Bhuiyarhat Bridge at Gap No 11/1.		DEPTH OF BORING : 42.0m	Chainage: 9+993 R. L. : 4.98
CLIENT : Road Division, Feni.		DATE OF BORING : 26-12-2011.	G. W. T : 0.31m below from E.G.L.

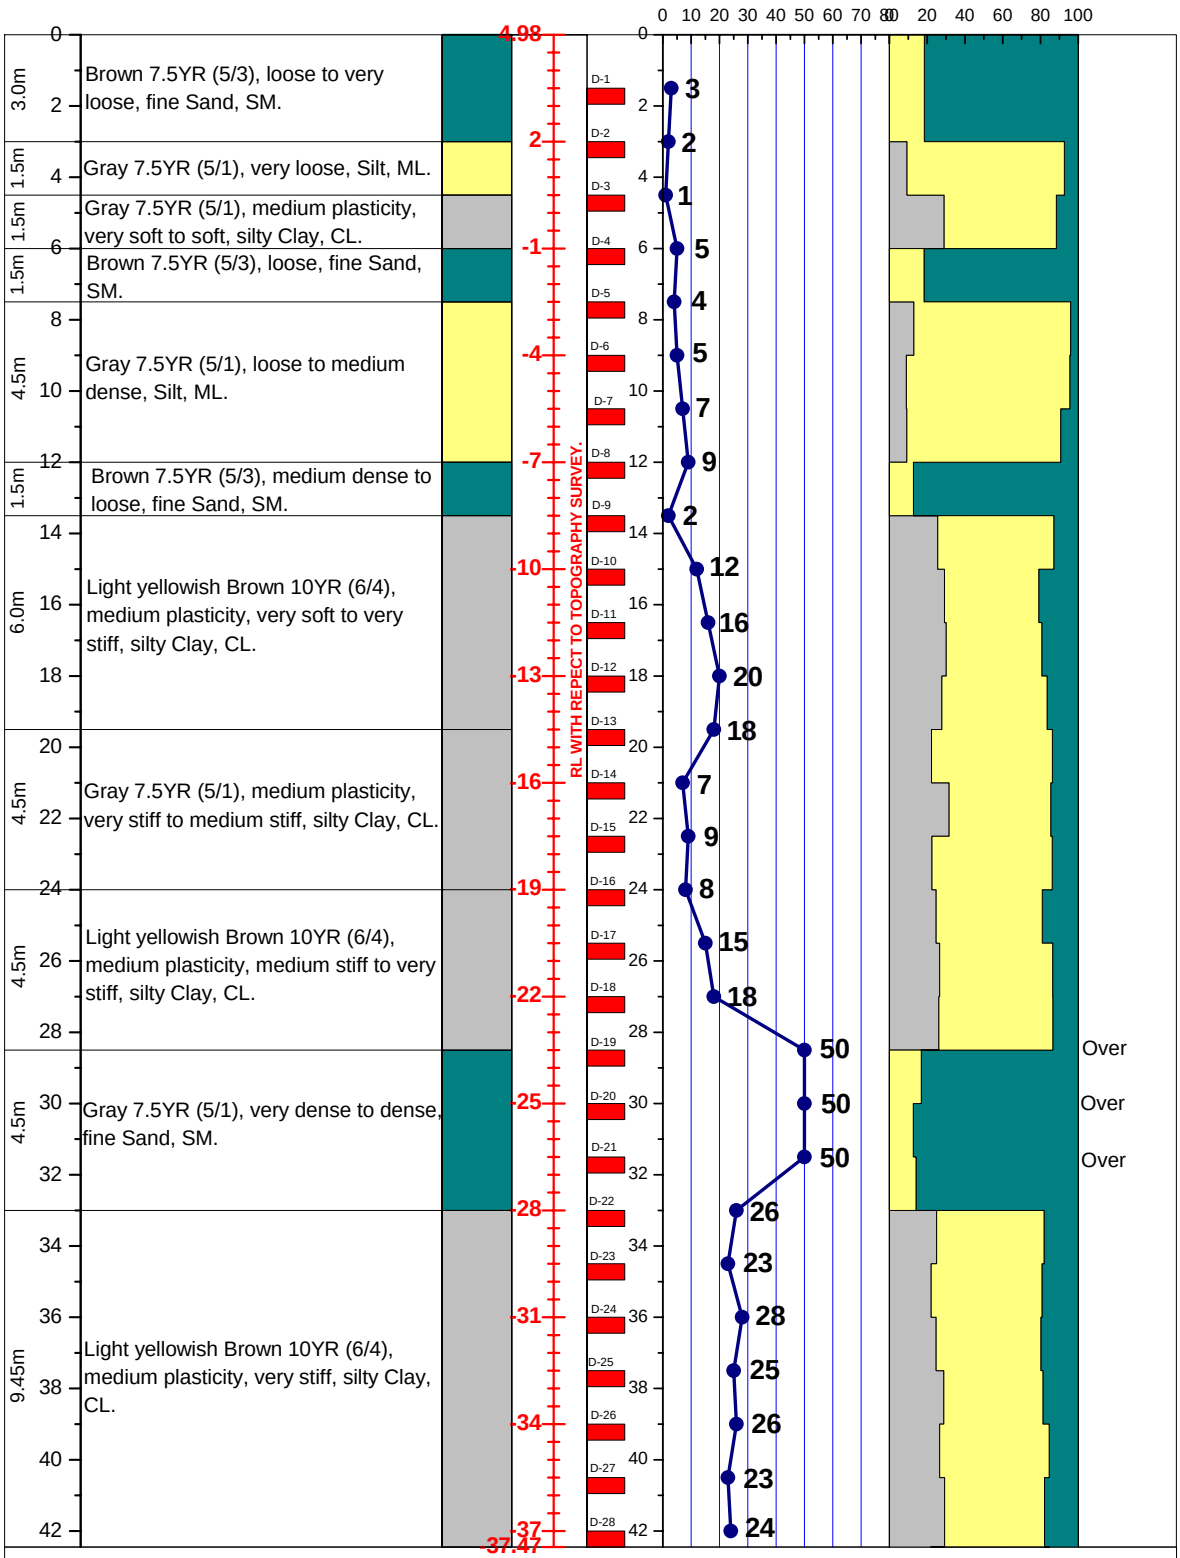

LEGEND FOR BORELOG AND GRAIN SIZE DISTRIBUTION (BASED ON 'ASTM CLASSIFICATION D-2487')

PLASTIC CLAY	SILT	PEAT/HIGHLY ORGANIC SOIL	UNDISTURBED SAMPLE
MICACEOUS FINE SAND/SILT	SAND	SHALE	DISTURBED SAMPLE

N- BLOWS DELIVERED PER FOOT BY A 140 LB HAMMER FALLING 30 INCHES

MAX^m PENETRATION= 50 BLOWS. AFTER 50 BLOWS PENETRATION DEPTH WERE MEASURED