A2 PROSOIL	BOREHOLE NO: BH-1	
	LOCATION : LRP 001+750 of Dharkhar-Akhaura-Senarbadi Road.	
PROJECT : Construction of Proposed Tanmandail Baily Bridge.	DEPTH OF BORING : 51.0m	R. L.: 5.3m below from Road Level.
CLIENT : Road Division, B.Baria.	DATE OF BORING : 20-05-2009.	G. W. T : 0.91m below from E.G.L.

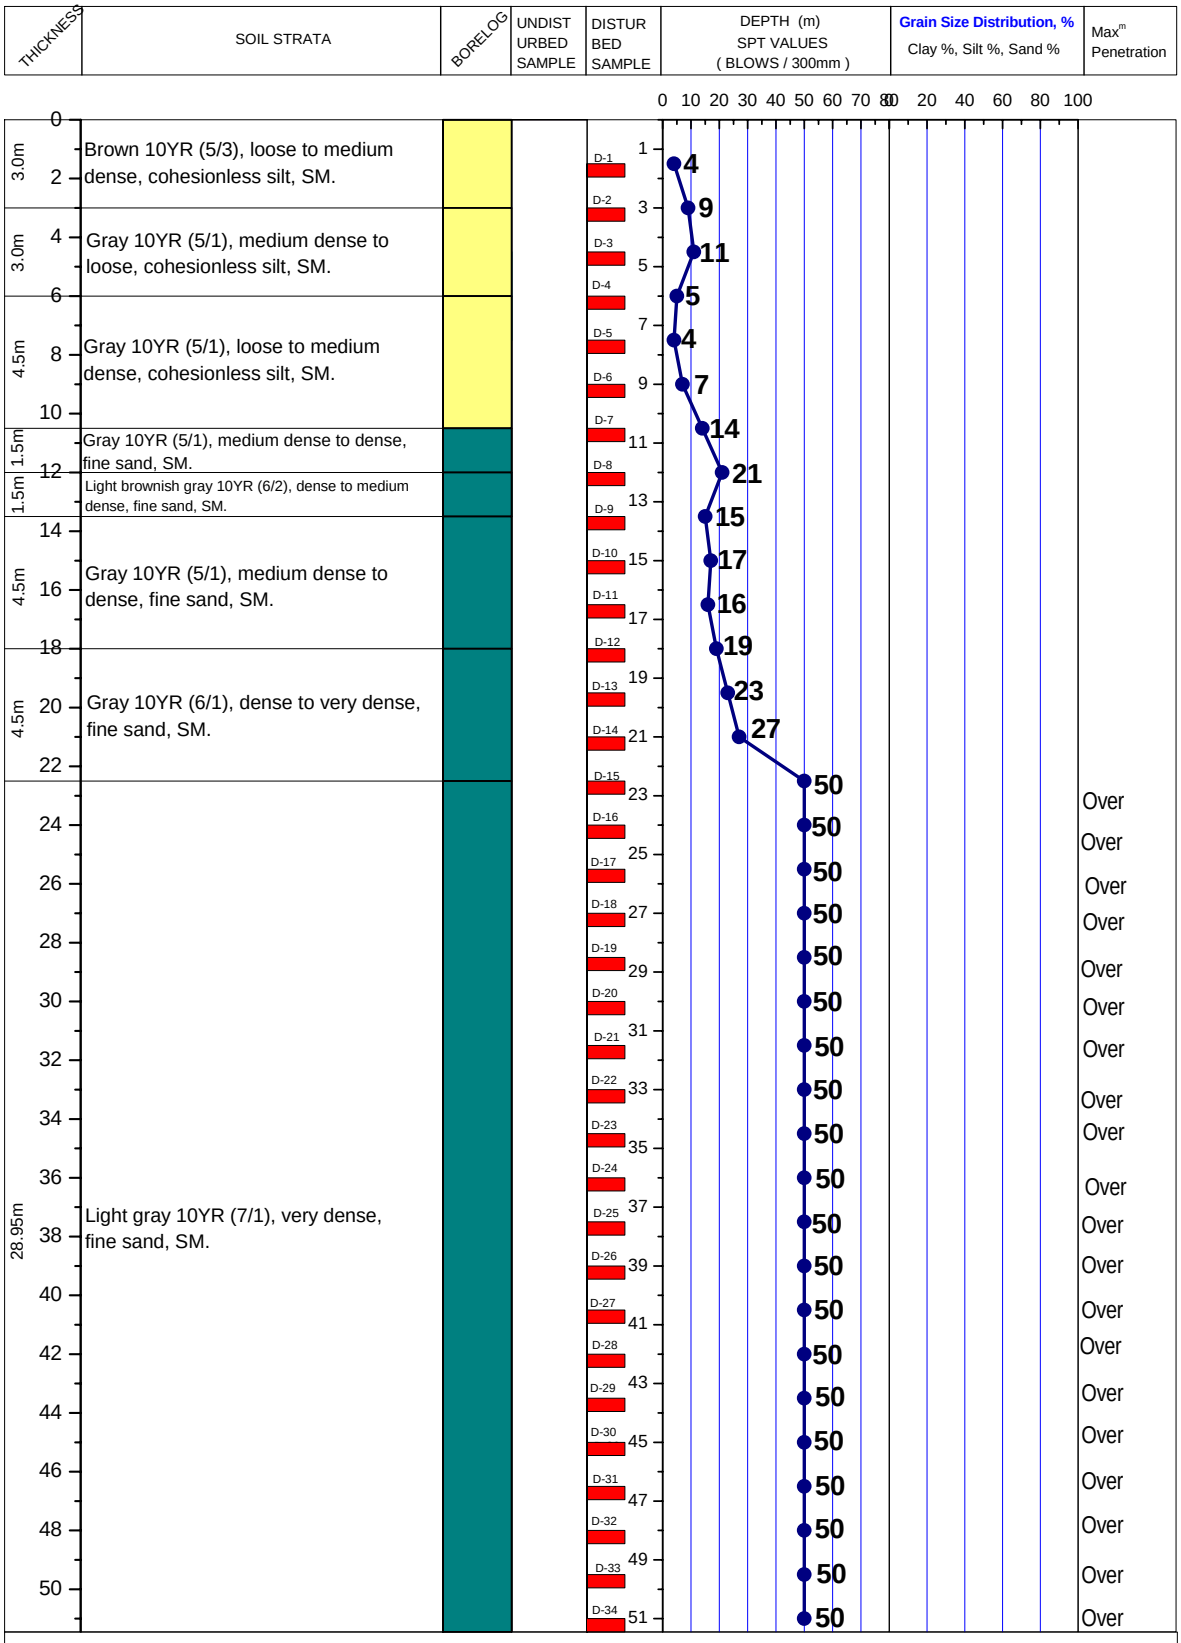

LEGEND FOR BORELOG AND GRAIN SIZE DISTRIBUTION

PLASTIC SILTY CLAY	NON PLASTIC SILT	ORGANIC	DISTURBED SAMPLE
LOW PLASTIC CLAYEY SILT	SAND	SHALE	UNDISTURBED SAMPLE

N- BLOWS DELIVERED PER FOOT BY A 140 LB HAMMER FALLING 30 INCHES

MAX^m PENETRATION= 50 BLOWS. AFTER 50 BLOWS PENETRATION DEPTH WERE MEASURED