A2	PROSOIL	BOREHOLE NO: BH-1	
		LOCATION: S. M. Pilot High School, Jangal Solimpur, Jafrabad, P. S: Sitakunda, Dist: Chittagong.	
PROJECT : Telecommunication Tower.		DEPTH OF BORING: 12.0m	R. L.: 0n Road Level.
CLIENT : AXIATA (Bangladesh) Ltd.		DATE OF BORING: 28-01-2015.	B. W. T : 0.61m below from E. G. L.

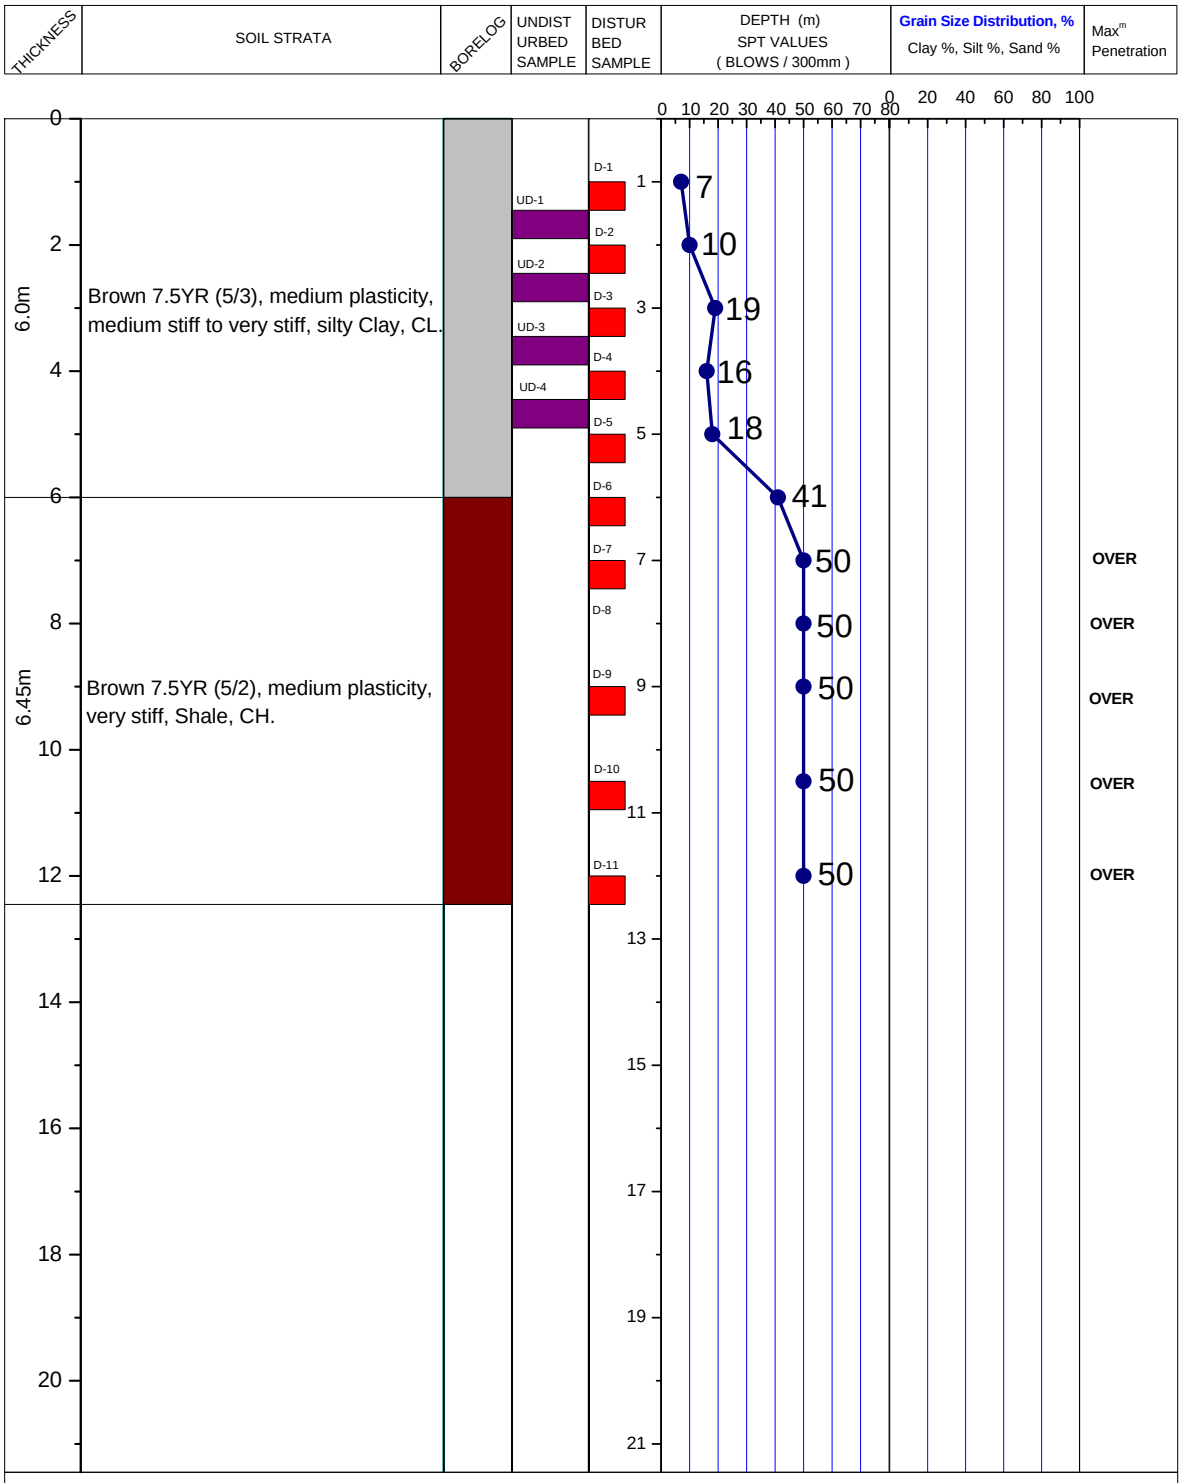

LEGEND FOR BORELOG AND GRAIN SIZE DISTRIBUTION (BASED ON 'ASTM CLASSIFICATION D-2487')

PLASTIC CLAY | SAND | SILT | SHALE

PEAT/HIGHLY ORGANIC SOIL | MICACEOUS FINE SAND/SILT | UNDISTURBED SAMPLE | DISTURBED SAMPLE

N- BLOWS DELIVERED PER FOOT BY A 140 LB HAMMER FALLING 30 INCHES

MAX^m PENETRATION= 50 BLOWS

AFTER 50 BLOWS PENETRATION DEPTH WERE MEASURED

XB

PROSOIL FOUNDATION CONSULTANT DHAKA-1205 68/B, INDIRA ROAD

Md. Shamsul Islam

(Engr. Md. Shamsul Islam)
B. Sc. Engg. (Civil, BUET),
M. Engg. (Geotech), MCSD, FIEB, CCPE
Chief Executive
Prosoil Foundation Consultant