A2 PROSOIL	BOREHOLE NO: 01	
	LOCATION : 34th km (34/1)(Ch: 33.414 to 33.444) (LRP 32b/c) of Munshigonj-Louhajong-Mawa Road.	
PROJECT : Proposed Munshigonj PC Girder Bridge.	DEPTH OF BORING : 51.0m	Chainage: 33+449 R. L. : 7.41
CLIENT : Road Division, Munshigonj.	DATE OF BORING : 16-04-2014 to 18-04-2014.	G. W. T : 1.83m below from E.G.L.

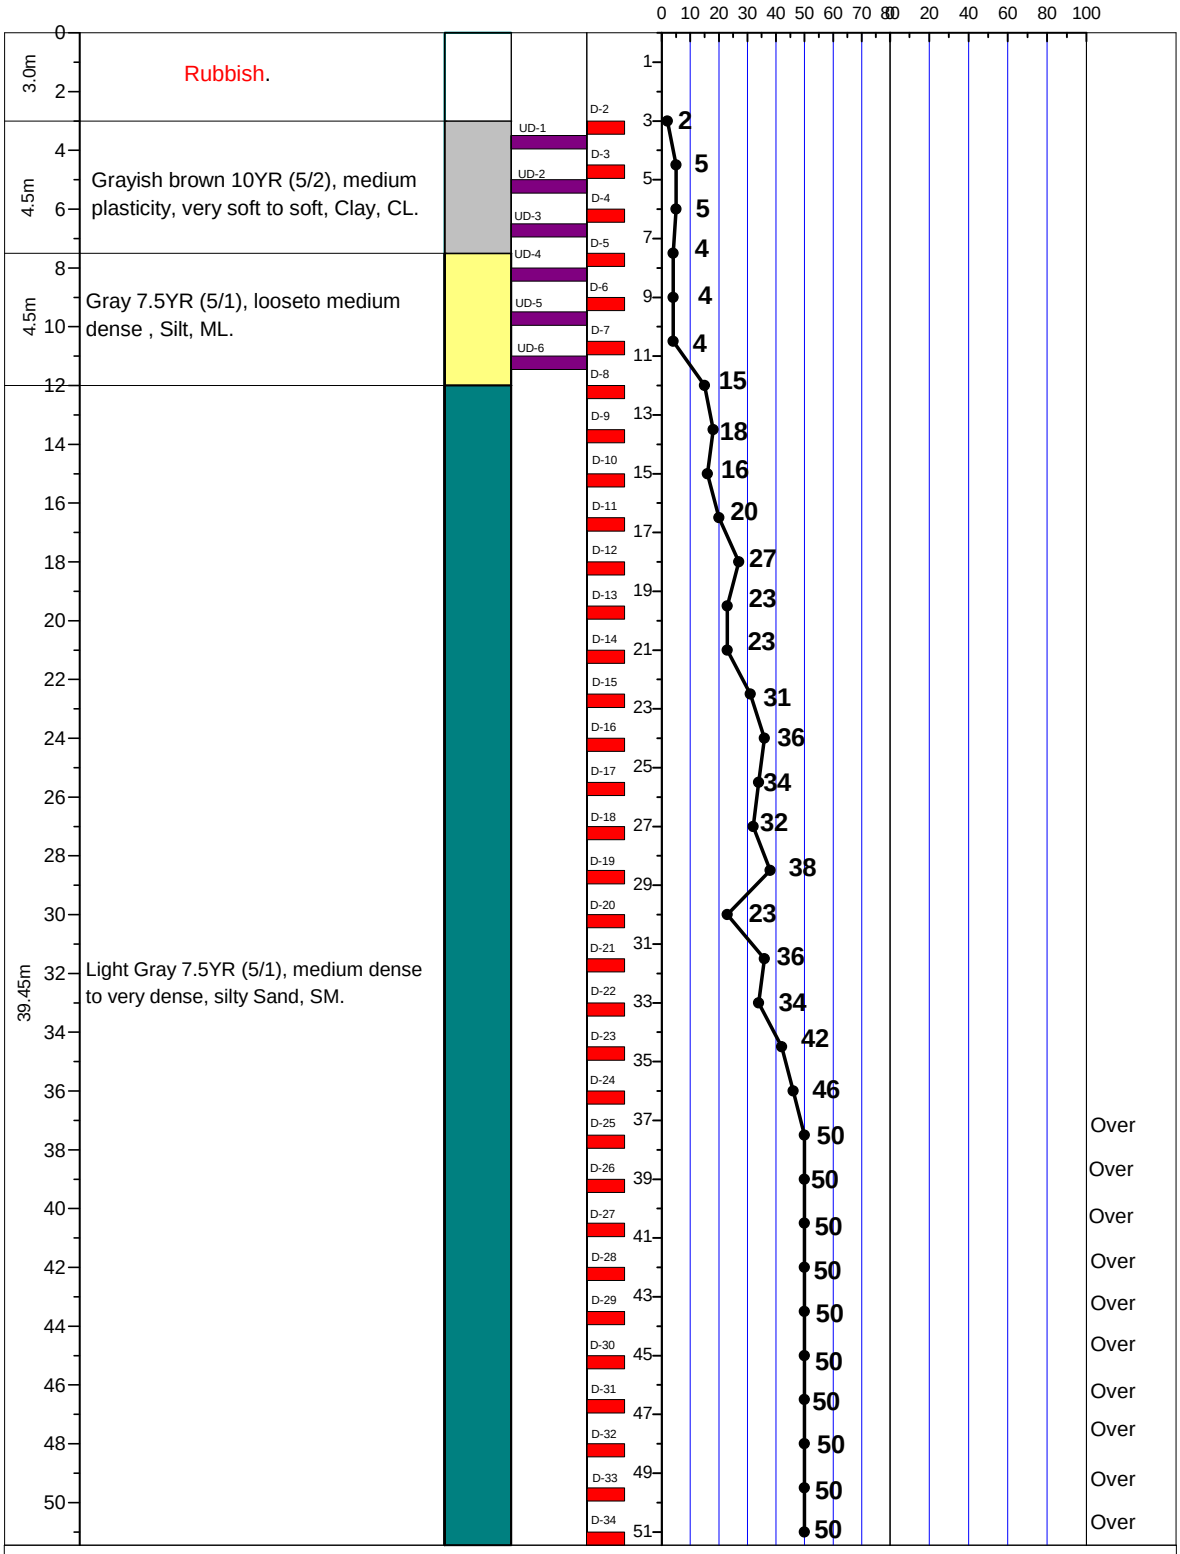

LEGEND FOR BOREHOLE AND GRAIN SIZE DISTRIBUTION (BASED ON 'ASTM CLASSIFICATION D-2487')

PLASTIC CLAY | SILT | PEAT/HIGHLY ORGANIC SOIL | UNDISTURBED SAMPLE

MICACEOUS FINE SAND/SILT | SAND | SHALE | DISTURBED SAMPLE

N- BLOWS DELIVERED PER FOOT BY A 140 LB HAMMER FALLING 30 INCHES

MAX^m PENETRATION= 50 BLOWS. AFTER 50 BLOWS PENETRATION DEPTH WERE MEASURED