A2	PROSOIL	BOREHOLE NO: BH-1 (Laxmipur End)	
		LOCATION : Road #R140, Road Name :Lalmai-Chandpur-Raipur-Laxmipur Road, LRP 80.90.	
PROJECT : Proposed Bridge LRP 80.90.		DEPTH OF BORING : 45.45m	Chainage: 416.921 R. L. : 6.384
CLIENT : Roads And Highways Department.		DATE OF BORING : 05-09-2012.	G. W. T : 2.499m below from E.G.L.

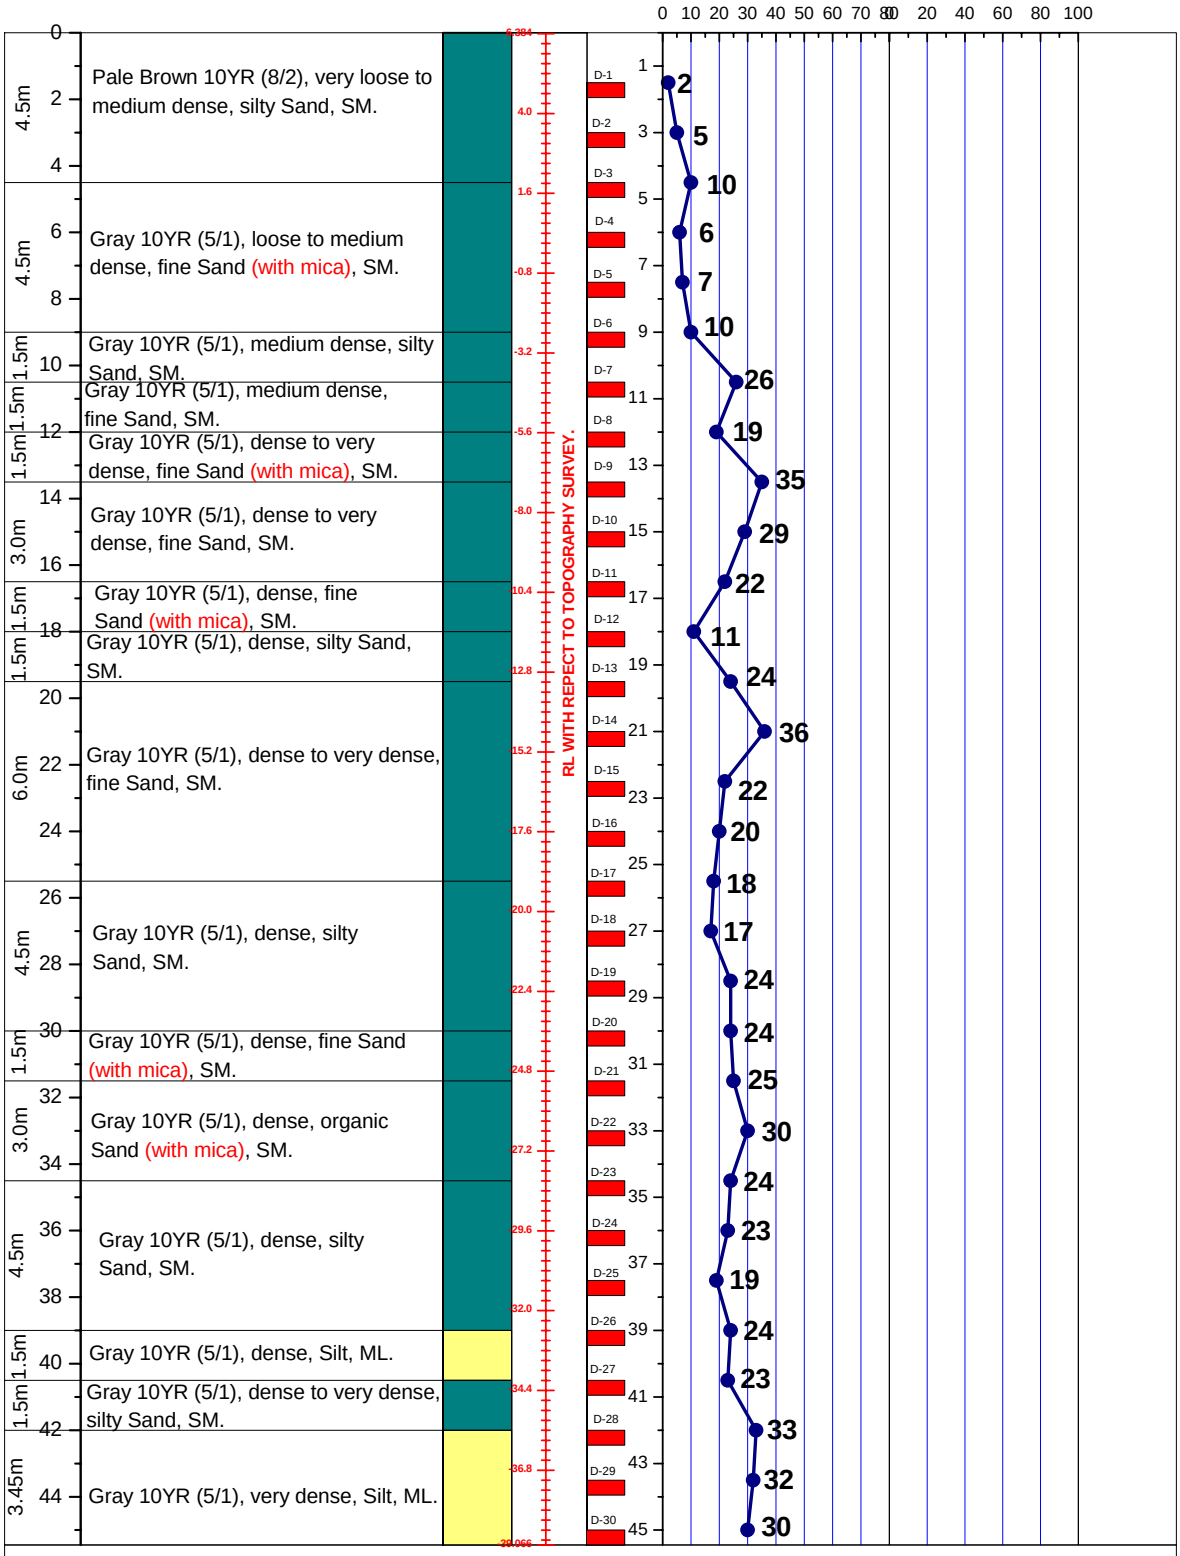

LEGEND FOR BORELOG AND GRAIN SIZE DISTRIBUTION (BASED ON 'ASTM CLASSIFICATION D-2487')

PLASTIC CLAY	SILT	PEAT/HIGHLY ORGANIC SOIL	UNDISTURBED SAMPLE
MICACEOUS FINE SAND/SILT	SAND	SHALE	DISTURBED SAMPLE

N- BLOWS DELIVERED PER FOOT BY A 140 LB HAMMER FALLING 30 INCHES

MAX^{m} PENETRATION= 50 BLOWS. AFTER 50 BLOWS PENETRATION DEPTH WERE MEASURED