A2	PROSOIL	BOREHOLE NO: BH-1	
		LOCATION : **Chainage 14+583.7 km on Darbost-Kanaight-Shahbag Road, Sylhet.**	
PROJECT : Proposed Bridge at 15th km from Chainage 14+583.7 to 14+635.4 km.		DEPTH OF BORING : 30.0m	**Chainage: 14+586.7** **R. L. : 8.61**
CLIENT : Road Division, Sylhet.		DATE OF BORING : 21-02-2010.	G. W. T : 0.91m below from E.G.L.

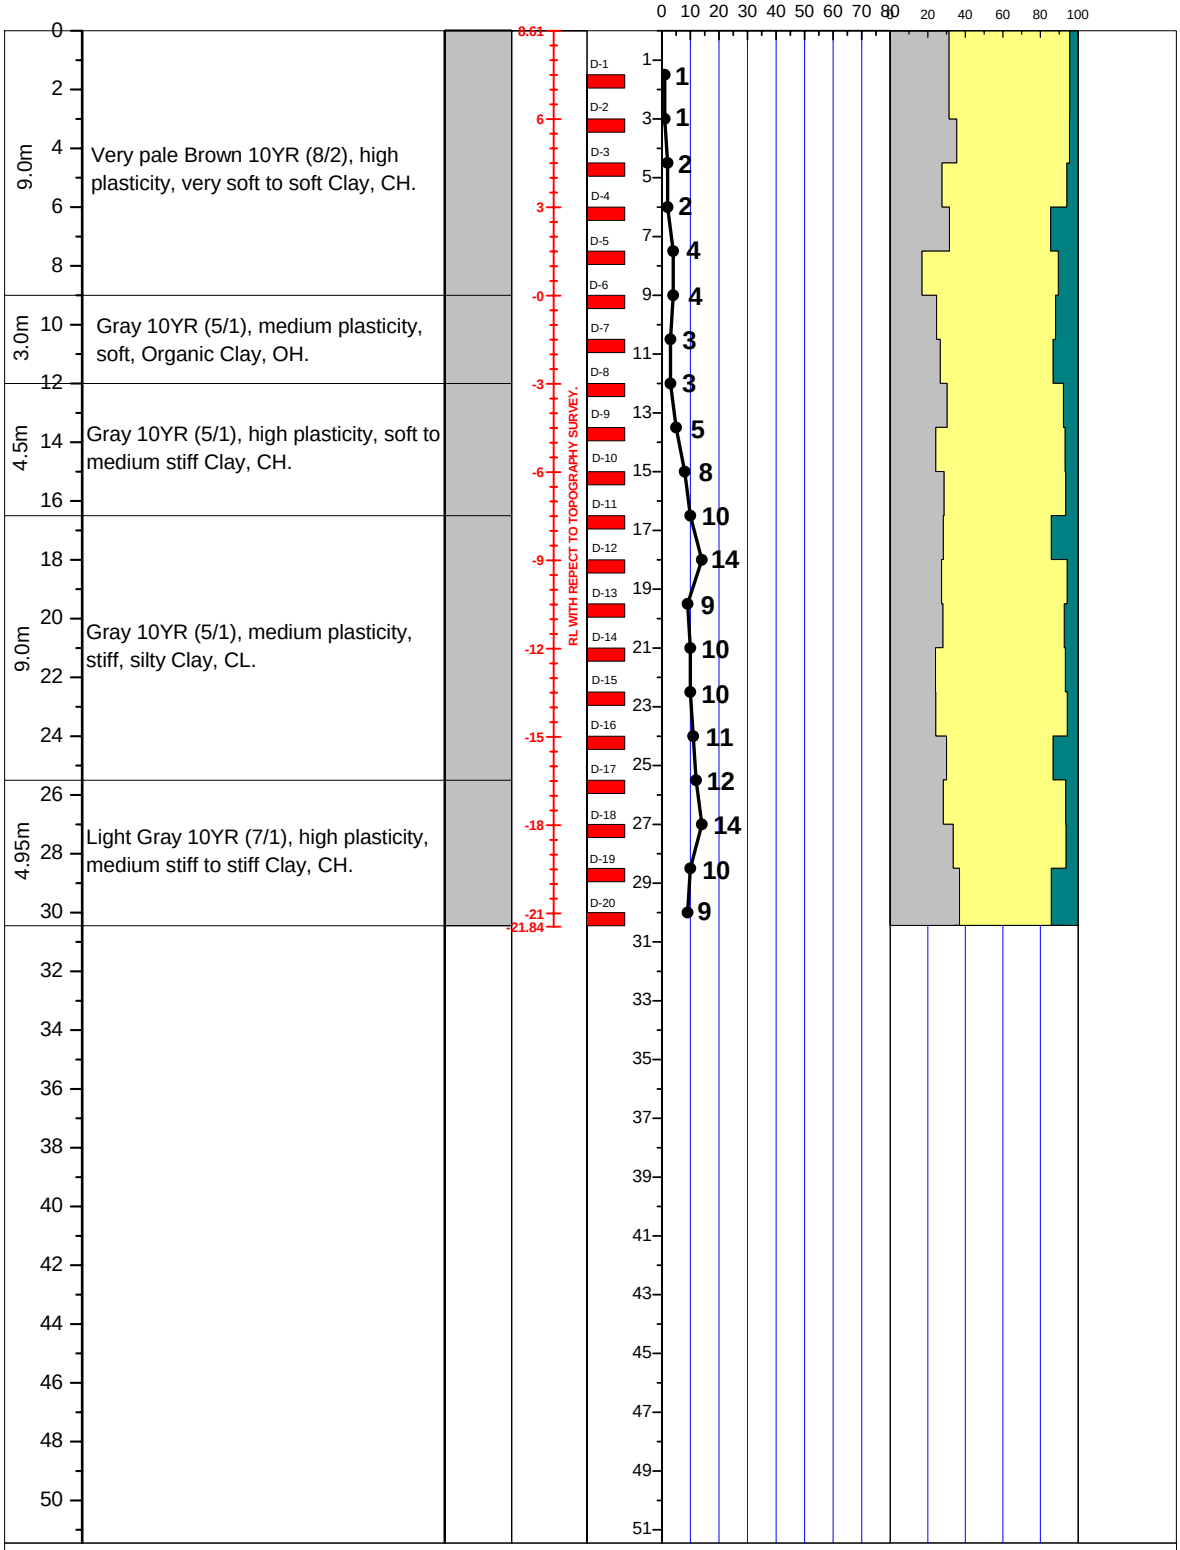

LEGEND FOR BORELOG AND GRAIN SIZE DISTRIBUTION (BASED ON 'ASTM CLASSIFICATION D-2487')

PLASTIC CLAY	SILT	PEAT/HIGHLY ORGANIC SOIL	UNDISTURBED SAMPLE
MICACEOUS FINE SAND/SILT	SAND	SHALE	DISTURBED SAMPLE

N- BLOWS DELIVERED PER FOOT BY A 140 LB HAMMER FALLING 30 INCHES

MAX^m PENETRATION= 50 BLOWS. AFTER 50 BLOWS PENETRATION DEPTH WERE MEASURED