A2	PROSOIL	BOREHOLE NO: BH-1	
		LOCATION : West Madda (Ward No.: 01), B. Baria.	
PROJECT : Proposed Six Storied Building.		DEPTH OF BORING : 15.0m	R. L.: Road Level.
CLIENT : Mohammad Johar Ali.		DATE OF BORING : 15-01-2008.	G. W. T : 1.52m below from E. G. L.

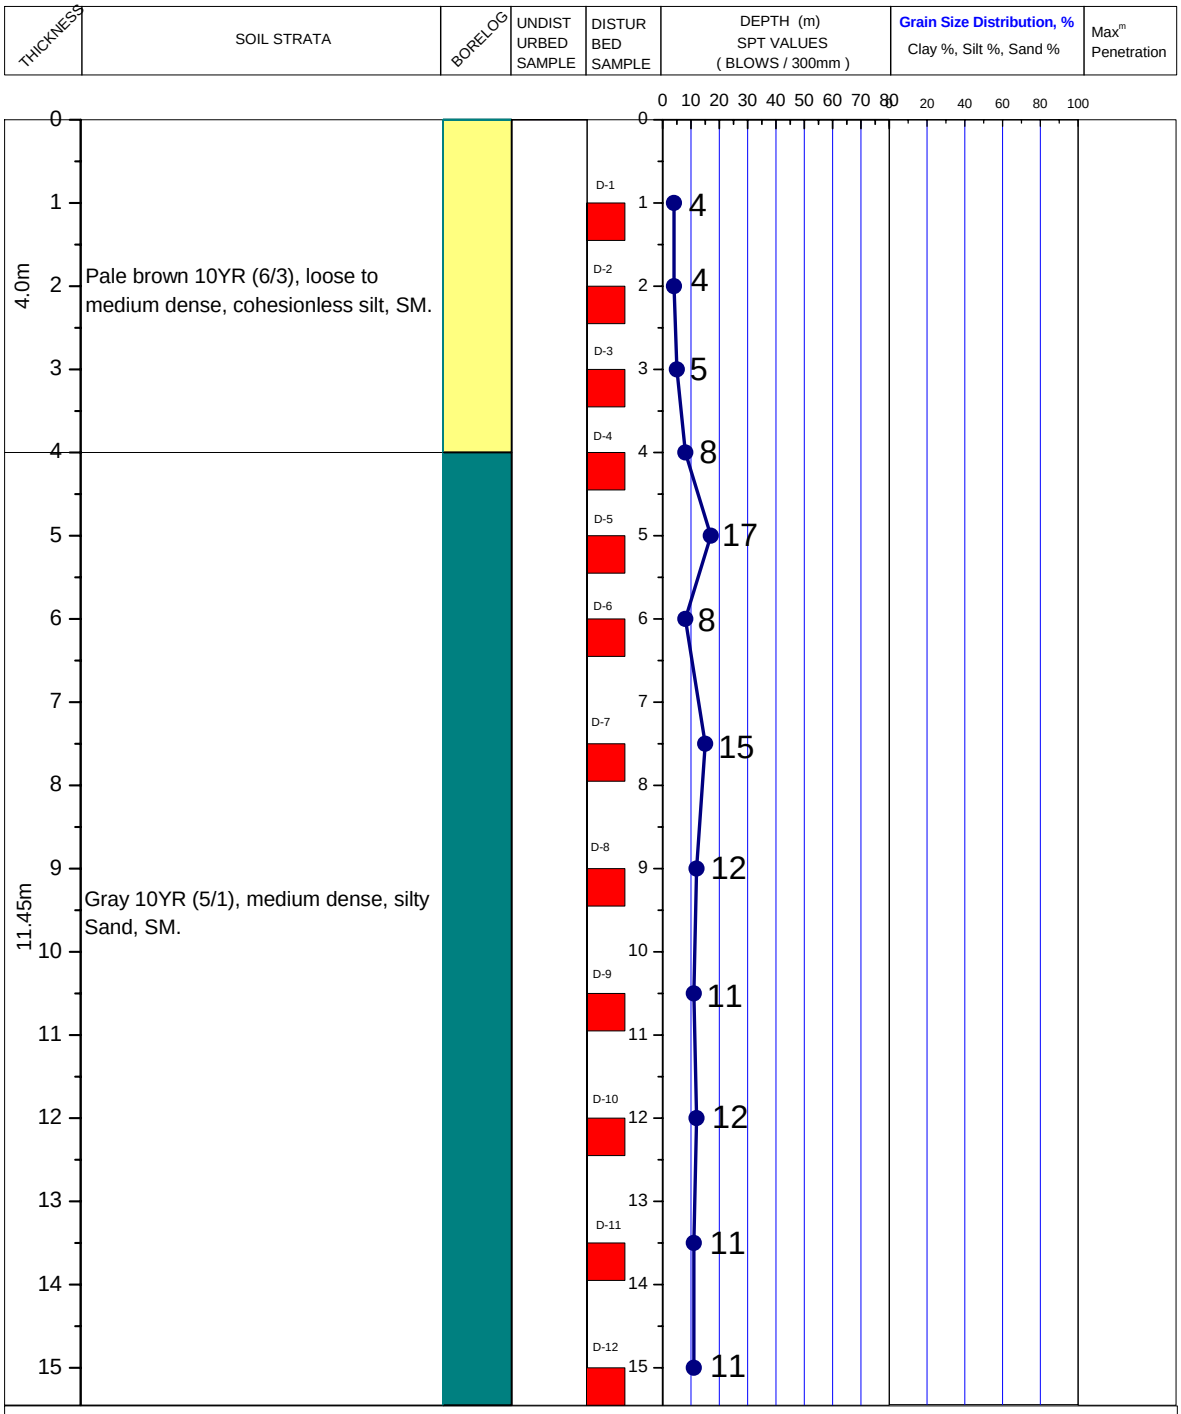

LEGEND FOR BORELOG AND GRAIN SIZE DISTRIBUTION

PLASTIC SILTY CLAY

LOW PLASTIC CLAYEY SILT

NON PLASTIC SILT

SAND

ORGANIC

UNDISTURBED SAMPLE

DISTURBED SAMPLE

SHALE

N- BLOWS DELIVERED PER FOOT BY A 140 LB HAMMER FALLING 30 INCHES

MAX^{m} PENETRATION= 50 BLOWS

AFTER 50 BLOWS PENETRATION DEPTH WERE MEASURED