
A2	PROSOIL	BOREHOLE NO: BH-1	
		LOCATION : **Chainage 10+000 km on Sari-Goainghat Road, Sylhet.**	
PROJECT : Proposed Bridge at Chainage 10+000.		DEPTH OF BORING : 45.0m	**Chainage: 10+035.3** **R. L. : 8.2**
CLIENT : Road Division, Sylhet.		DATE OF BORING : 17-02-2010.	G. W. T : 0.91m below from E.G.L.

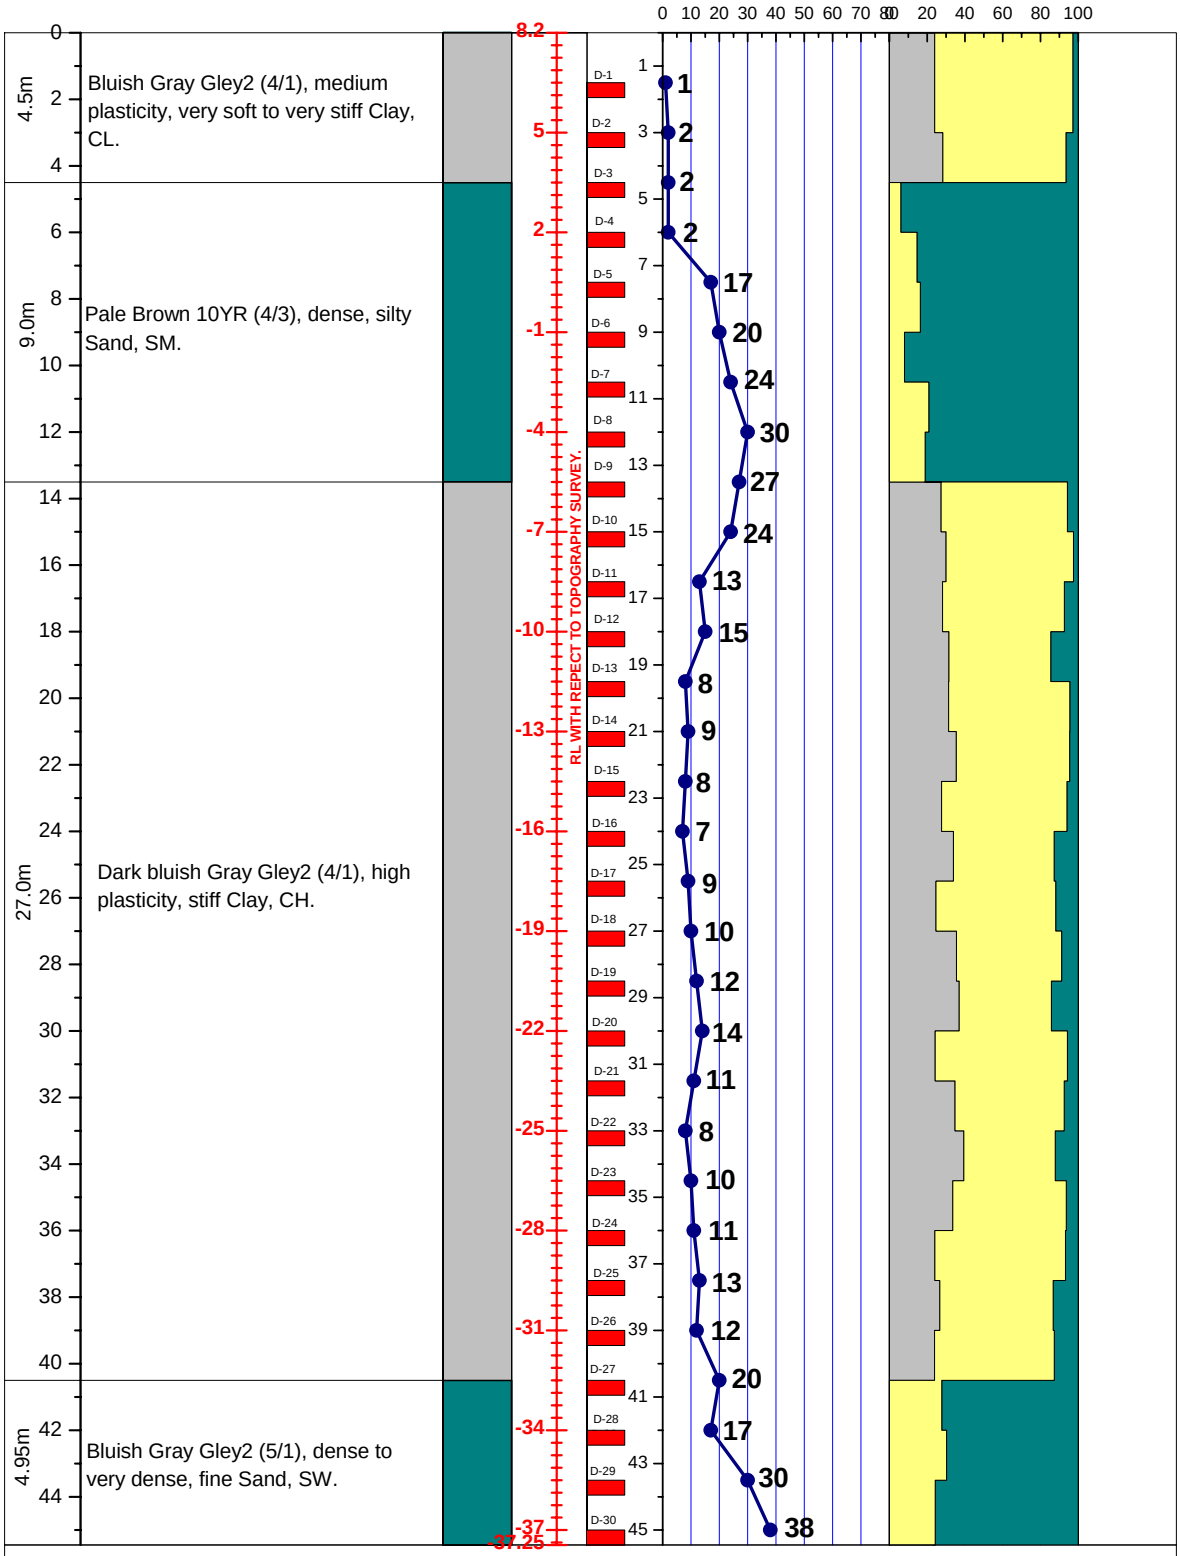

LEGEND FOR BORELOG AND GRAIN SIZE DISTRIBUTION (BASED ON 'ASTM CLASSIFICATION D-2487')

PLASTIC CLAY | SILT | PEAT/HIGHLY ORGANIC SOIL | UNDISTURBED SAMPLE

MICACEOUS FINE SAND/SILT | SAND | SHALE | DISTURBED SAMPLE

N- BLOWS DELIVERED PER FOOT BY A 140 LB HAMMER FALLING 30 INCHES

MAX^{m} PENETRATION= 50 BLOWS. AFTER 50 BLOWS PENETRATION DEPTH WERE MEASURED