A2 PROSOIL	BOREHOLE NO: BH-1	
	LOCATION : Dighirpar Dorbost, Jaflong road.	
PROJECT : Telecommunication Tower.	DEPTH OF BORING : 21.0m	R. L.: 0.73m below from Road Level.
CLIENT : Grameen phone Ltd.	DATE OF BORING : 31-12-2004	G. W. T : 2.44m below from E. G. L.

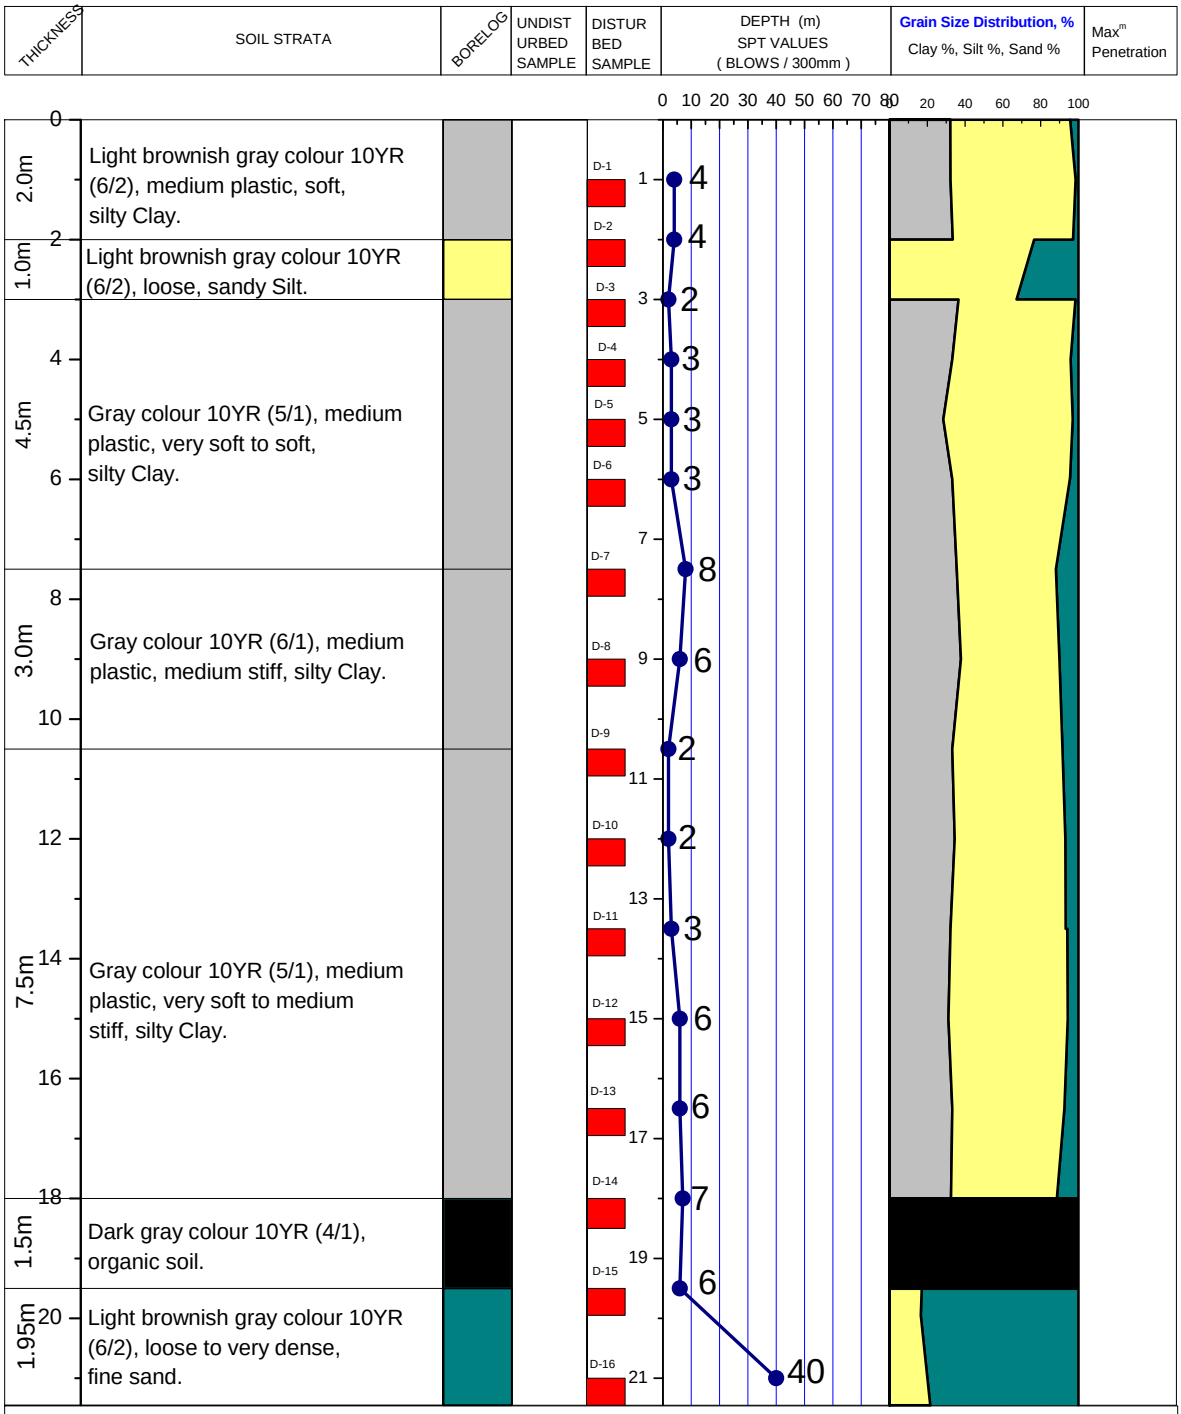

ID FOR BOREHOLE A RAIN SIZE DISTRIBU

PLASTIC SILTY CLAY

LOW PLASTIC CLAYEY SILT

NON PLASTIC SILT

SAND

UNDISTURBED SAMPLE

ORGANIC

DISTURBED SAMPLE

N- BLOWS DELIVERED PER FOOT BY A 140 LB HAMMER FALLING 30 INCHES

MAX^{m} PENETRATION= 50 BLOWS

AFTER 50 BLOWS PENETRATION DEPTH WERE MEASURED