
A2 PROSOIL	BOREHOLE NO: BH-1	
	LOCATION : Plot No-G.P.JA-73/1, Mohakhali, Gulshan, Dhaka-1212.	
PROJECT : Proposed Six Storied Building.	DEPTH OF BORING : 15.0m	R. L.: 0.45m above from Road Level.
CLIENT : Md.Giasuddin.	DATE OF BORING : 13-08-2008.	G. W. T : 3.04m below from E. G. L.

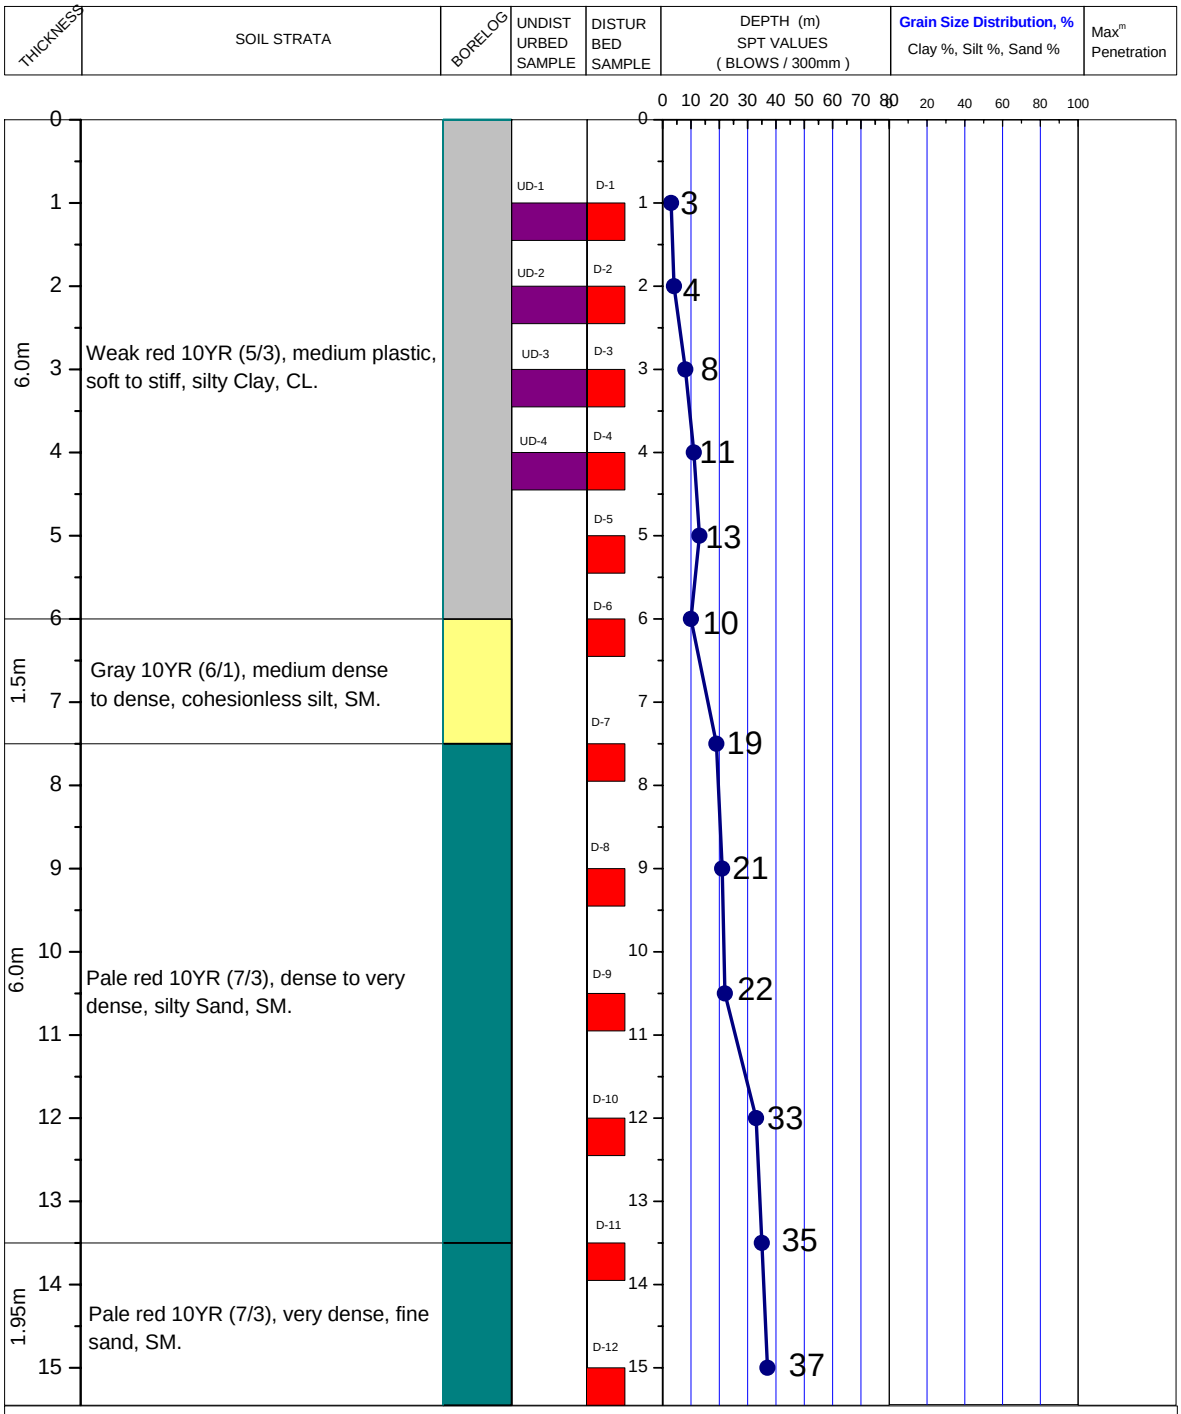

LEGEND FOR BORELOG AND GRAIN SIZE DISTRIBUTION

PLASTIC SILTY CLAY

LOW PLASTIC CLAYEY SILT

NON PLASTIC SILT

SAND

ORGANIC

UNDISTURBED SAMPLE

DISTURBED SAMPLE

SHALE

N- BLOWS DELIVERED PER FOOT BY A 140 LB HAMMER FALLING 30 INCHES

MAX^{m} PENETRATION= 50 BLOWS

AFTER 50 BLOWS PENETRATION DEPTH WERE MEASURED