A2 PROSOIL	BOREHOLE NO: BH-1	
	LOCATION :C.S#94, R.S#119, Gazipura, Word#11, 27 Gazipura Road, Tongi.	
PROJECT : Proposed Seven(7) Storied Building.	DEPTH OF BORING : 21.0m	R. L.: On Road Level.
CLIENT : CITY AXIS LTD.	DATE OF BORING: 23-02-2011.	G. W. T : 0.91m below from E.G.L.

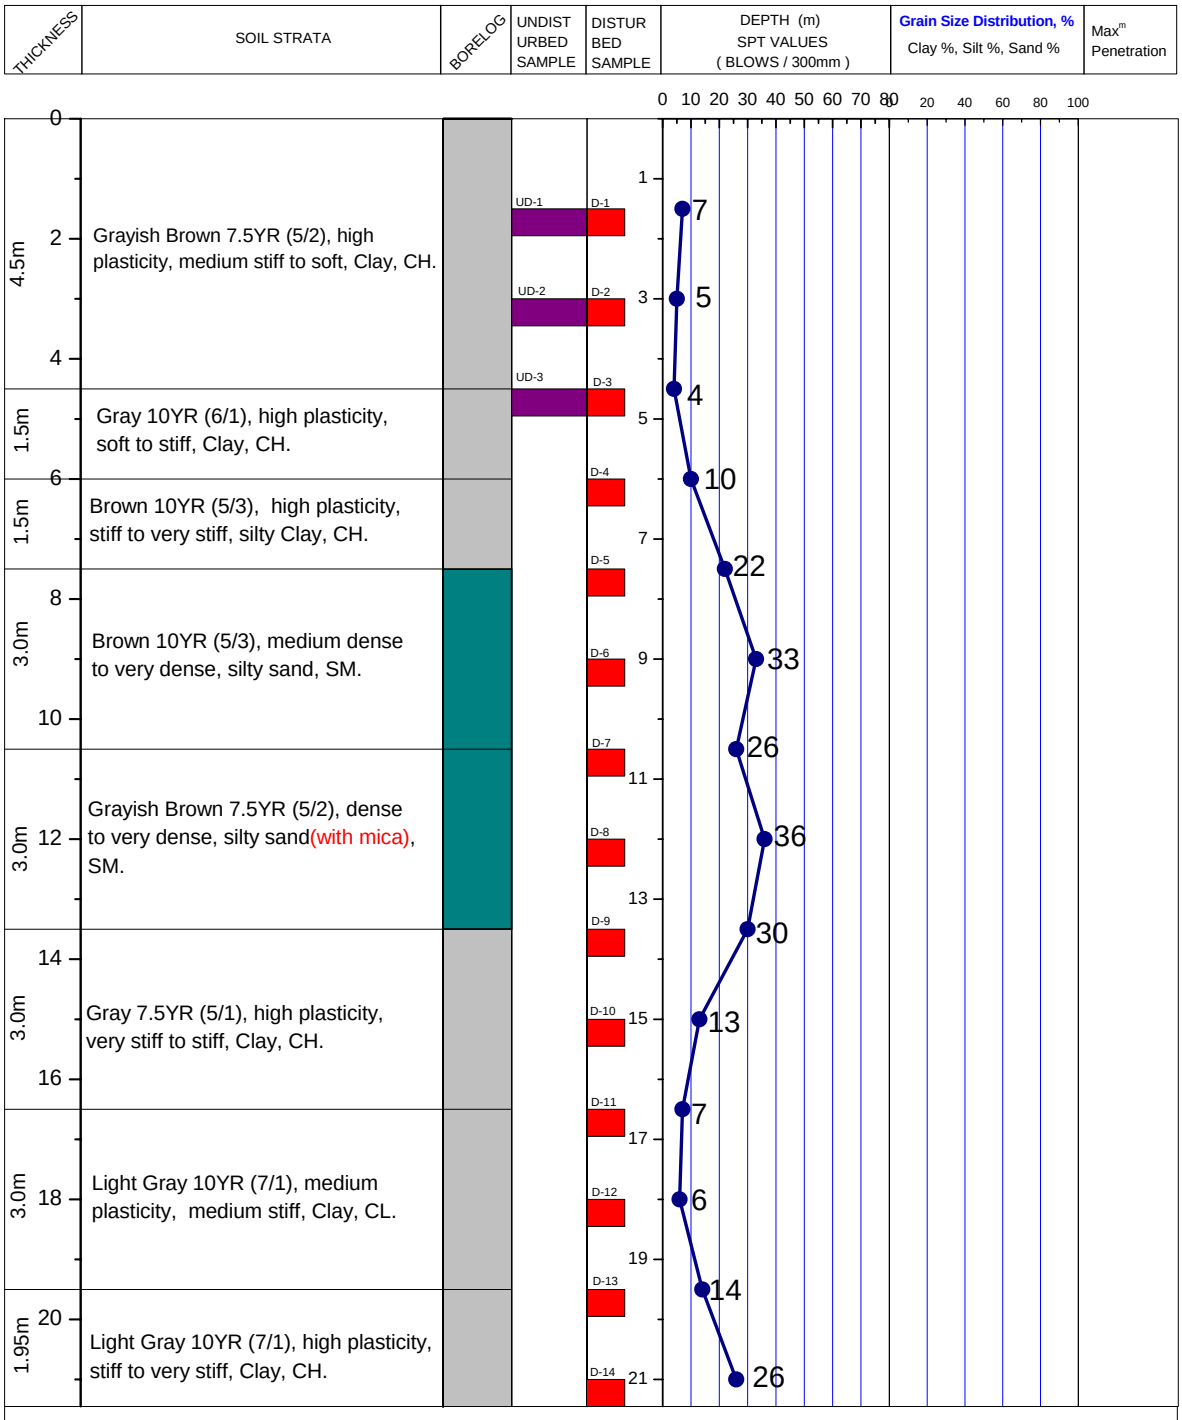

LEGEND FOR BORELOG AND GRAIN SIZE DISTRIBUTION (BASED ON 'ASTM CLASSIFICATION D-2487')

PLASTIC CLAY	SAND	SHALE	UNDISTURBED SAMPLE
MICACEOUS FINE SAND/SILT	SILT	PEAT/HIGHLY ORGANIC SOIL	DISTURBED SAMPLE

N- BLOWS DELIVERED PER FOOT BY A 140 LB HAMMER FALLING 30 INCHES

MAX^{m} PENETRATION= 50 BLOWS

AFTER 50 BLOWS PENETRATION DEPTH WERE MEASURED