A2	PROSOIL	BOREHOLE NO: BH-1	
		LOCATION: The Station commander, Station Head Quarter, Bogra Cantonment, Bogra.	
PROJECT : Telecommunication Tower.		DEPTH OF BORING: 21.0m	R. L.: Too far from Road Level.
CLIENT : Grameenphone Ltd.		DATE OF BORING: 20-07-2013.	G. W. T : 3.05m below from E. G. L.

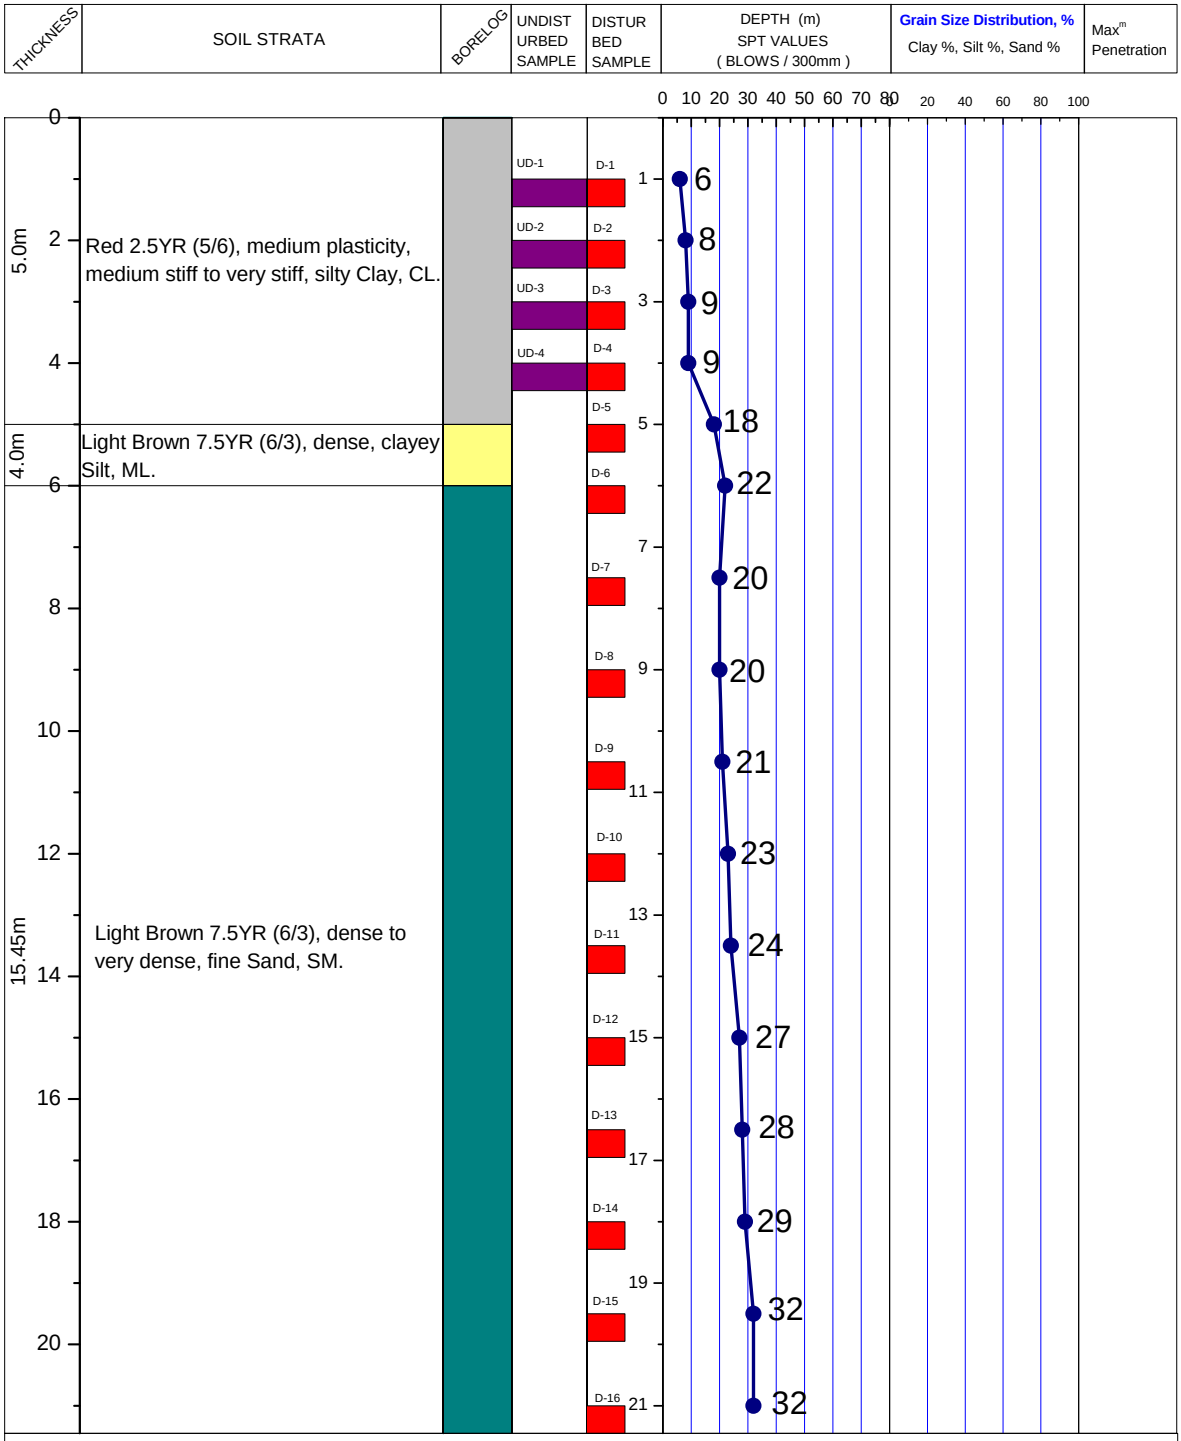

LEGEND FOR BORELOG AND GRAIN SIZE DISTRIBUTION (BASED ON 'ASTM CLASSIFICATION D-2487')

PLASTIC CLAY	SHALE	SILT	SAND
PEAT/HIGHLY ORGANIC SOIL	MICACEOUS FINE SAND/SILT	UNDISTURBED SAMPLE	DISTURBED SAMPLE

N- BLOWS DELIVERED PER FOOT BY A 140 LB HAMMER FALLING 30 INCHES

MAX^{m} PENETRATION= 50 BLOWS

AFTER 50 BLOWS PENETRATION DEPTH WERE MEASURED