A2	PROSOIL	BOREHOLE NO: BH-01	
		LOCATION : Bow Bazar, Sylhet.	
PROJECT : BOW BAZAR BRIDGE.		DEPTH OF BORING : 51.0m	Chainage: R. L. : 3.96m.
CLIENT : Road Division, Sylhet.		DATE OF BORING : 21-06-2015.	B. W. T : 0.91m below from E.G.L.

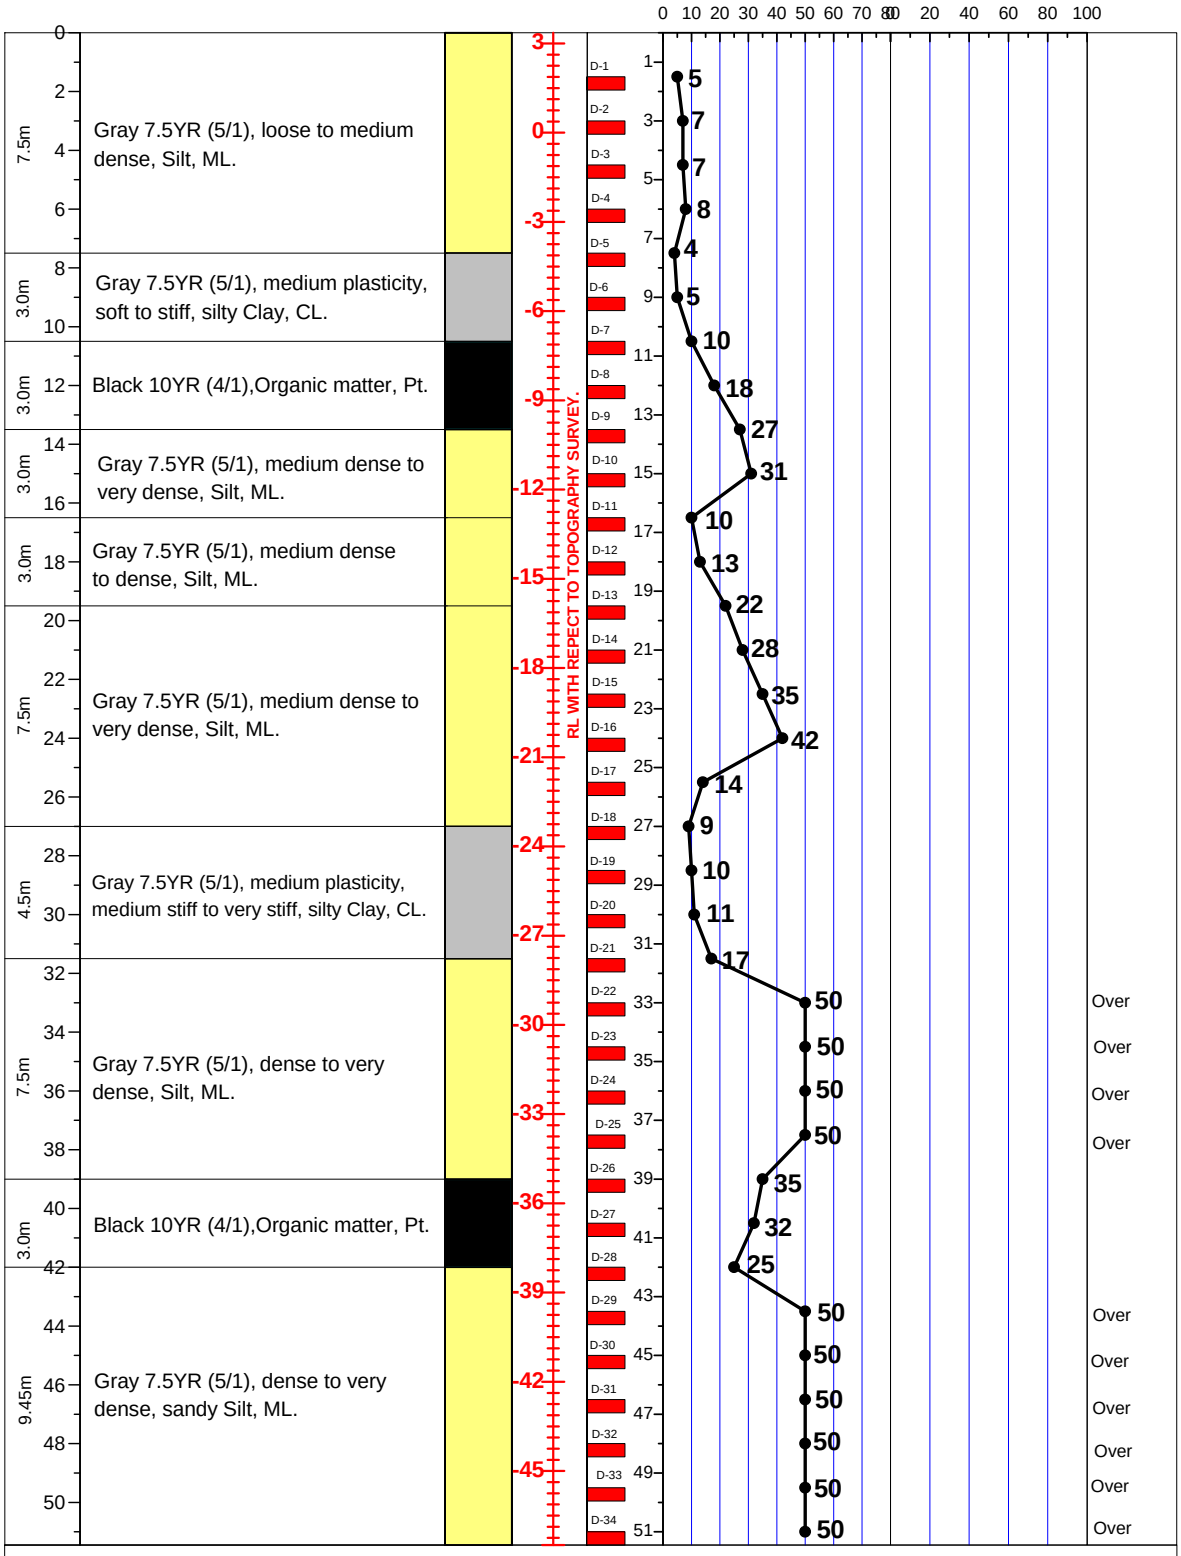

LEGEND FOR BORELOG AND GRAIN SIZE DISTRIBUTION (BASED ON 'ASTM CLASSIFICATION D-2487')

PLASTIC CLAY	SILT	PEAT/HIGHLY ORGANIC SOIL	UNDISTURBED SAMPLE
MICACEOUS FINE SAND/SILT	SAND	SHALE	DISTURBED SAMPLE

N- BLOWS DELIVERED PER FOOT BY A 140 LB HAMMER FALLING 30 INCHES

MAX^{m} PENETRATION= 50 BLOWS. AFTER 50 BLOWS PENETRATION DEPTH WERE MEASURED