
A2	PROSOIL	Borehole No: BH-01	
		Location: Bisho Road Jame Masjid, Narayanganj.	
NAME OF PROJECT: Commercial Complex Shimanto Towar.		Borehole Depth: 30.0m	R.L.: 1.948m
CLIENT: 62 BGB.		Date of Boring: 29-11-2020 to 01-12-2020	B. W. T : 1.5m above from E. G. L.

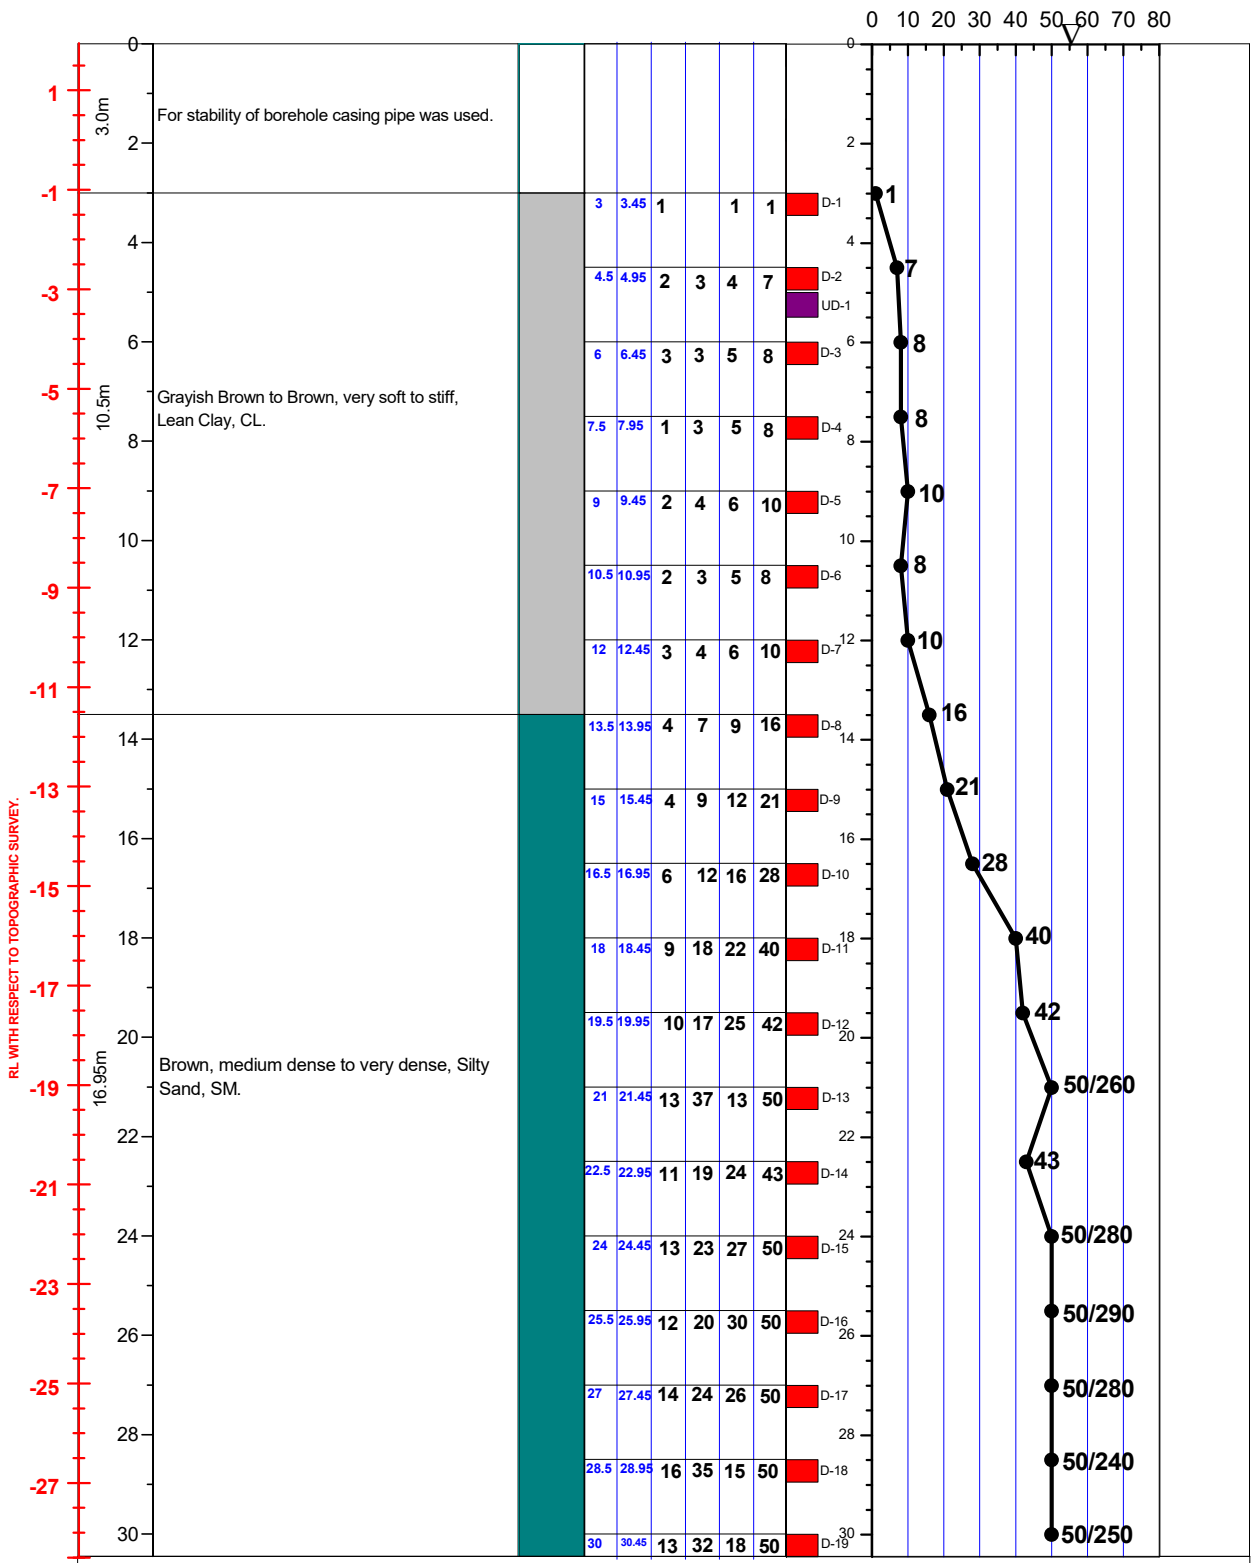

LEGEND FOR BORELOG AND GRAIN SIZE DISTRIBUTION (BASED ON 'ASTM CLASSIFICATION D-2487')

PLASTIC CLAY	SILT	PEAT/HIGHLY ORGANIC SOIL	UNDISTURBED SAMPLE
MICACEOUS FINE SAND/SILT	SAND	SHALE	DISTURBED SAMPLE

N- BLOWS DELIVERED PER FOOT BY A 140 LB HAMMER FALLING 30 INCHES

MAX^m PENETRATION= 50 BLOWS. AFTER 50 BLOWS PENETRATION DEPTH WERE MEASURED