
A2	PROSOIL	BOREHOLE NO: BH-1	
		LOCATION : Chintemoni, Balaganj, Sylhet. (24°25'47.3142"N, 91°34'05.3840"E).	
PROJECT : Chintemoni GPS, (Multi-purpose Cyclone Shelter/Govt. Primary School).		DEPTH OF BORING : 24.0m	R. L.: On Road Level.
CLIENT : US Army Corps of Engr, Alaska District. THROUGH : AUSPICIOUS, QA Contractor.		DATE OF BORING: 16-04-2013.	G. W. T : 4.08m below from E.G.L.

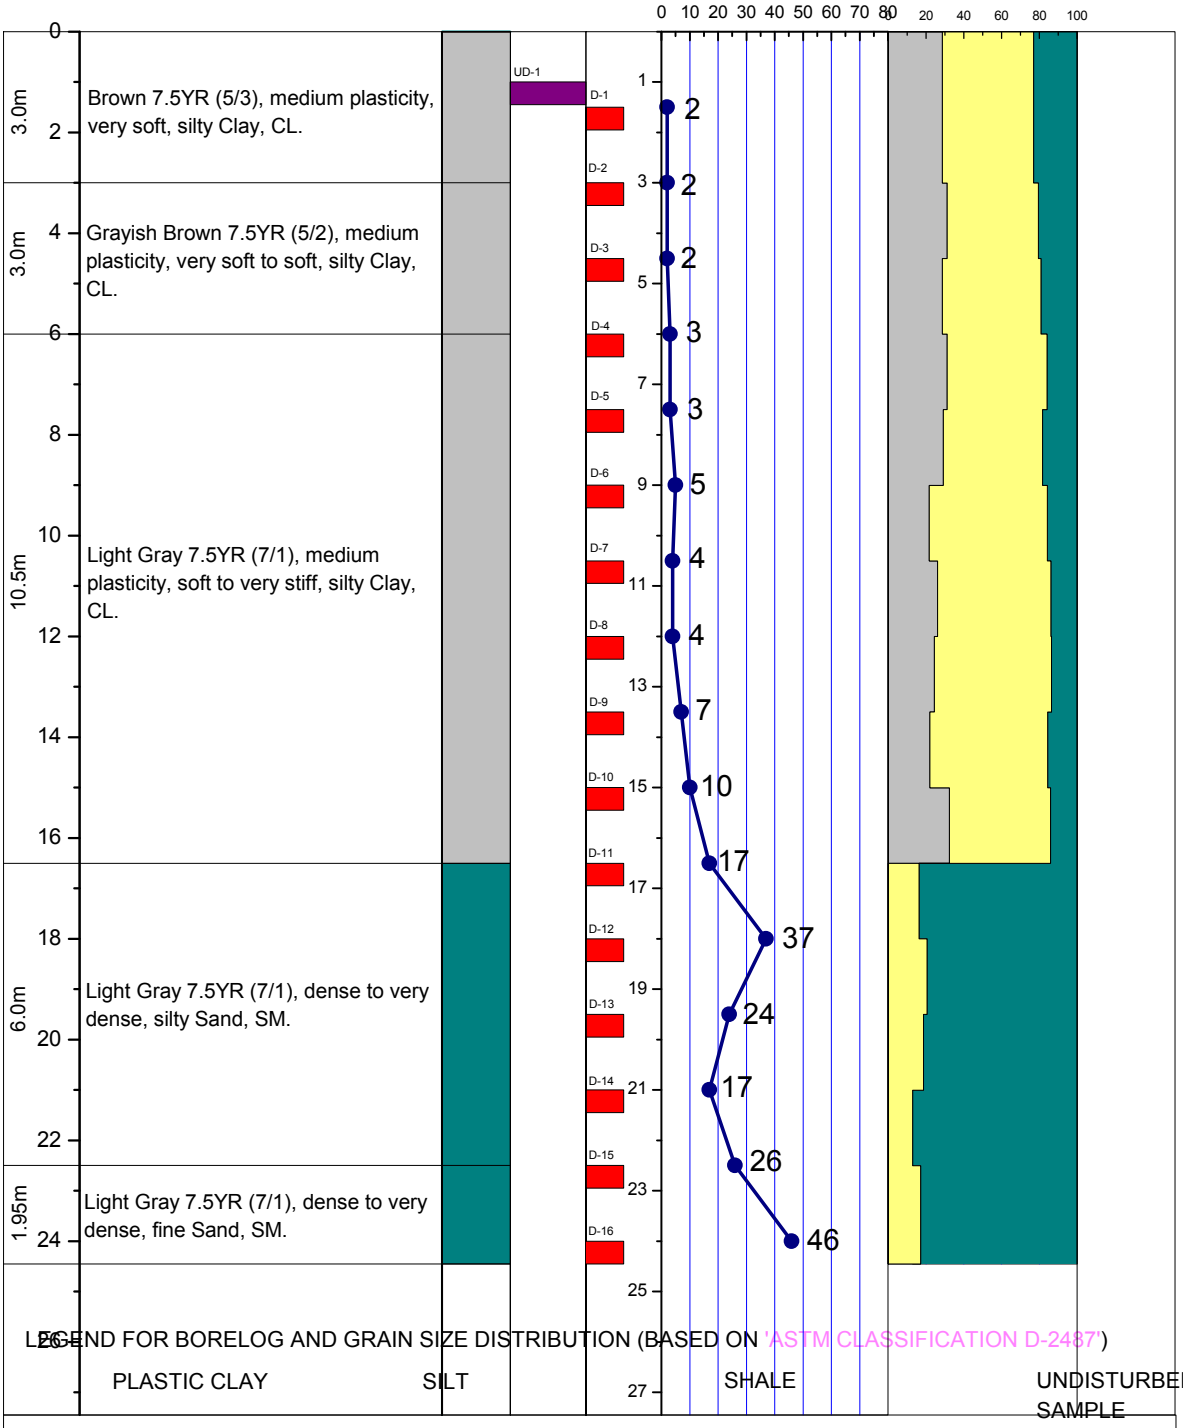

LEGEND FOR BOREHOLE AND GRAIN SIZE DISTRIBUTION (BASED ON 'ASTM CLASSIFICATION D-2487')

PLASTIC CLAY

SILT

SHALE

UNDISTURBED SAMPLE

MICACEOUS FINE SAND/SILT

SAND


PEAT/HIGHLY ORGANIC SOIL

DISTURBED SAMPLE

N- BLOWS DELIVERED PER FOOT BY A 140 LB HAMMER FALLING 30 INCHES

MAX^m PENETRATION= 50 BLOW
AFTER 50 BLOWS PENETRATIO TH WERE MEASURED

A6	PROSOIL	BOREHOLE NO: BH-1 (SETTLEMENT CALCULATION)
		LOCATION : Chintemoni, Balaganj, Sylhet. (24°25'47.3142"N, 91°34'05.3840"E).
PROJECT : Chintemoni GPS, (Multi-purpose Cyclone Shelter/Govt. Primary School)		SHALLOW FOOTING: B: 0.6m, L=0.9m, P=100kpa
CLIENT : US Army Corps of Engr, Alaska District. THROUGH : AUSPICIOUS, QA Contractor.		Shear failure Safety Factor=0.3

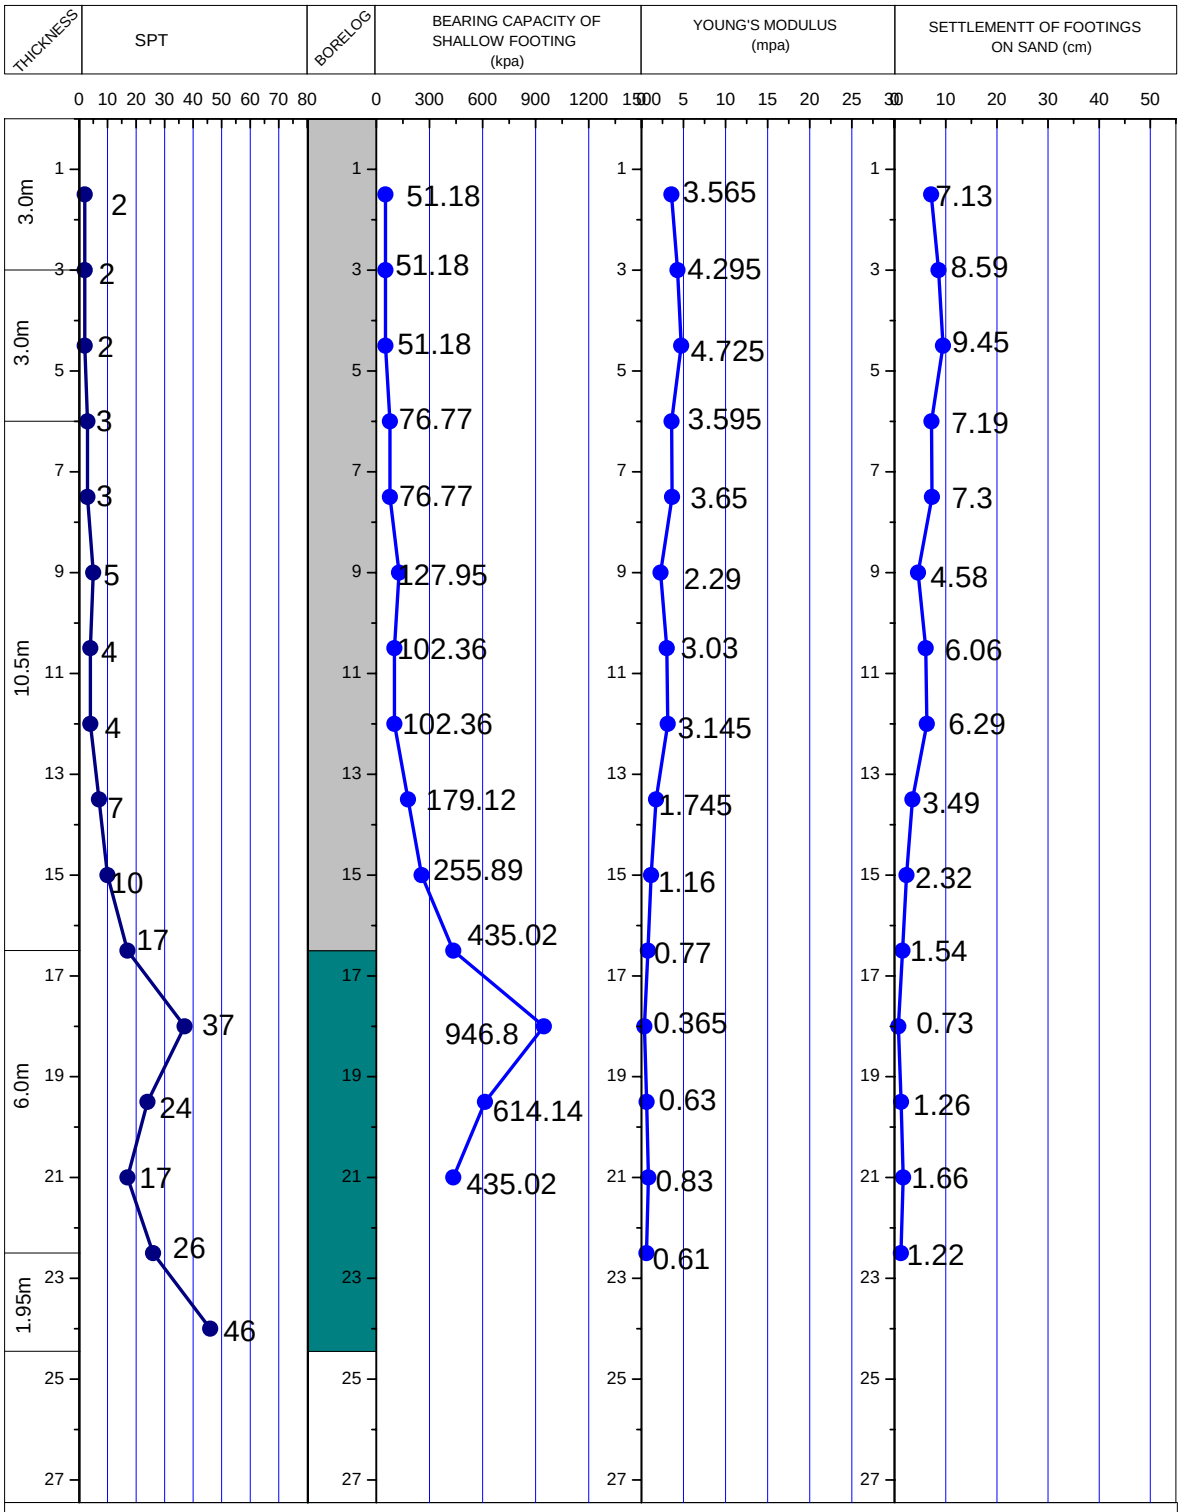

LEGEND FOR BORELOG AND GRAIN SIZE DISTRIBUTION (BASED ON 'ASTM CLASSIFICATION D-2487')

PLASTIC CLAY	SILT	SHALE	UNDISTURBED SAMPLE
MICACEOUS FINE SAND/SILT	SAND	PEAT/HIGHLY ORGANIC SOIL	

SETTLEMENT CALCULATION BY SOFTWARE: NOVO SPT CORRELATION PROGRAM.